


Powered by FRAMECAD Structure ®

Minimum number of fasteners required is 2 per joint

SHS

WELD SHS

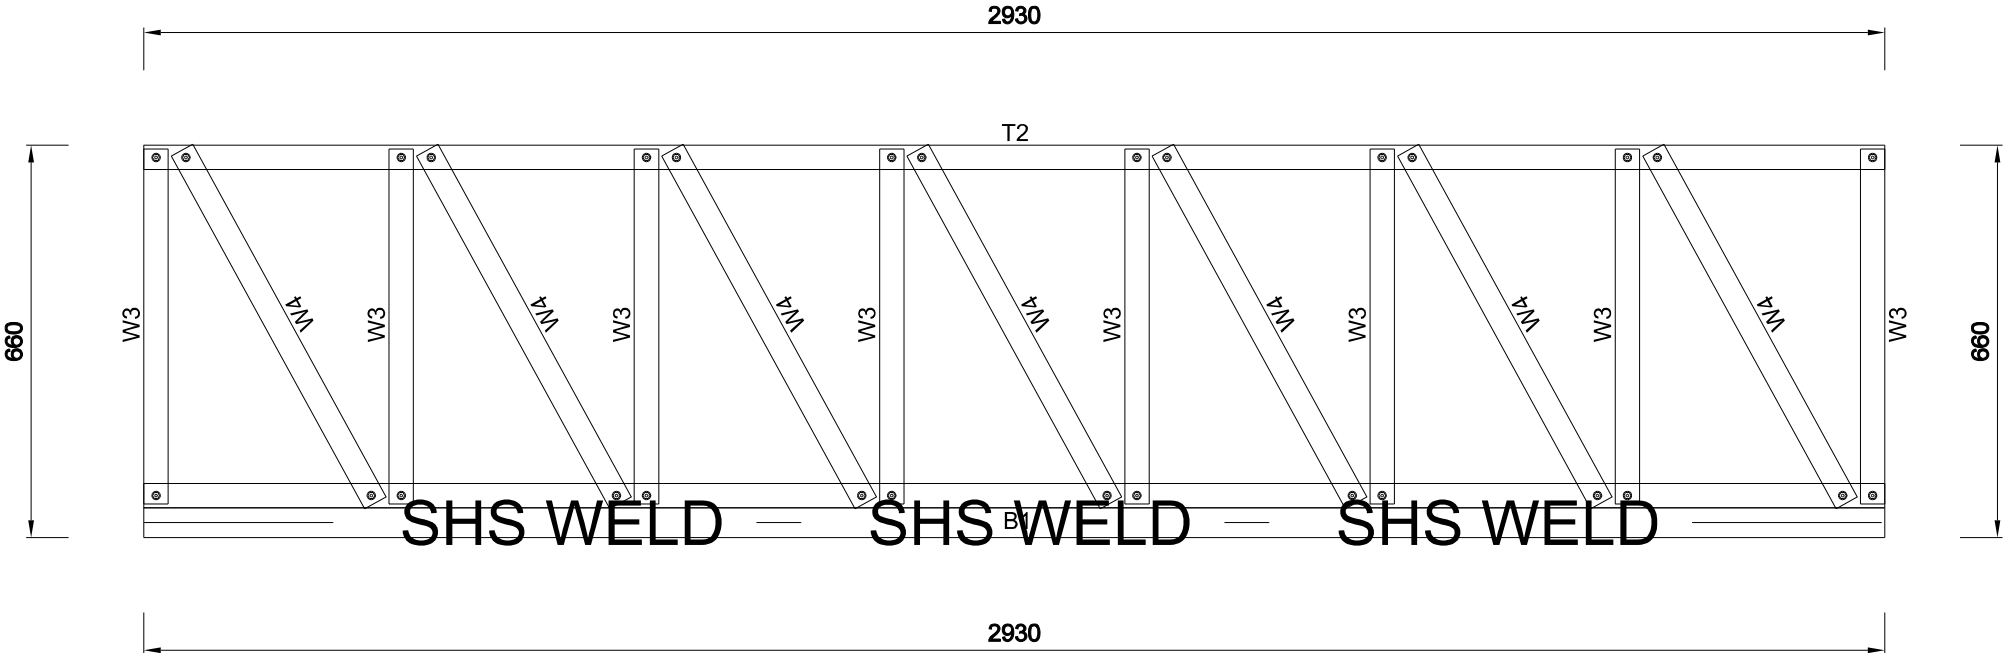

150x50x4 RHS

Quantity Required = 1 Mark as B9100 Engineering Status = Support Missing