


MARK	QTY	LENGTH
B9215(RHS)	1	5480

FAB BY	NAME	
	DATE	
CHECK BY	NAME	
	DATE	

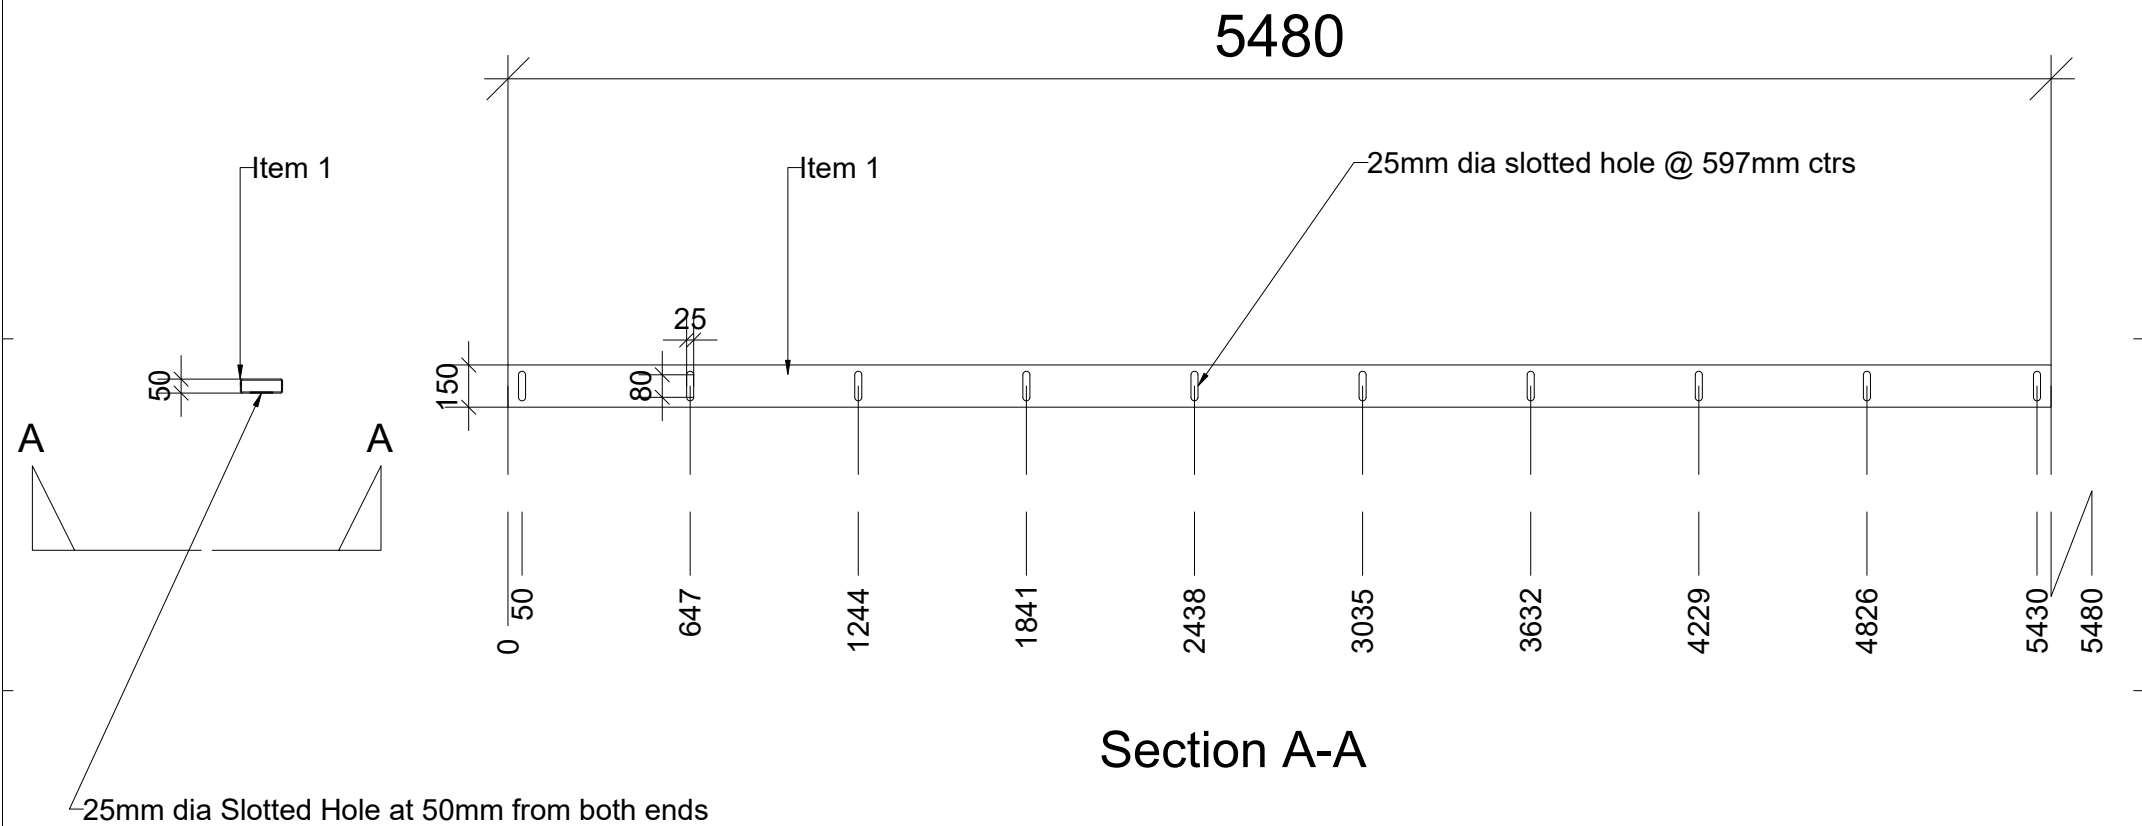

ITEM	QTY	MATERIAL	LENGTH	NOTE	FINISH
1	1	150x50x4 RHS	5480	25 dia Slotted hole	New - Paint

 www.austruss.com.au (02) 4860 1400	DRAWN A.George Ph:	ISSUE	DATE	DESCRIPTION OF REVISION	Client/Company Name	Project Name	Building / Zone / Area	Job Number	
		A	18/09/26	IEC	Interior Works	IMHC Cumberland	Level 9 Zone 2	25010	
DWG FILE: 25010-LGS-L2-020 [A] LEVEL L2 - Structure File					Project Address Dragonfly Dr, Westmead, NSW, 2145		Drawing Name B9215 RHS	Drawing Number 25010 - LGS - L9 - B9215 RHS	Revision A
					NOTE: USE PROVIDED DIMENSIONS ONLY. IF NOT PROVIDED, ASK.		Scale: 1 : 300		