


WELD ALL

GUSSET

OVERALL HEIGHT = 2267

HEIGHT = 2104

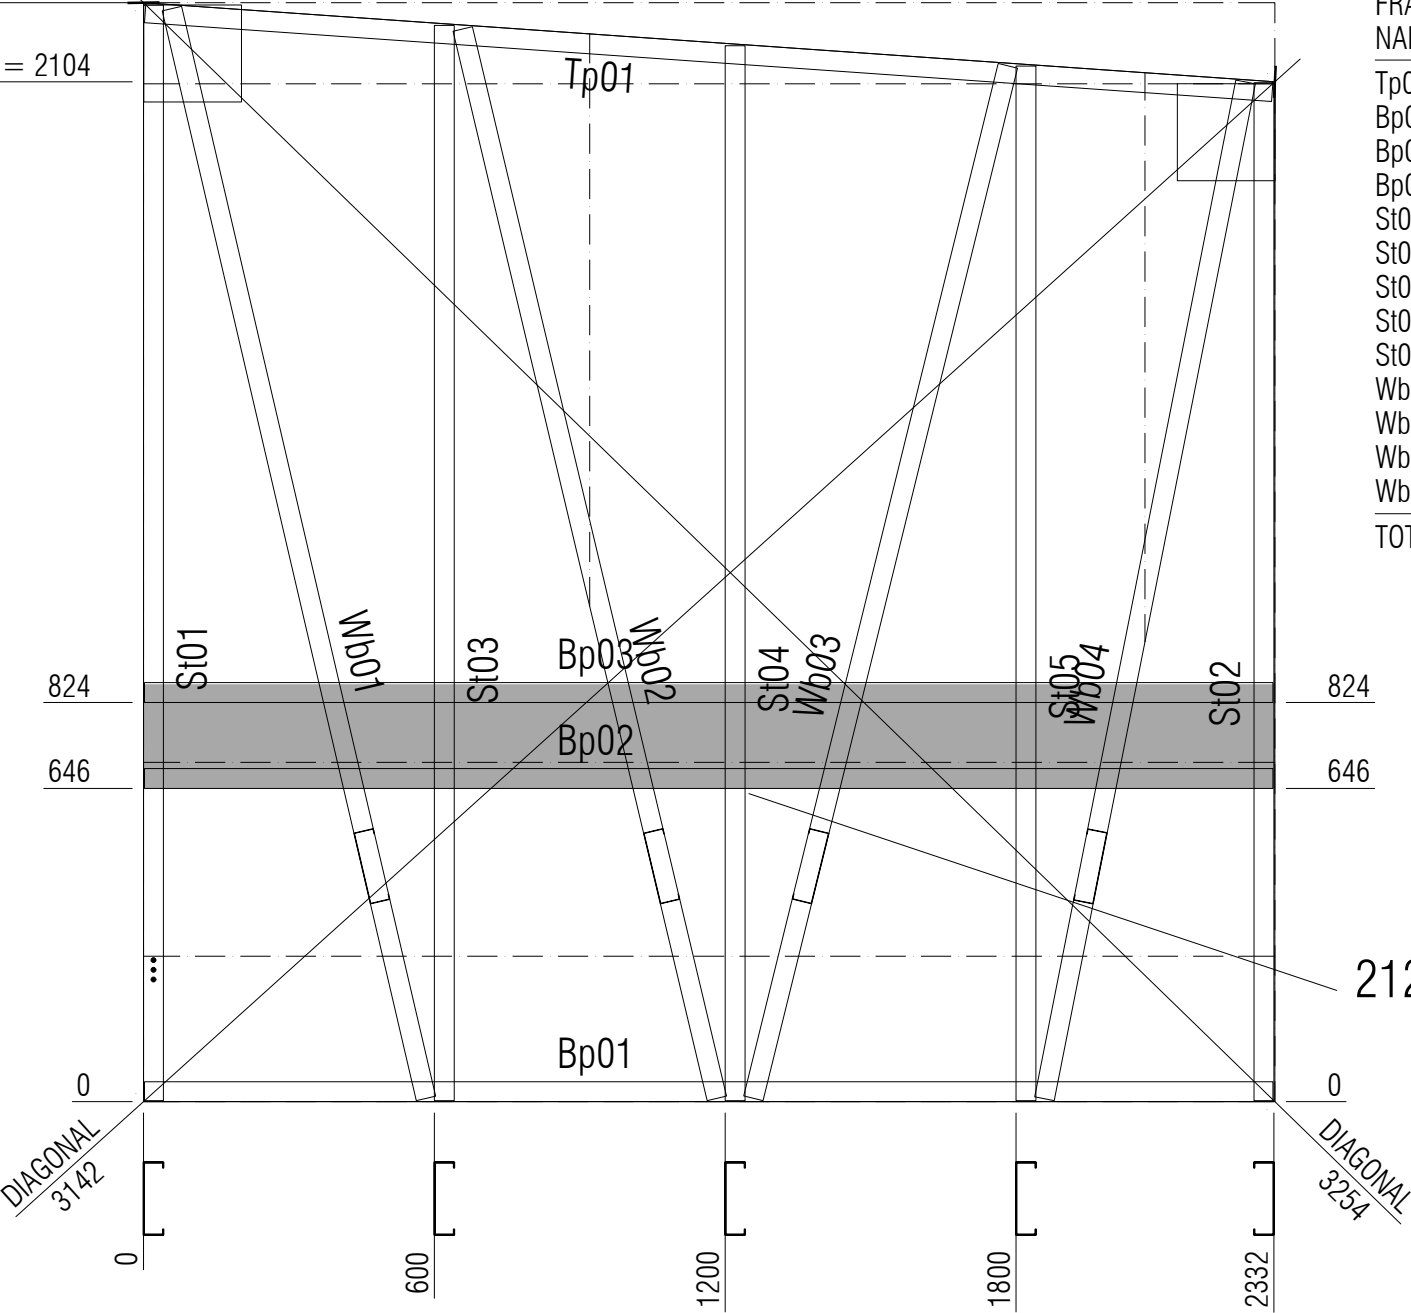

FRAME STICKS NAME	LENGTH	WT	QTY	PROFILE
Tp01	2331	4.3	1	150S41-950-500
Bp01	2328	4.3	1	150S41-950-500
Bp02	2328	4.3	1	150S41-950-500
Bp03	2328	4.3	1	150S41-950-500
St01	2260	4.2	1	150S41-950-500
St02	2100	3.9	1	150S41-950-500
St03	2219	4.1	1	150S41-950-500
St04	2177	4.0	1	150S41-950-500
St05	2135	3.9	1	150S41-950-500
Wb01	2309	4.2	1	150S41-950-500
Wb02	2268	4.2	1	150S41-950-500
Wb03	2194	4.0	1	150S41-950-500
Wb04	2138	3.9	1	150S41-950-500
TOTAL	29114	53.6	13	

212x2.4mm PURLIN COIL WELDED TO FRONT SIDE



DELIVERING SINCE 2003

DRAWN: N.N PH: 02 4860 1416
OFFICE: 02 4860 1400

REV	DATE	REASON

AUSTRUSS PROJECT NAME
CALDERWOOD
AUSTRUSS ZONE NUMBER
A1
CLIENT NAME
ADCO
PROJECT ADDRESS
**179 CALDERWOOD ROAD
CALDERWOOD NSW 2527**

AUSTRUSS PROJECT NUMBER
25363
DRAWING NAME
BE1000
DRAWING NUMBER
####
REV
0




SCAN FOR 3D

Design Summary	
Floor Type	Concrete
Roof Load	Auto
System	FC_AusTruss
Wind Load	N2

WELD STP

WELD ALL

OVERALL HEIGHT = 221

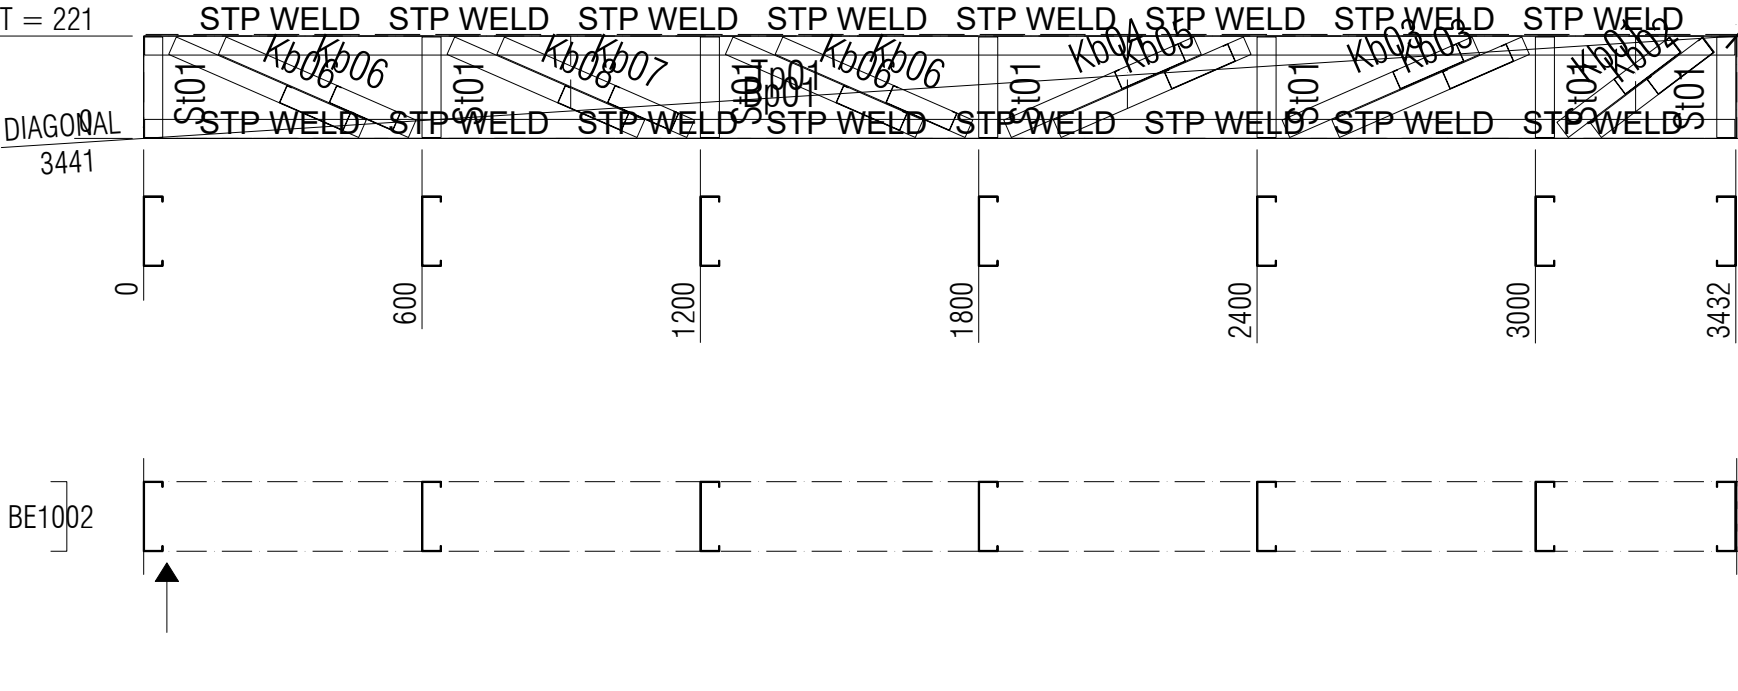

FRAME STICKS NAME	LENGTH	WT	QTY	PROFILE
Tp01	3428	6.3	1	150S41-950-500
Bp01	3428	6.3	1	150S41-950-500
St01	217	0.4	7	150S41-950-500
Kb01	305	0.6	1	150S41-950-500
Kb02	305	0.6	1	150S41-950-500
Kb03	447	0.8	2	150S41-950-500
Kb04	447	0.8	1	150S41-950-500
Kb05	447	0.8	1	150S41-950-500
Kb06	447	0.8	4	150S41-950-500
Kb07	447	0.8	1	150S41-950-500
Kb08	447	0.8	1	150S41-950-500
TOTAL	13452	24.8	21	



DELIVERING SINCE 2003

DRAWN: N.N

PH: 02 4860 1416
OFFICE: 02 4860 1400

REV	DATE	REASON

AUSTRUSS PROJECT NAME

CALDERWOOD

AUSTRUSS ZONE NUMBER

A1

CLIENT NAME

ADCO

PROJECT ADDRESS

179 CALDERWOOD ROAD
CALDERWOOD NSW 2527

AUSTRUSS PROJECT NUMBER

25363

DRAWING NAME

BE1001

DRAWING NUMBER

####

REV

0

SCAN FOR 3D




Design Summary	
Floor Type	Concrete
Roof Load	Auto
System	FC_AusTruss
Wind Load	N2

WELD STP

WELD ALL

OVERALL HEIGHT = 221

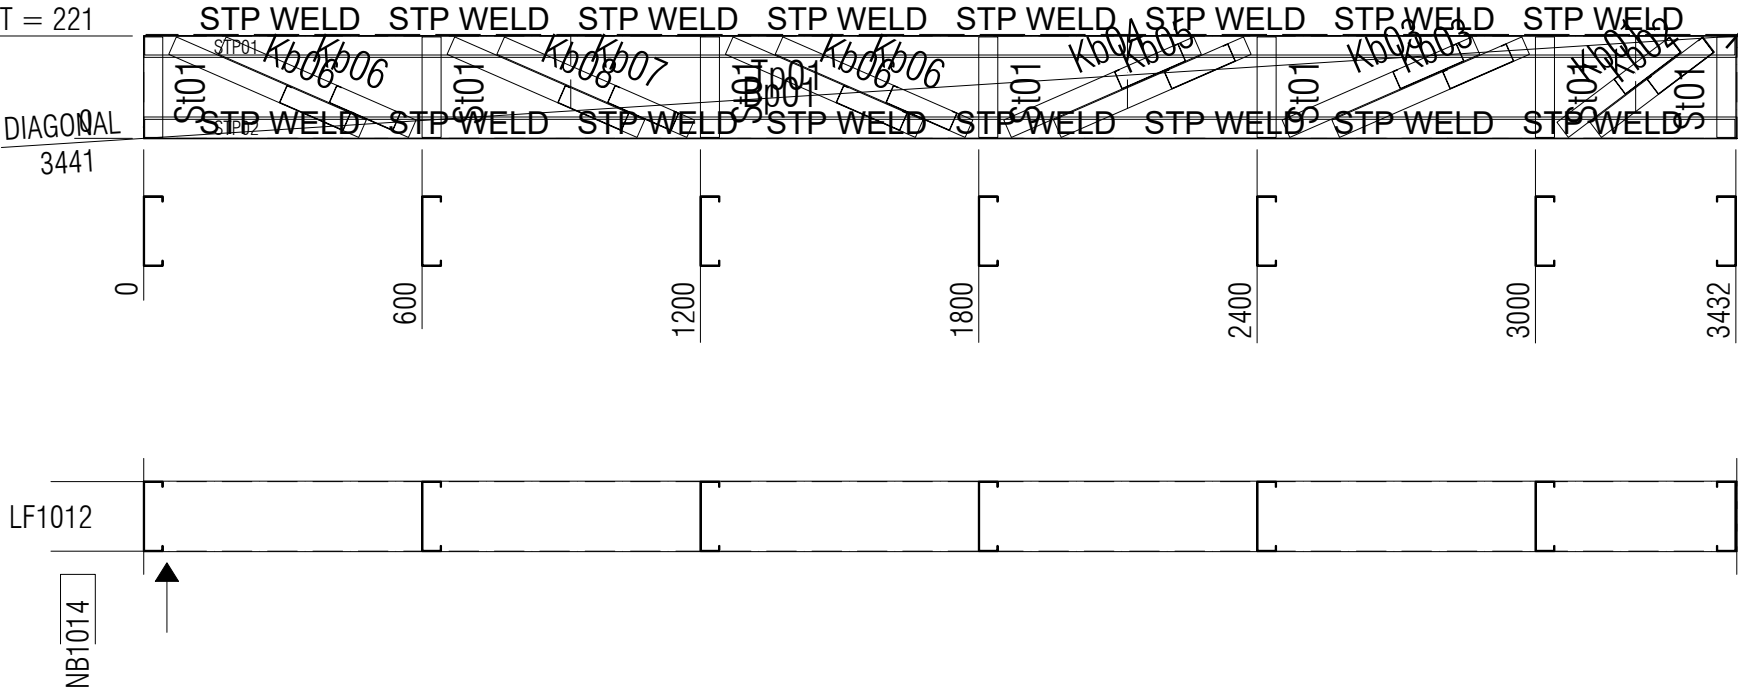

FRAME STICKS				
NAME	LENGTH	WT	QTY	PROFILE
Tp01	3428	6.3	1	150S41-950-500
Bp01	3428	6.3	1	150S41-950-500
St01	217	0.4	7	150S41-950-500
Kb01	305	0.6	1	150S41-950-500
Kb02	305	0.6	1	150S41-950-500
Kb03	447	0.8	2	150S41-950-500
Kb04	447	0.8	1	150S41-950-500
Kb05	447	0.8	1	150S41-950-500
Kb06	447	0.8	4	150S41-950-500
Kb07	447	0.8	1	150S41-950-500
Kb08	447	0.8	1	150S41-950-500
TOTAL	13452	24.8	21	

STEEL SUPPORT MEMBERS				
NAME	PROFILE	LENGTH	WT	QTY
STP01	152U47_095_550	3434	4.4	1
STP02	152U47_095_550	3434	4.4	1
TOTAL				



DELIVERING SINCE 2003

DRAWN: N.N

PH: 02 4860 1416
OFFICE: 02 4860 1400

REV	DATE	REASON

AUSTRUSS PROJECT NAME
CALDERWOOD

AUSTRUSS ZONE NUMBER
A1

CLIENT NAME
ADCO

PROJECT ADDRESS
179 CALDERWOOD ROAD
CALDERWOOD NSW 2527

AUSTRUSS PROJECT NUMBER
25363

DRAWING NAME
BE1002

DRAWING NUMBER
####

REV
0




SCAN FOR 3D

Design Summary	
Floor Type	Concrete
Roof Load	Auto
System	FC_AusTruss
Wind Load	N2

WELD ALL

OVERALL HEIGHT = 1480

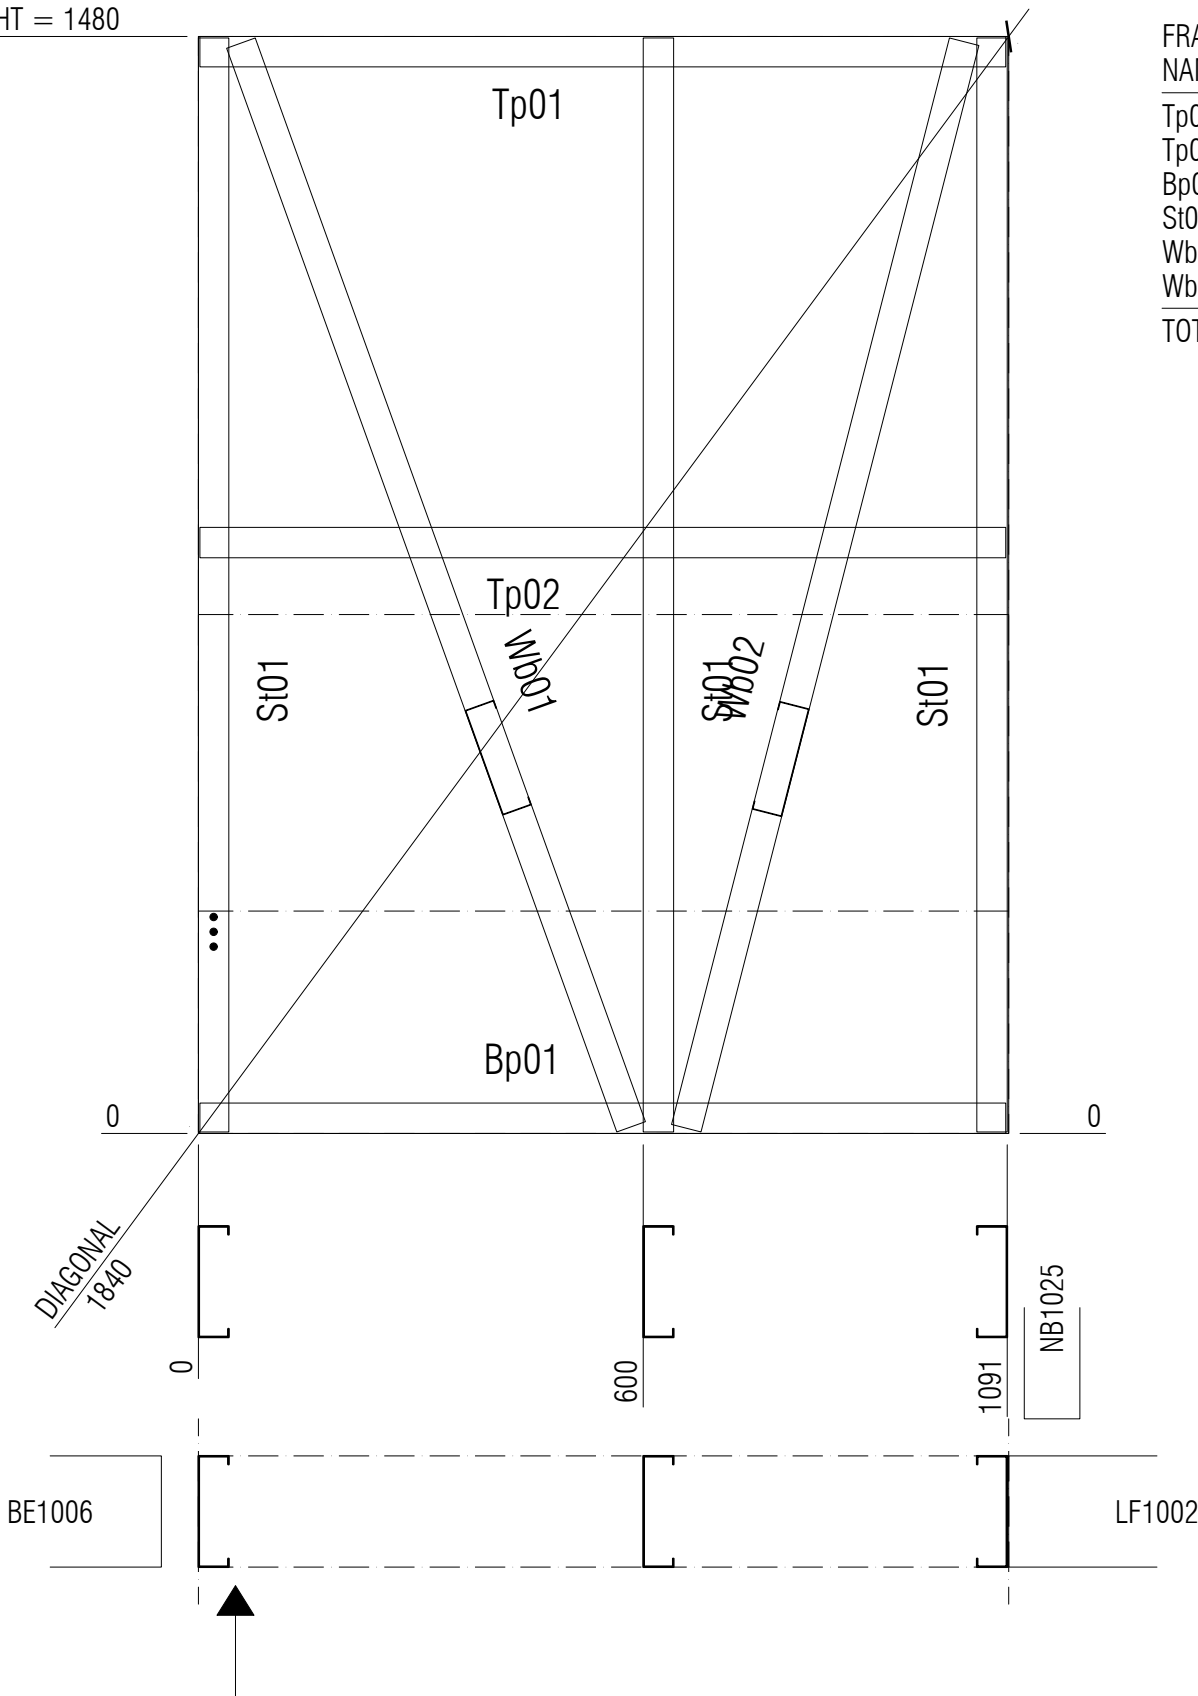

FRAME STICKS				
NAME	LENGTH	WT	QTY	PROFILE
Tp01	1087	2.0	1	150S41-950-500
Tp02	1087	2.0	1	150S41-950-500
Bp01	1087	2.0	1	150S41-950-500
St01	1476	2.7	3	150S41-950-500
Wb01	1554	2.9	1	150S41-950-500
Wb02	1513	2.8	1	150S41-950-500
TOTAL	10755	19.8	8	



DELIVERING SINCE 2003

DRAWN: N.N

PH: 02 4860 1416
OFFICE: 02 4860 1400

REV	DATE	REASON

AUSTRUSS PROJECT NAME

CALDERWOOD

AUSTRUSS ZONE NUMBER

A1

CLIENT NAME

ADCO

PROJECT ADDRESS

179 CALDERWOOD ROAD
CALDERWOOD NSW 2527

AUSTRUSS PROJECT NUMBER

25363

DRAWING NAME

BE1003

DRAWING NUMBER

####

REV

0


SCAN FOR 3D



Design Summary	
Floor Type	Concrete
Roof Load	Auto
System	FC_AusTruss
Wind Load	N2

WELD ALL

OVERALL HEIGHT = 1480

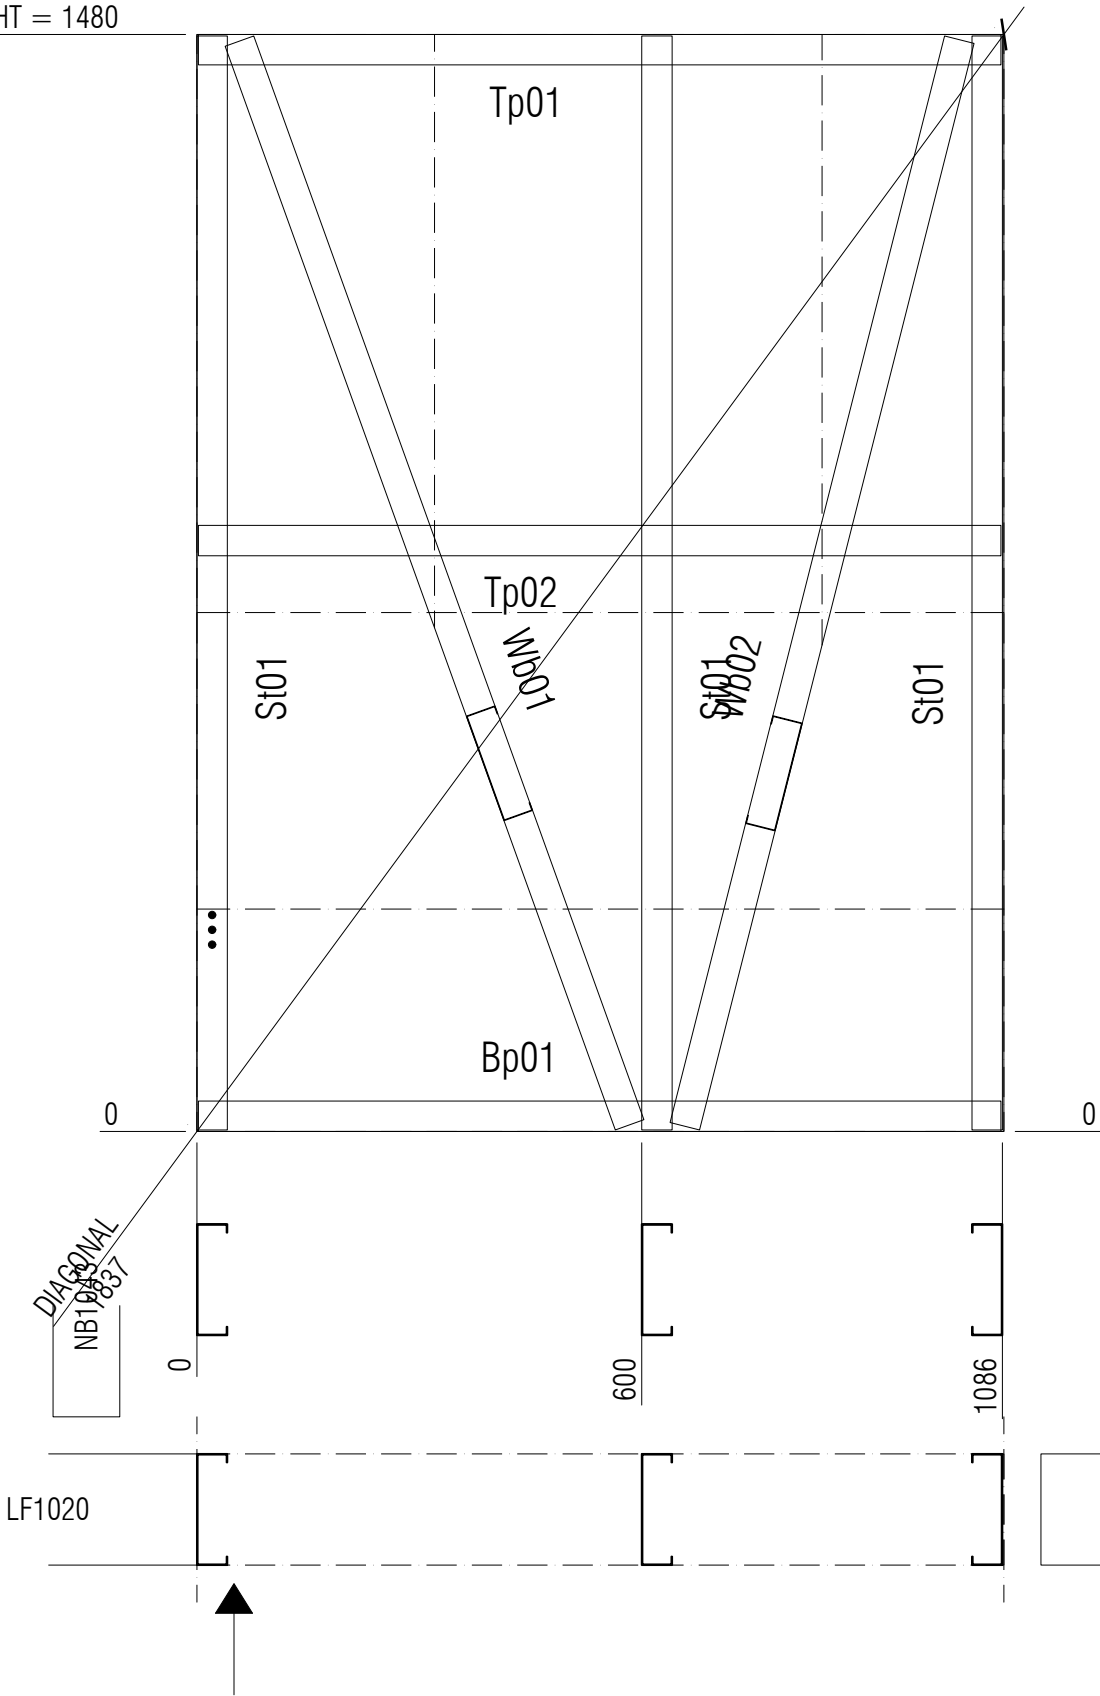

FRAME STICKS				
NAME	LENGTH	WT	QTY	PROFILE
Tp01	1082	2.0	1	150S41-950-500
Tp02	1082	2.0	1	150S41-950-500
Bp01	1082	2.0	1	150S41-950-500
St01	1476	2.7	3	150S41-950-500
Wb01	1554	2.9	1	150S41-950-500
Wb02	1512	2.8	1	150S41-950-500
TOTAL	10741	19.8	8	



DELIVERING SINCE 2003

DRAWN: N.N

PH: 02 4860 1416
OFFICE: 02 4860 1400

REV	DATE	REASON

AUSTRUSS PROJECT NAME

CALDERWOOD

AUSTRUSS ZONE NUMBER

A1

CLIENT NAME

ADCO

PROJECT ADDRESS

179 CALDERWOOD ROAD
CALDERWOOD NSW 2527

AUSTRUSS PROJECT NUMBER

25363

DRAWING NAME

BE1004

DRAWING NUMBER

####

REV

0

SCAN FOR 3D



GUSSET

Technical drawing of a building facade section, showing structural elements and dimensions. The drawing is oriented vertically on the page.

Dimensions:

- Overall height: 1480
- Overall width: 2292
- Horizontal dimensions (from left to right): 0, 600, 1200, 1800, 2292.
- Vertical dimensions (from bottom to top): 0, 600, 1200, 1800, 2292.

Structural Elements and Labels:

- St01:** Vertical structural elements (columns) located at 0, 600, 1200, 1800, and 2292.
- Wb01, Wb02, Wb03, Wb04:** Diagonal structural elements (bracing) connecting the columns.
- TP01, TP02:** Horizontal structural elements (trusses) located at 600 and 1200.
- Bp01:** A horizontal structural element (beam) located at 1800.
- BE1004:** A horizontal structural element (beam) located at the bottom.
- DIAGONAL 2730:** A diagonal structural element spanning the entire width.
- 0:** A vertical structural element located at the bottom left.
- ...**: A vertical structural element located at the bottom right.

Other Labels:

- 0:** Located at the bottom left corner.
- 600, 1200, 1800, 2292:** Located along the bottom edge.
- 0, 600, 1200, 1800, 2292:** Located along the right edge.

FRAME STICKS				
NAME	LENGTH	WT	QTY	PROFILE
Tp01	2288	4.2	1	150S41-950-500
Tp02	2288	4.2	1	150S41-950-500
Bp01	2288	4.2	1	150S41-950-500
St01	1476	2.7	5	150S41-950-500
Wb01	1554	2.9	1	150S41-950-500
Wb02	1554	2.9	1	150S41-950-500
Wb03	1554	2.9	1	150S41-950-500
Wb04	1513	2.8	1	150S41-950-500
TOTAL	20418	37.6	12	

 AUSTRUSS DELIVERING SINCE 2003		PH: 02 4860 1416 OFFICE: 02 4860 1400	
		DRAWN: N.N	
<u>REV</u>	<u>DATE</u>	<u>REASON</u>	
AUSTRUSS PROJECT NAME CALDERWOOD			
AUSTRUSS ZONE NUMBER A1			
CLIENT NAME ADCO			
PROJECT ADDRESS 179 CALDERWOOD ROAD CALDERWOOD NSW 2527			
AUSTRUSS PROJECT NUMBER 25363			
DRAWING NAME BE1005			
DRAWING NUMBER ####			REV 0




SCAN FOR 3D

Design Summary	
Floor Type	Concrete
Roof Load	Auto
System	FC_AusTruss
Wind Load	N2

WELD ALL

GUSSET

OVERALL HEIGHT = 1480

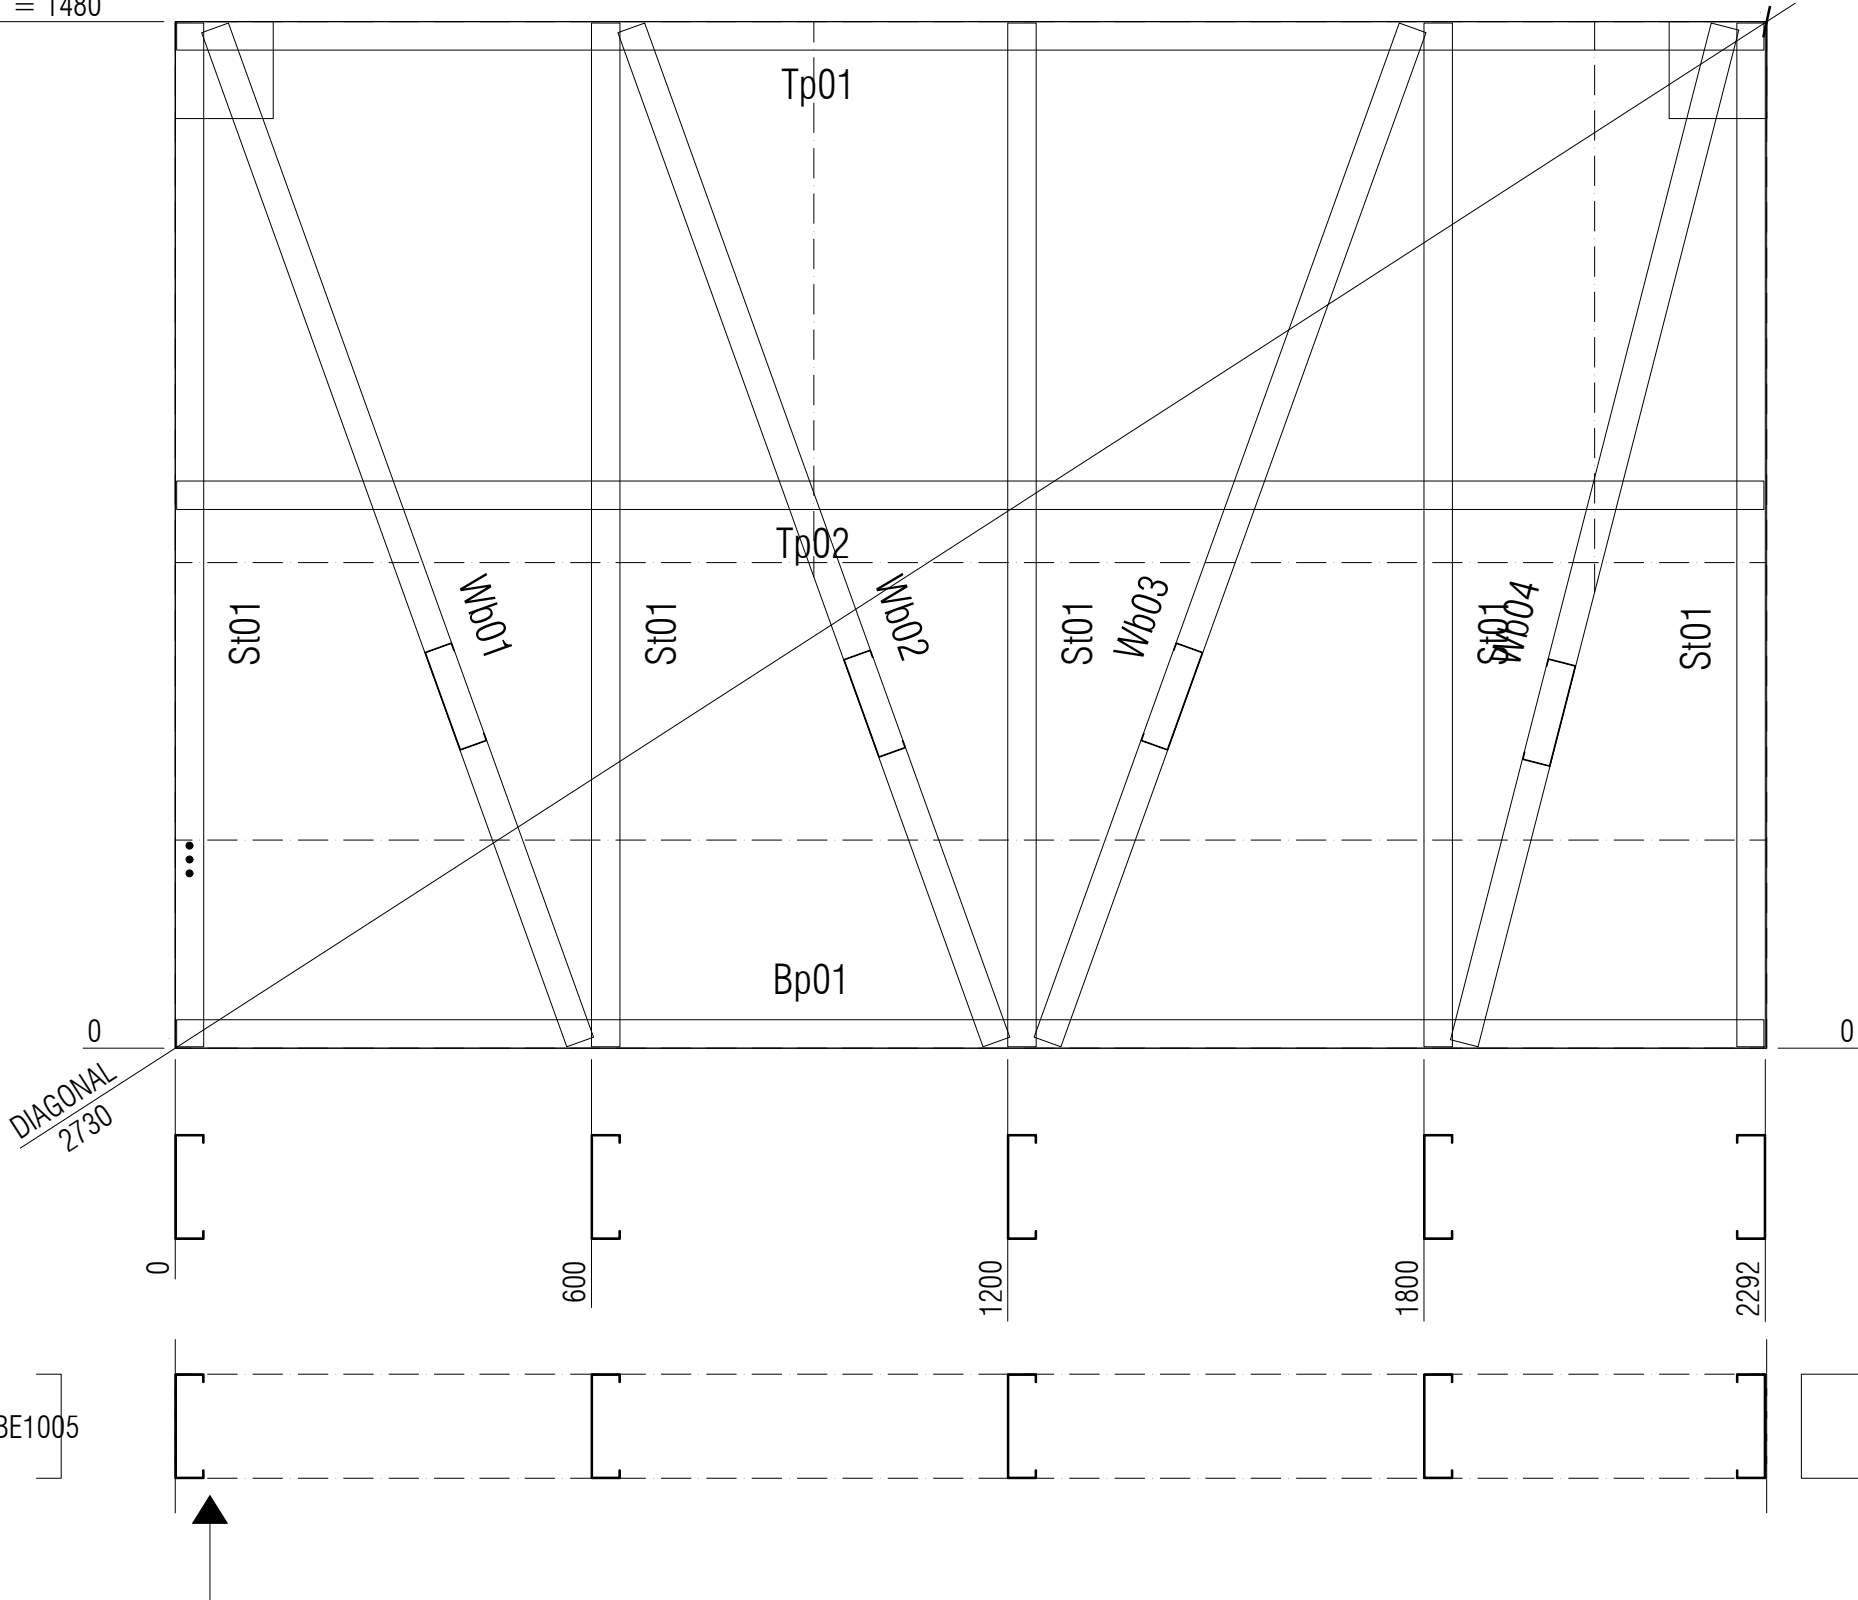

FRAME STICKS				
NAME	LENGTH	WT	QTY	PROFILE
Tp01	2288	4.2	1	150S41-950-500
Tp02	2288	4.2	1	150S41-950-500
Bp01	2288	4.2	1	150S41-950-500
St01	1476	2.7	5	150S41-950-500
Wb01	1554	2.9	1	150S41-950-500
Wb02	1554	2.9	1	150S41-950-500
Wb03	1554	2.9	1	150S41-950-500
Wb04	1513	2.8	1	150S41-950-500
TOTAL	20418	37.6	12	



DELIVERING SINCE 2003

DRAWN: N.N

PH: 02 4860 1416
OFFICE: 02 4860 1400

REV	DATE	REASON

AUSTRUSS PROJECT NAME

CALDERWOOD

AUSTRUSS ZONE NUMBER

A1

CLIENT NAME

ADCO

PROJECT ADDRESS

179 CALDERWOOD ROAD
CALDERWOOD NSW 2527

AUSTRUSS PROJECT NUMBER

25363

DRAWING NAME

BE1006

DRAWING NUMBER

####

REV

0




SCAN FOR 3D

Design Summary	
Floor Type	Concrete
Roof Load	Auto
System	FC_AusTruss
Wind Load	N2

WELD ALL

GUSSET

OVERALL HEIGHT = 2300

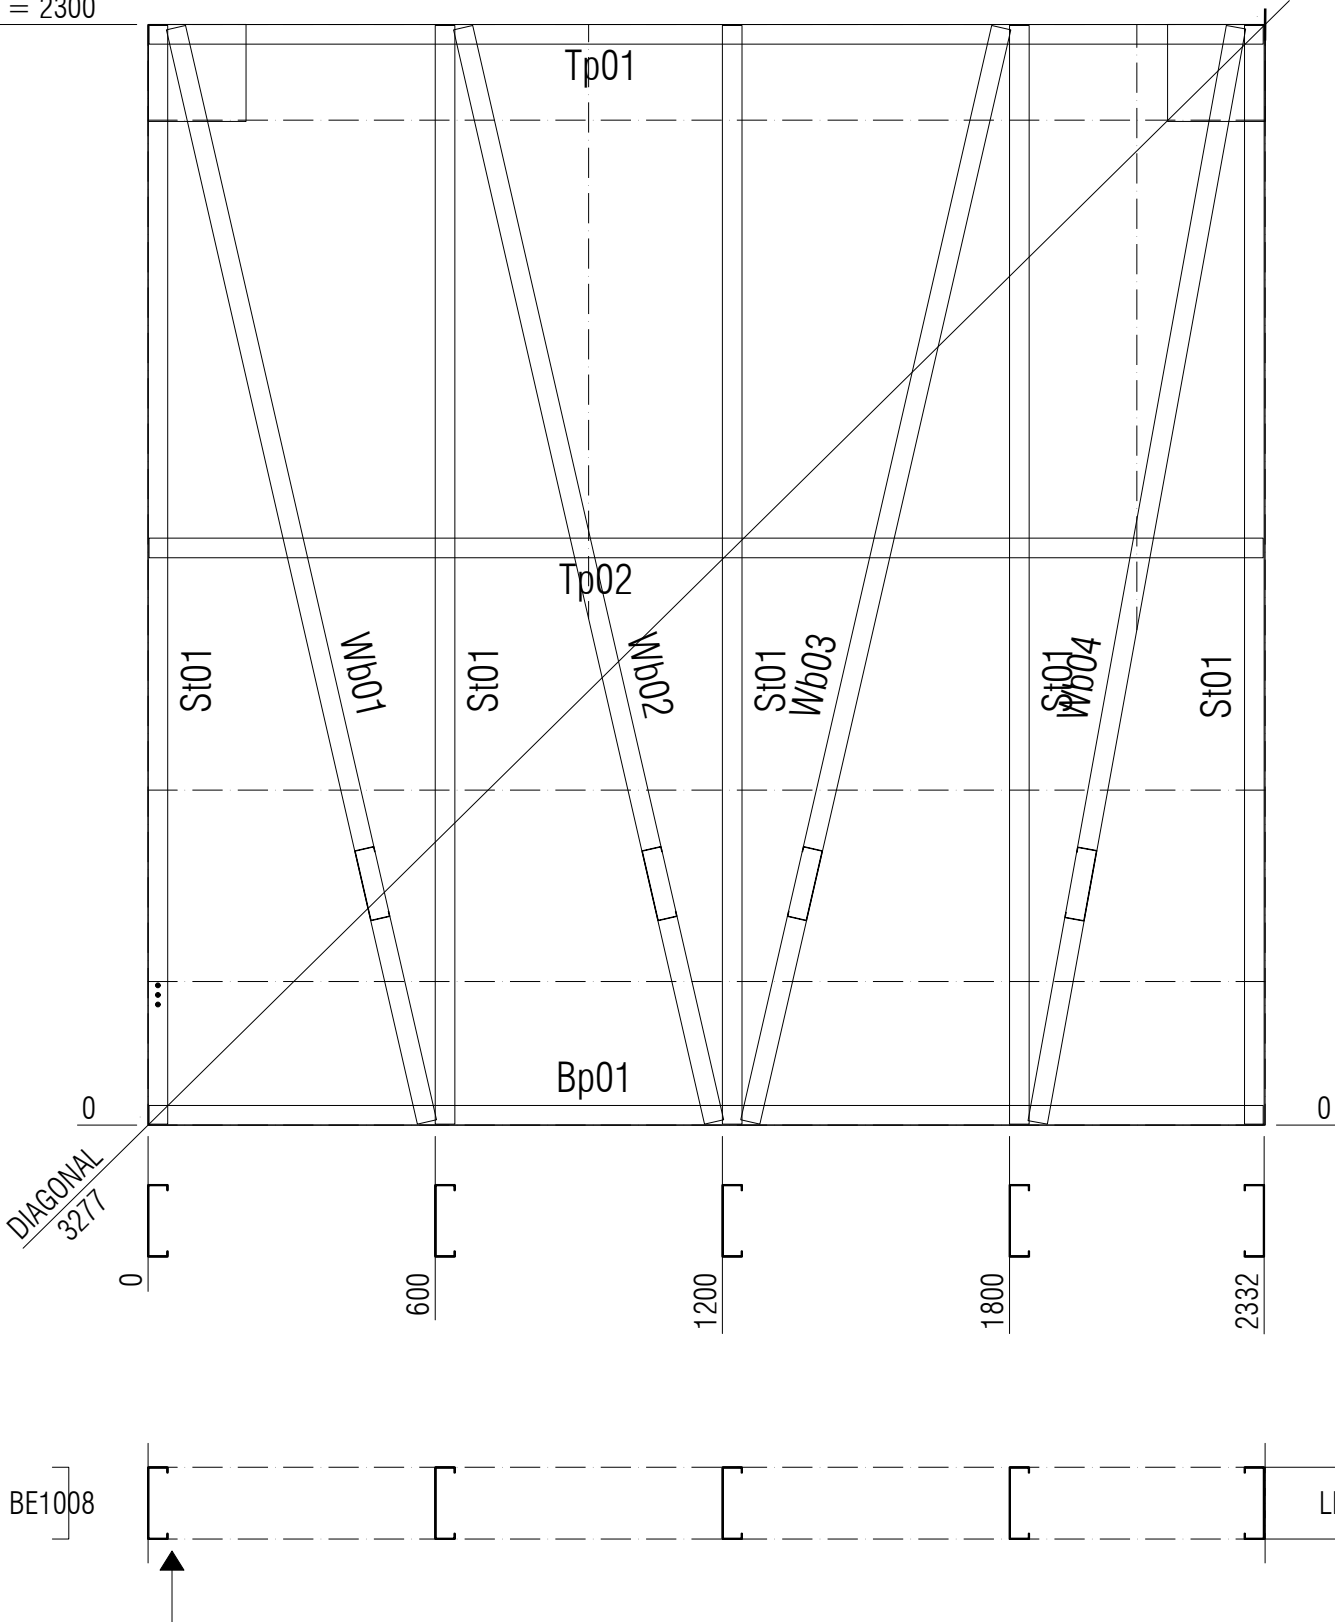

FRAME STICKS NAME	LENGTH	WT	QTY	PROFILE
Tp01	2328	4.3	1	150S41-950-500
Tp02	2328	4.3	1	150S41-950-500
Bp01	2328	4.3	1	150S41-950-500
St01	2296	4.2	5	150S41-950-500
Wb01	2346	4.3	1	150S41-950-500
Wb02	2346	4.3	1	150S41-950-500
Wb03	2346	4.3	1	150S41-950-500
Wb04	2326	4.3	1	150S41-950-500
TOTAL	27827	51.2	12	



DELIVERING SINCE 2003

DRAWN: N.N PH: 02 4860 1416
OFFICE: 02 4860 1400

REV	DATE	REASON

AUSTRUSS PROJECT NAME
CALDERWOOD
AUSTRUSS ZONE NUMBER
A1

CLIENT NAME
ADCO

PROJECT ADDRESS
**179 CALDERWOOD ROAD
CALDERWOOD NSW 2527**

AUSTRUSS PROJECT NUMBER
25363

DRAWING NAME
BE1007

DRAWING NUMBER
####

REV
0




SCAN FOR 3D

Design Summary	
Floor Type	Concrete
Roof Load	Auto
System	FC_AusTruss
Wind Load	N2

WELD ALL

GUSSET

OVERALL HEIGHT = 2300

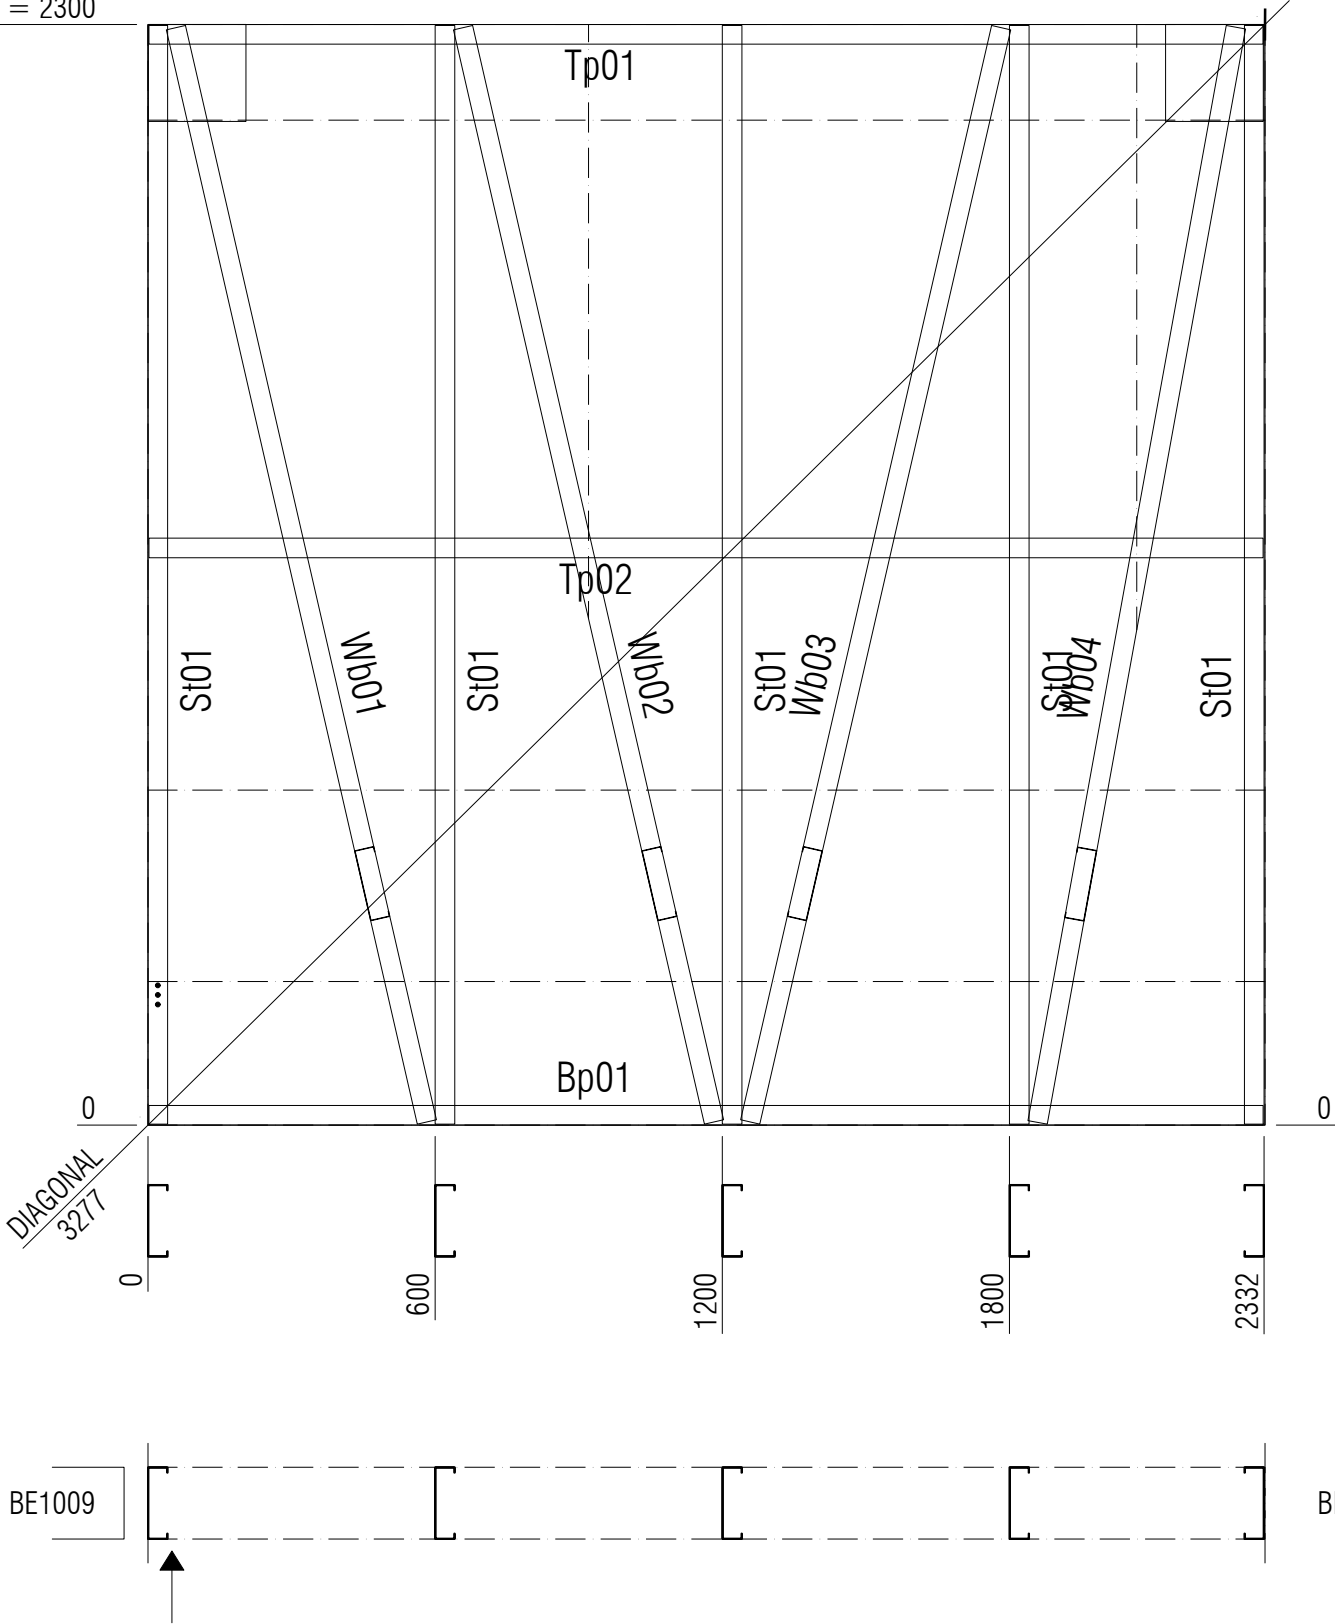

FRAME STICKS NAME	LENGTH	WT	QTY	PROFILE
Tp01	2328	4.3	1	150S41-950-500
Tp02	2328	4.3	1	150S41-950-500
Bp01	2328	4.3	1	150S41-950-500
St01	2296	4.2	5	150S41-950-500
Wb01	2346	4.3	1	150S41-950-500
Wb02	2346	4.3	1	150S41-950-500
Wb03	2346	4.3	1	150S41-950-500
Wb04	2326	4.3	1	150S41-950-500
TOTAL	27827	51.2	12	



DELIVERING SINCE 2003

DRAWN: N.N PH: 02 4860 1416
OFFICE: 02 4860 1400

REV	DATE	REASON

AUSTRUSS PROJECT NAME
CALDERWOOD
AUSTRUSS ZONE NUMBER
A1
CLIENT NAME
ADCO

PROJECT ADDRESS
**179 CALDERWOOD ROAD
CALDERWOOD NSW 2527**

AUSTRUSS PROJECT NUMBER
25363

DRAWING NAME
BE1008

DRAWING NUMBER
####

REV
0




SCAN FOR 3D

Design Summary	
Floor Type	Concrete
Roof Load	Auto
System	FC_AusTruss
Wind Load	N2

WELD ALL

GUSSET

OVERALL HEIGHT = 2300

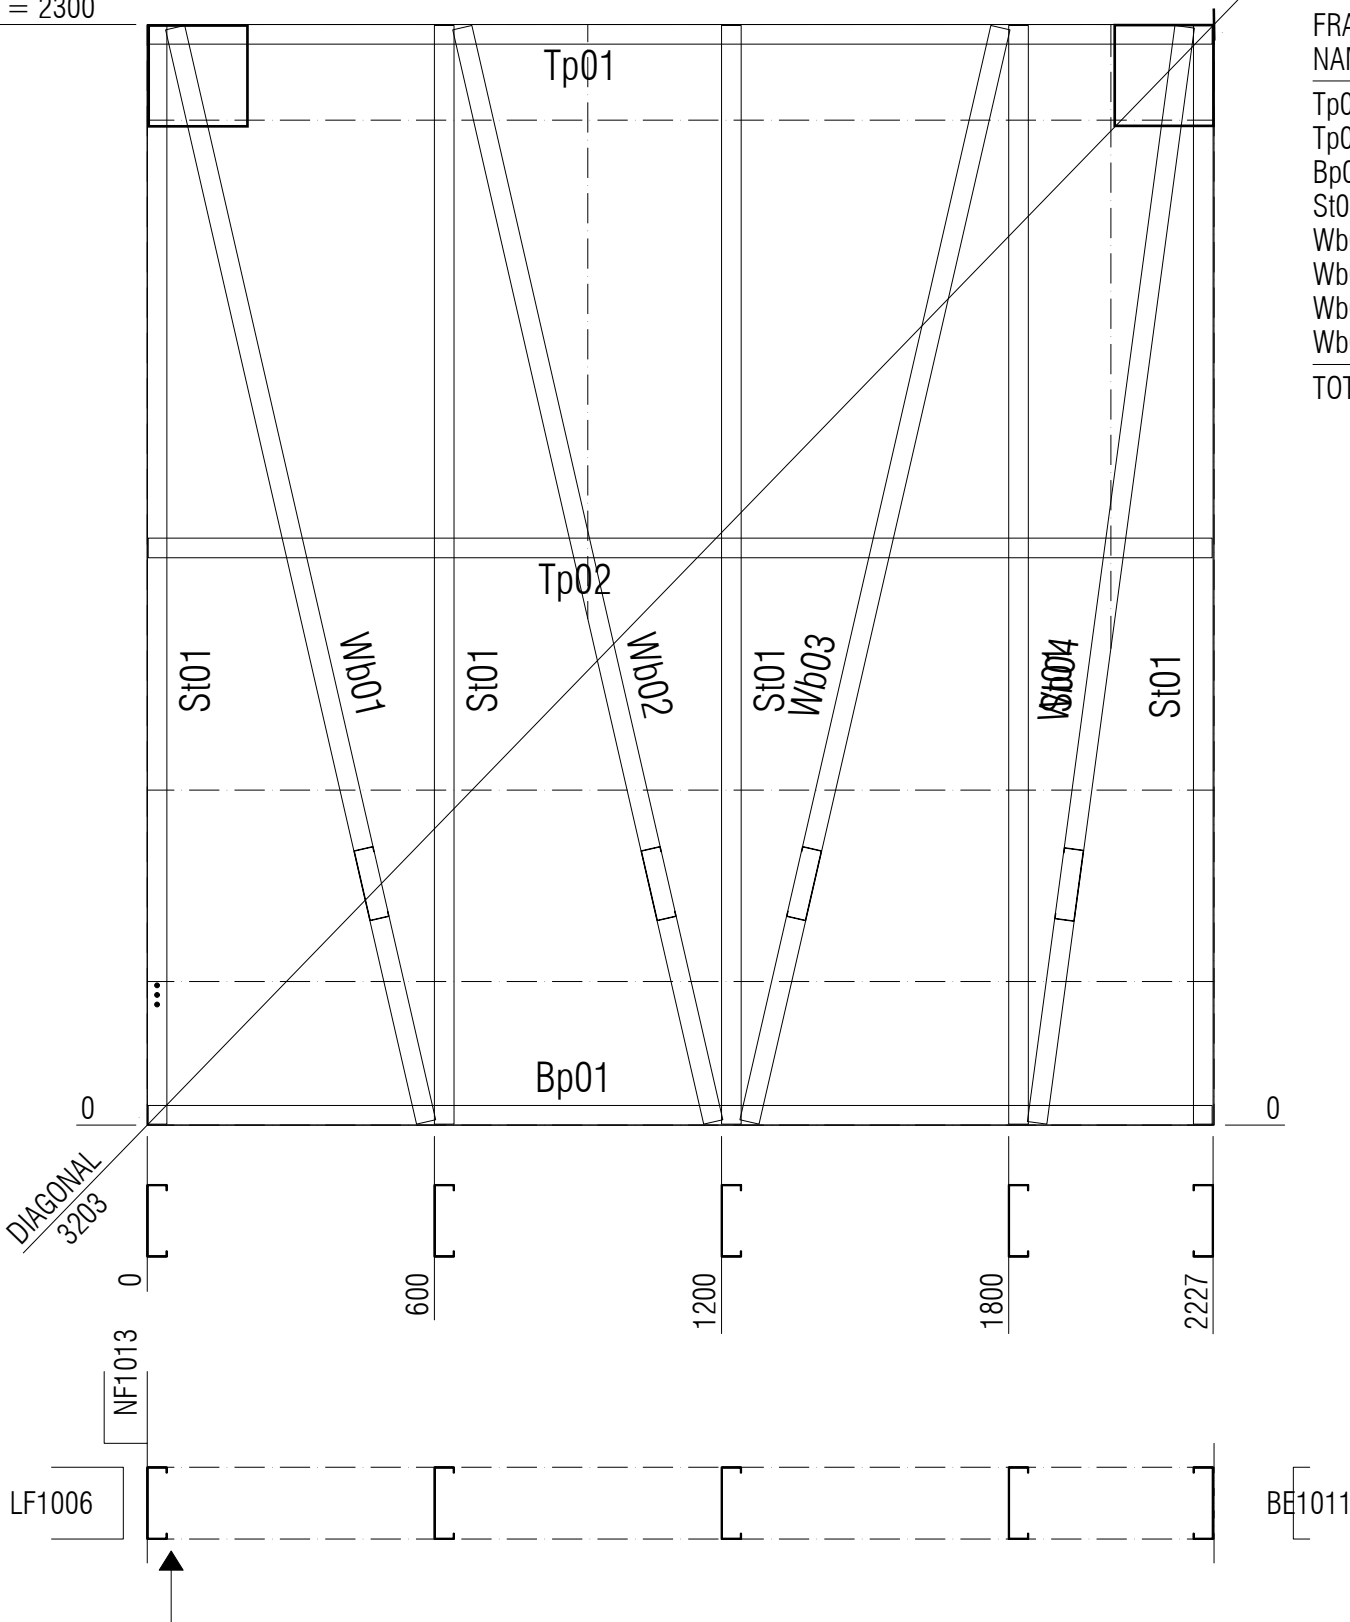

FRAME STICKS				
NAME	LENGTH	WT	QTY	PROFILE
Tp01	2223	4.1	1	150S41-950-500
Tp02	2223	4.1	1	150S41-950-500
Bp01	2223	4.1	1	150S41-950-500
St01	2296	4.2	5	150S41-950-500
Wb01	2346	4.3	1	150S41-950-500
Wb02	2346	4.3	1	150S41-950-500
Wb03	2346	4.3	1	150S41-950-500
Wb04	2311	4.3	1	150S41-950-500
TOTAL	27497	50.6	12	



DELIVERING SINCE 2003

DRAWN: N.N

PH: 02 4860 1416
OFFICE: 02 4860 1400

REV	DATE	REASON

AUSTRUSS PROJECT NAME

CALDERWOOD

AUSTRUSS ZONE NUMBER

A1

CLIENT NAME

ADCO

PROJECT ADDRESS

179 CALDERWOOD ROAD
CALDERWOOD NSW 2527

AUSTRUSS PROJECT NUMBER

25363

DRAWING NAME

BE1010

DRAWING NUMBER

####

REV

0




SCAN FOR 3D

Design Summary	
Floor Type	Concrete
Roof Load	Auto
System	FC_AusTruss
Wind Load	N2

WELD ALL

GUSSET

OVERALL HEIGHT = 2300

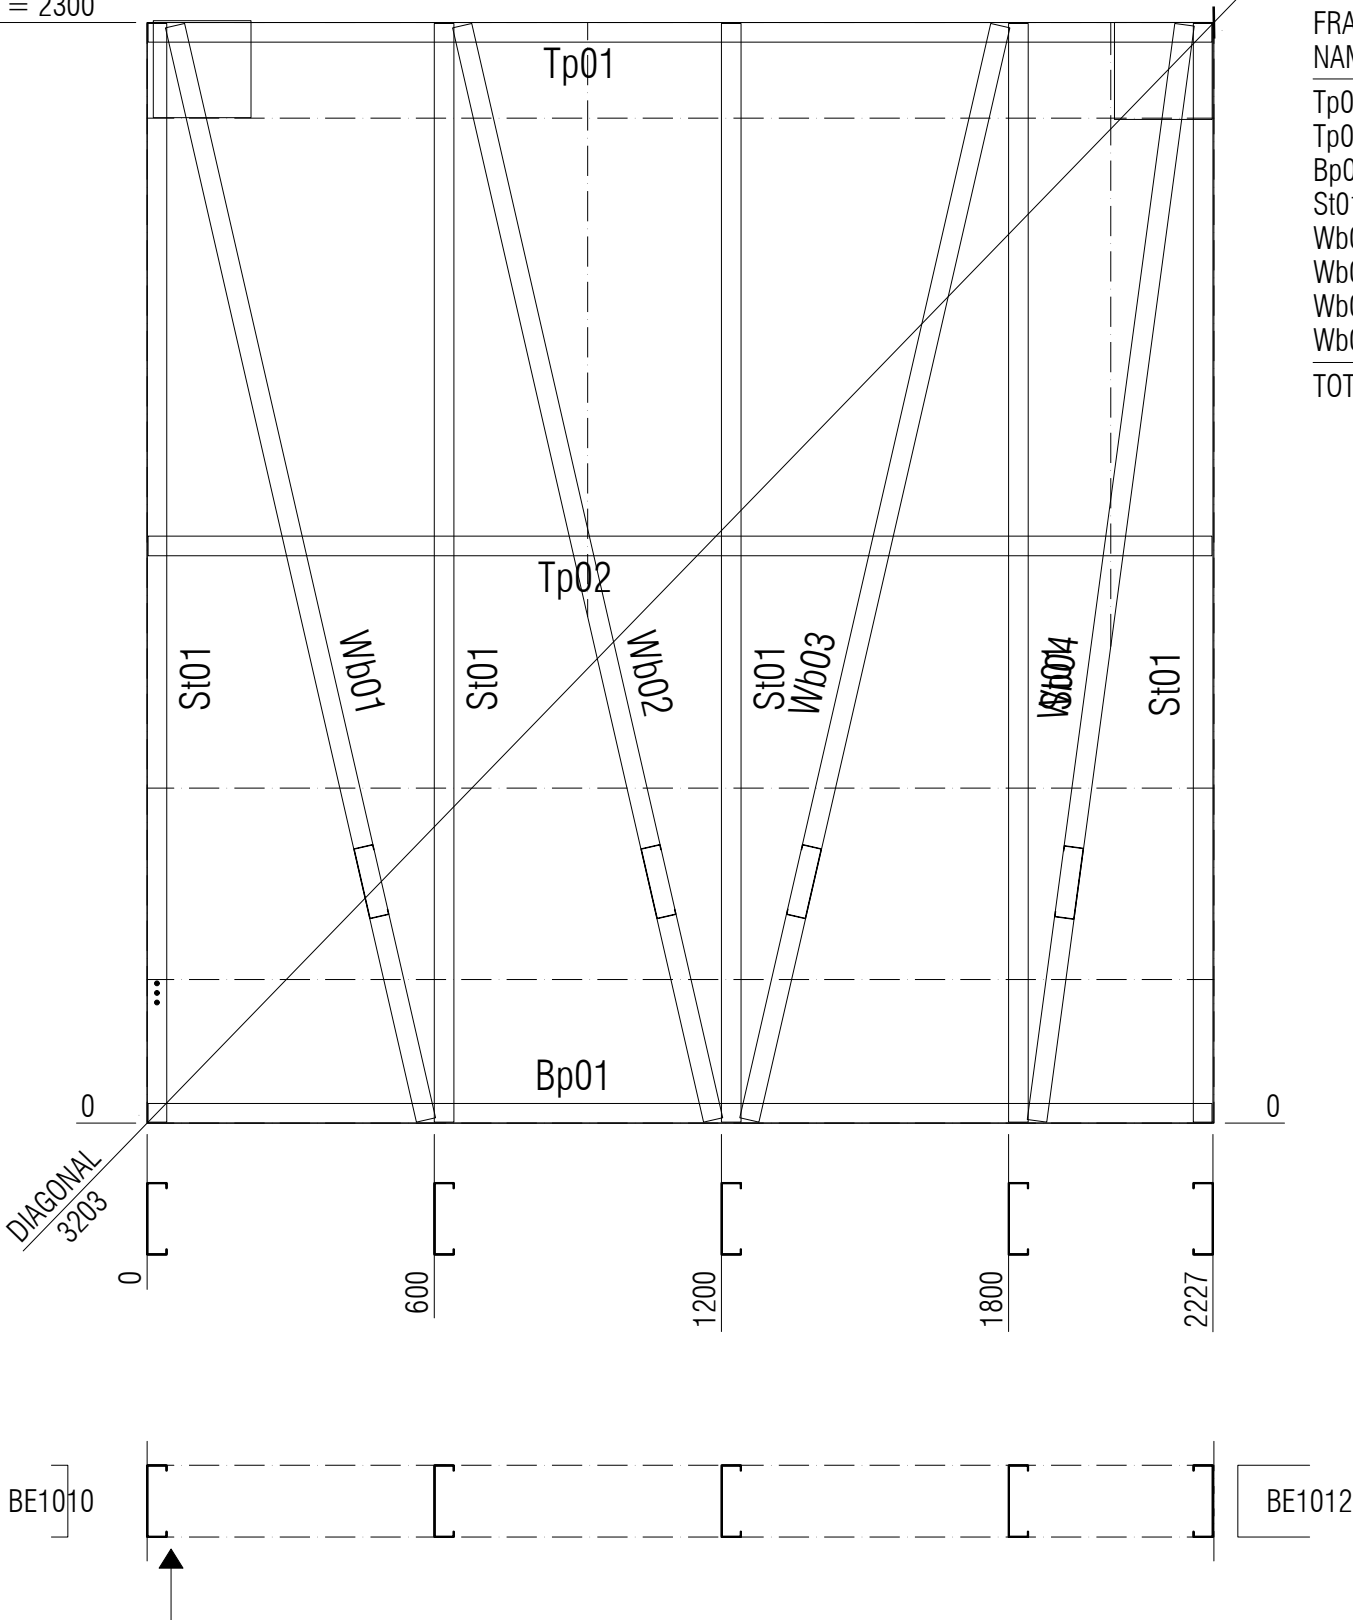

FRAME STICKS				
NAME	LENGTH	WT	QTY	PROFILE
Tp01	2223	4.1	1	150S41-950-500
Tp02	2223	4.1	1	150S41-950-500
Bp01	2223	4.1	1	150S41-950-500
St01	2296	4.2	5	150S41-950-500
Wb01	2346	4.3	1	150S41-950-500
Wb02	2346	4.3	1	150S41-950-500
Wb03	2346	4.3	1	150S41-950-500
Wb04	2311	4.3	1	150S41-950-500
TOTAL	27497	50.6	12	



DELIVERING SINCE 2003

DRAWN: N.N PH: 02 4860 1416
OFFICE: 02 4860 1400

REV	DATE	REASON

AUSTRUSS PROJECT NAME

CALDERWOOD

AUSTRUSS ZONE NUMBER

A1

CLIENT NAME

ADCO

PROJECT ADDRESS

179 CALDERWOOD ROAD
CALDERWOOD NSW 2527

AUSTRUSS PROJECT NUMBER

25363

DRAWING NAME

BE1011

DRAWING NUMBER

####

REV

0




SCAN FOR 3D

Design Summary	
Floor Type	Concrete
Roof Load	Auto
System	FC_AusTruss
Wind Load	N2

WELD ALL

OVERALL HEIGHT = 2300

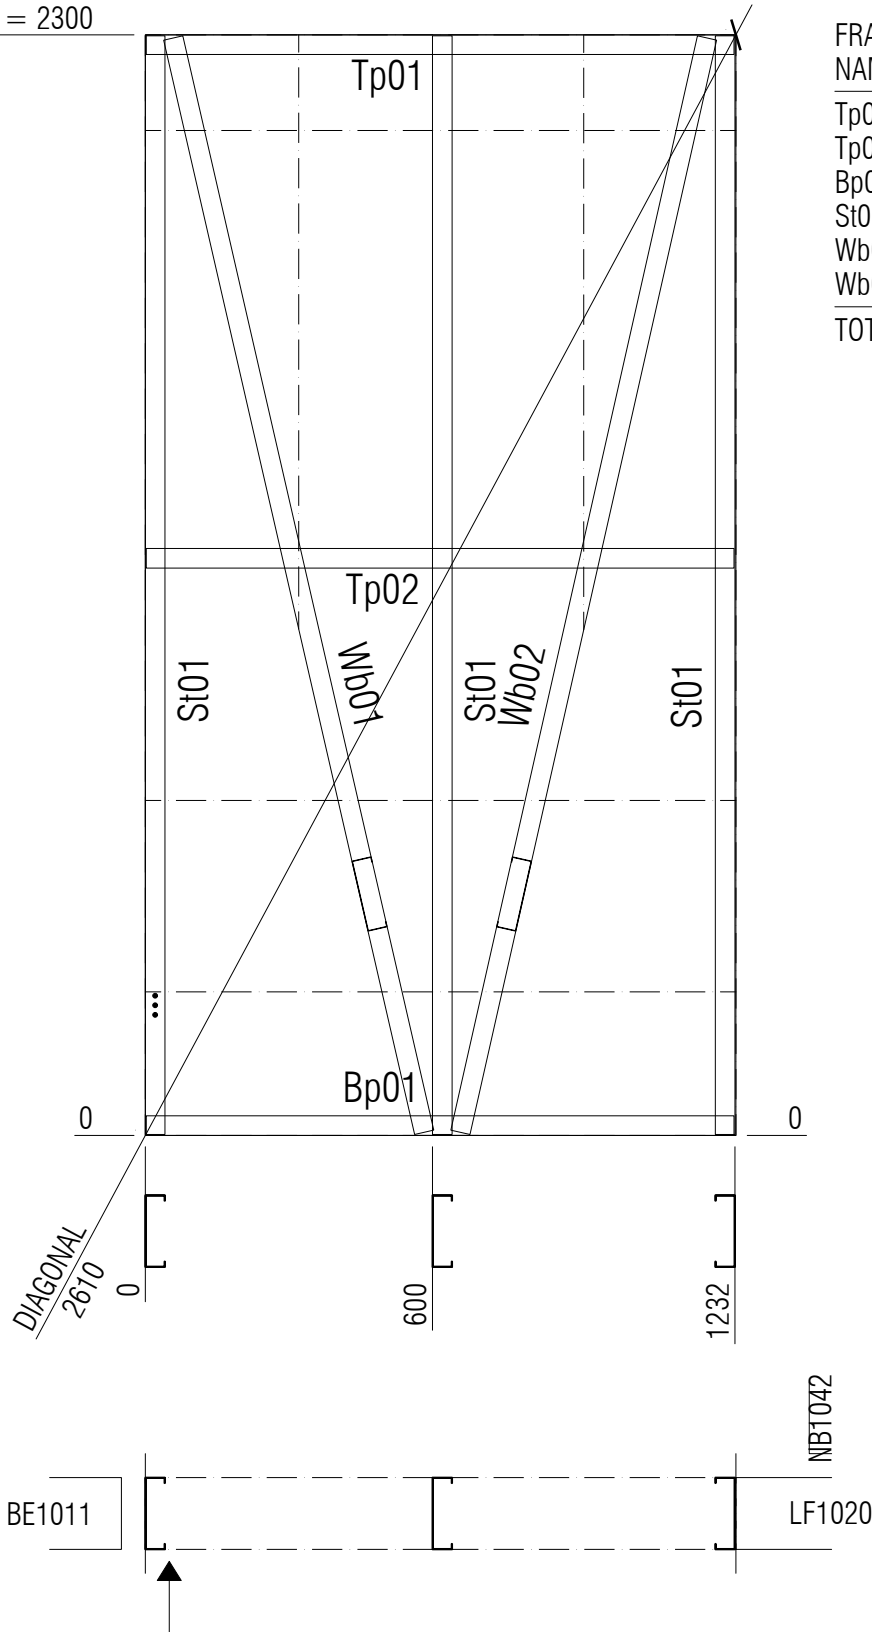


Design Summary	
Floor Type	Concrete
Roof Load	Auto
System	FC_AusTruss
Wind Load	N2

WELD ALL


GUSSET

212x2.4mm PURLIN COIL WELDED TO FRONT SIDE

OVERALL HEIGHT = 1031

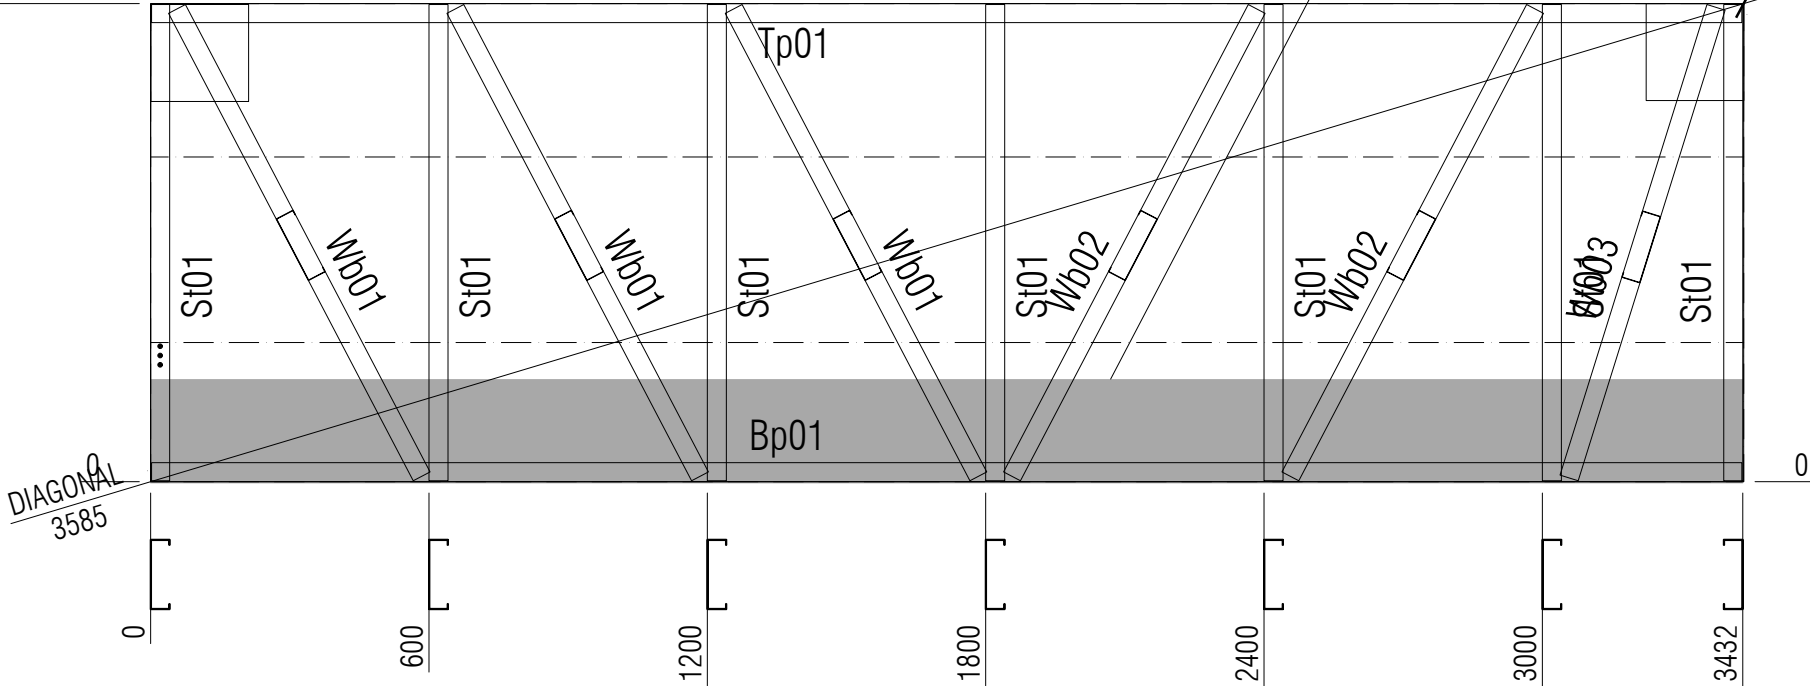

FRAME STICKS NAME	LENGTH	WT	QTY	PROFILE
Tp01	3428	6.3	1	150S41-950-500
Bp01	3428	6.3	1	150S41-950-500
St01	1027	1.9	7	150S41-950-500
Wb01	1137	2.1	3	150S41-950-500
Wb02	1137	2.1	2	150S41-950-500
Wb03	1063	2.0	1	150S41-950-500
TOTAL	20792	38.3	15	

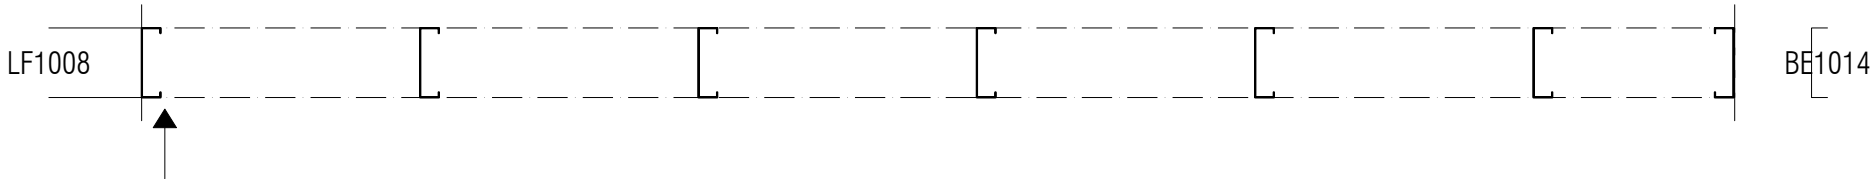

SCAN FOR 3D

 AUSTRUSS		
DELIVERING SINCE 2003		
DRAWN: N.N		PH: 02 4860 1416 OFFICE: 02 4860 1400
REV	DATE	REASON
AUSTRUSS PROJECT NAME		
CALDERWOOD		
AUSTRUSS ZONE NUMBER		
A1		
CLIENT NAME		
ADCO		
PROJECT ADDRESS		
179 CALDERWOOD ROAD CALDERWOOD NSW 2527		
AUSTRUSS PROJECT NUMBER		
25363		
DRAWING NAME		
BE1013		
DRAWING NUMBER		REV
####		0


Design Summary	
Floor Type	Concrete
Roof Load	Auto
System	FC_AusTruss
Wind Load	N2

WELD ALL


GUSSET

212x2.4mm PURLIN COIL WELDED TO FRONT SIDE

OVERALL HEIGHT = 1031

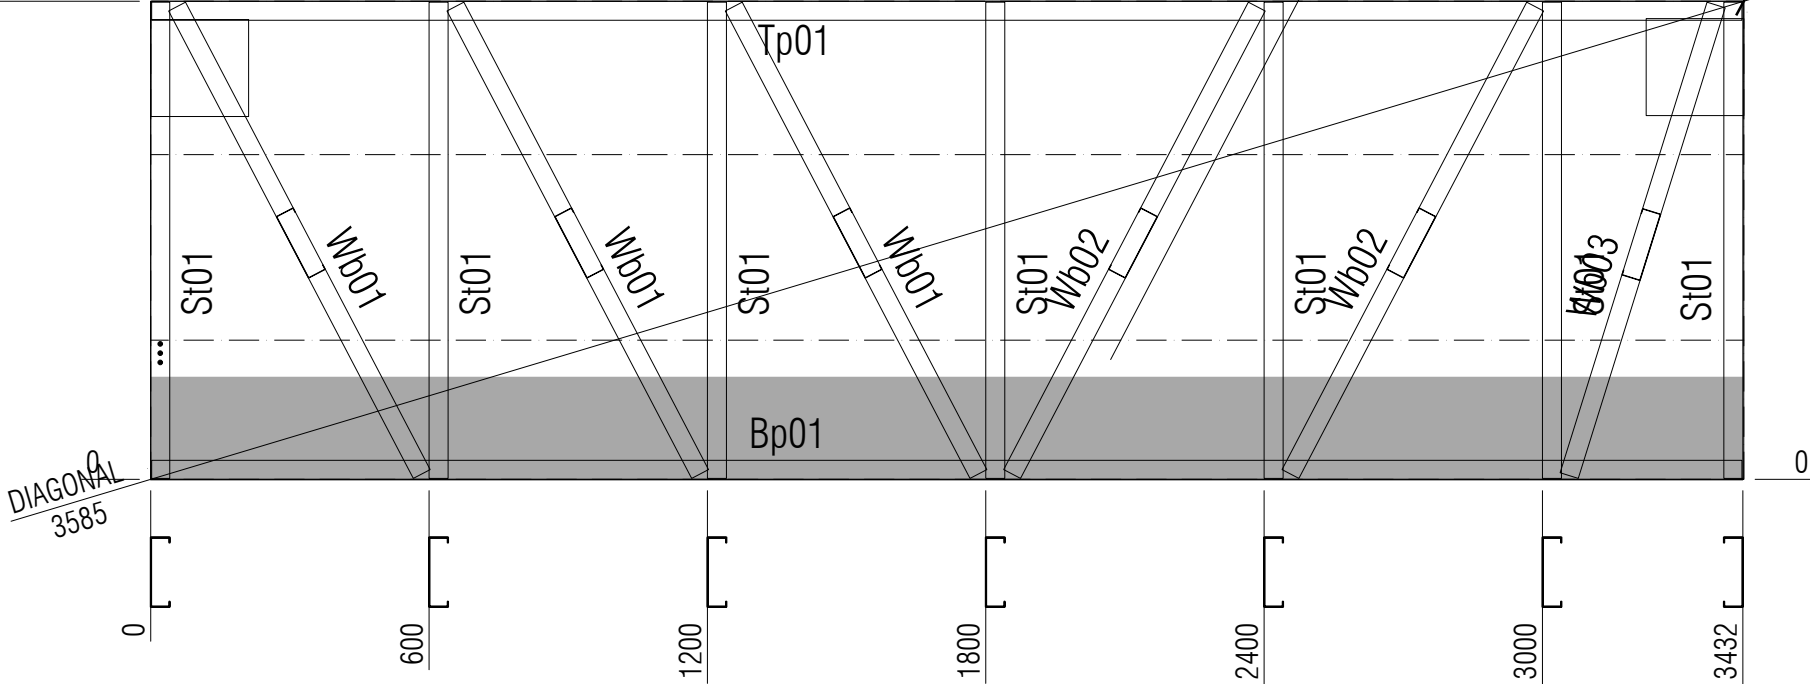

FRAME STICKS				
NAME	LENGTH	WT	QTY	PROFILE
Tp01	3428	6.3	1	150S41-950-500
Bp01	3428	6.3	1	150S41-950-500
St01	1027	1.9	7	150S41-950-500
Wb01	1137	2.1	3	150S41-950-500
Wb02	1137	2.1	2	150S41-950-500
Wb03	1063	2.0	1	150S41-950-500
TOTAL	20792	38.3	15	

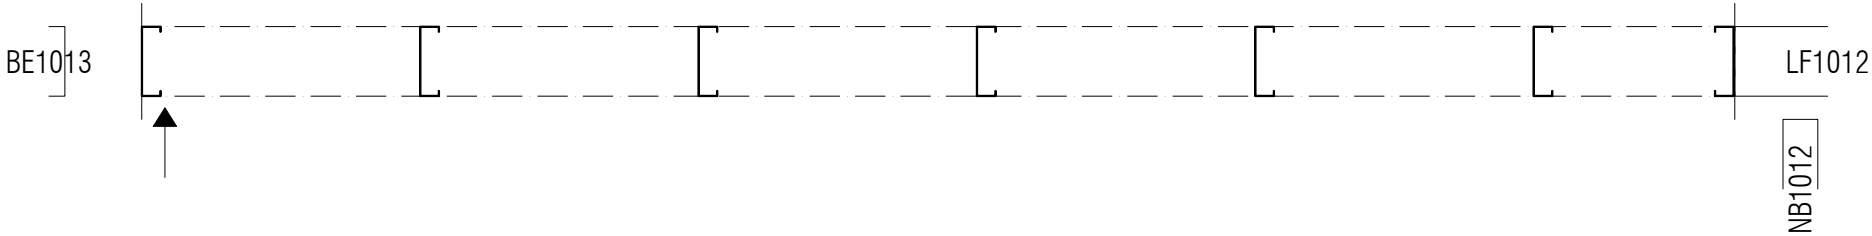

SCAN FOR 3D

AUSTRUSS	
DELIVERING SINCE 2003	
DRAWN: N.N	PH: 02 4860 1416 OFFICE: 02 4860 1400
REV	DATE REASON
AUSTRUSS PROJECT NAME	
CALDERWOOD	
AUSTRUSS ZONE NUMBER	
A1	
CLIENT NAME	
ADCO	
PROJECT ADDRESS	
179 CALDERWOOD ROAD CALDERWOOD NSW 2527	
AUSTRUSS PROJECT NUMBER	
25363	
DRAWING NAME	
BE1014	
DRAWING NUMBER	
####	
REV	
0	


Design Summary	
Floor Type	Concrete
Roof Load	Auto
System	FC_AusTruss
Wind Load	N2

WELD ALL


GUSSET

212x2.4mm PURLIN COIL WELDED TO FRONT SIDE

OVERALL HEIGHT = 1031

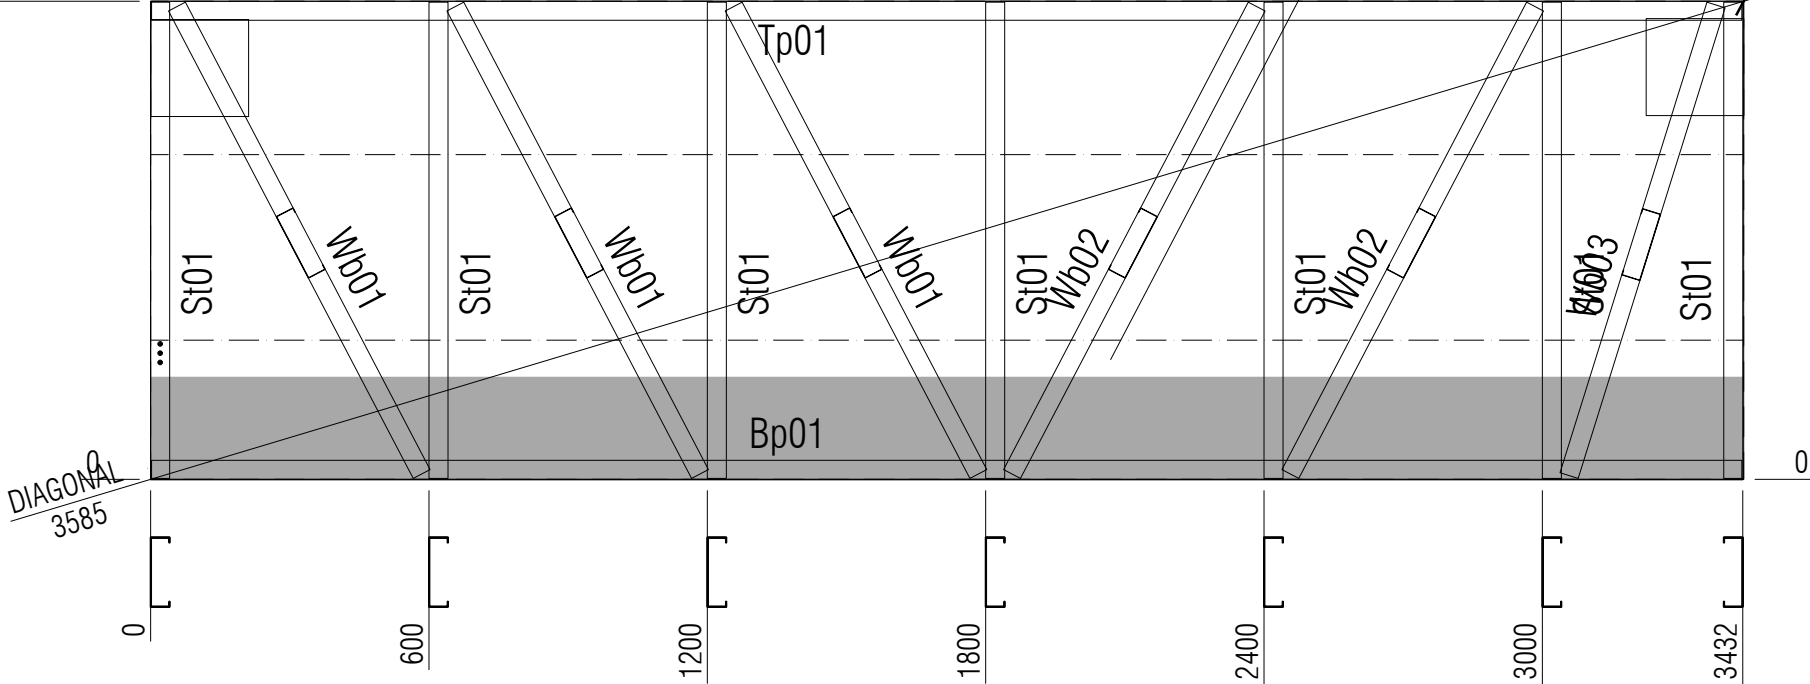

FRAME STICKS				
NAME	LENGTH	WT	QTY	PROFILE
Tp01	3428	6.3	1	150S41-950-500
Bp01	3428	6.3	1	150S41-950-500
St01	1027	1.9	7	150S41-950-500
Wb01	1137	2.1	3	150S41-950-500
Wb02	1137	2.1	2	150S41-950-500
Wb03	1063	2.0	1	150S41-950-500
TOTAL	20792	38.3	15	

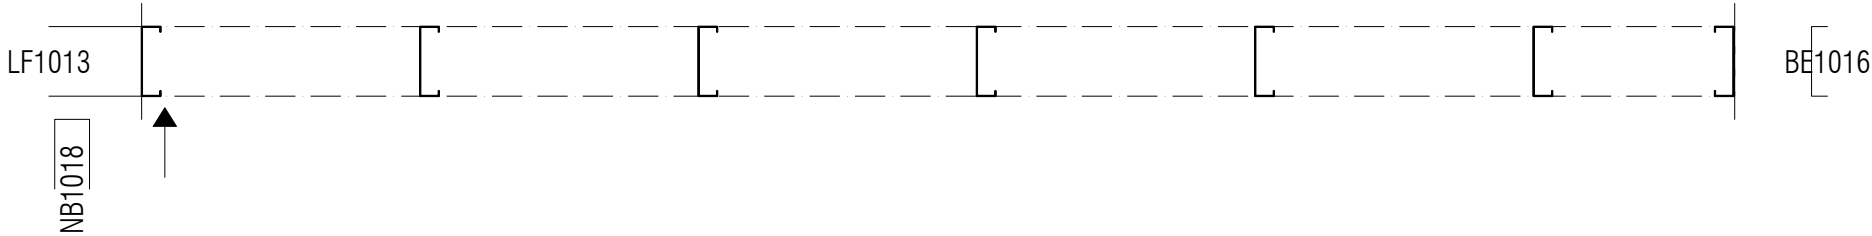



DELIVERING SINCE 2003

DRAWN: N.N

PH: 02 4860 1416
OFFICE: 02 4860 1400

REV	DATE	REASON

AUSTRUSS PROJECT NAME

CALDERWOOD

AUSTRUSS ZONE NUMBER

A1

CLIENT NAME

ADCO

PROJECT ADDRESS

179 CALDERWOOD ROAD
CALDERWOOD NSW 2527

AUSTRUSS PROJECT NUMBER

25363

DRAWING NAME

BE1015

DRAWING NUMBER

####


REV

0



SCAN FOR 3D

WELD ALL GUSSET

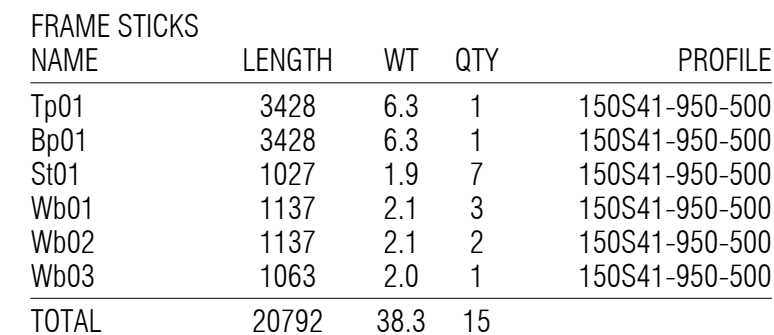

 AUSTRUSS DELIVERING SINCE 2003		
DRAWN: N.N		PH: 02 4860 1416 OFFICE: 02 4860 1400
REV	DATE	REASON
AUSTRUSS PROJECT NAME CALDERWOOD AUSTRUSS ZONE NUMBER A1		
CLIENT NAME ADCO		
PROJECT ADDRESS 179 CALDERWOOD ROAD CALDERWOOD NSW 2527		
AUSTRUSS PROJECT NUMBER 25363		
DRAWING NAME BE1016		
DRAWING NUMBER		REV
####		0


Design Summary	
Floor Type	Concrete
Roof Load	Auto
System	FC_AusTruss
Wind Load	N2

WELD PART

OVERALL HEIGHT = 5052
HEIGHT = 5009

FRAME STICKS				
NAME	LENGTH	WT	QTY	PROFILE
Tp01	601	1.1	1	150S41-950-500
Bp01	602	1.1	1	150S41-950-500
St01	5045	9.3	1	150S41-950-500
St02	5005	9.2	1	150S41-950-500
St03	5008	9.2	1	150S41-950-500
Ng01	602	1.1	4	150S41-950-500
Kb01	1001	1.8	1	150S41-950-500
Kb02	1117	2.1	1	150S41-950-500
Kb03	1006	1.9	1	150S41-950-500
Kb04	953	1.8	1	150S41-950-500
Kb05	1361	2.5	1	150S41-950-500
TOTAL	24108	44.4	14	


212x2.4mm PURLIN COIL WELDED TO FRONT SIDE

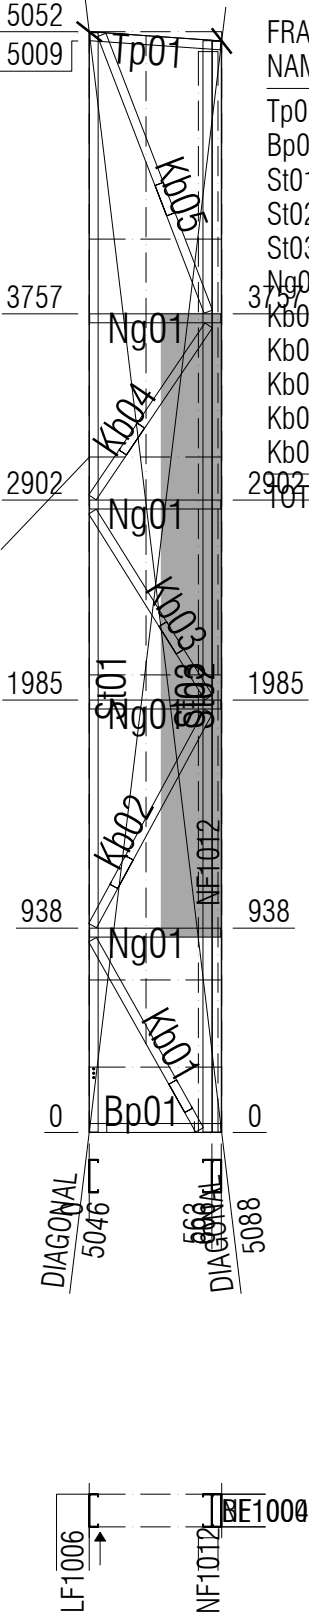


AUSTRUSS DELIVERING SINCE 2003	
DRAWN: N.N	PH: 02 4860 1416 OFFICE: 02 4860 1400
REV	DATE REASON
AUSTRUSS PROJECT NAME CALDERWOOD	
AUSTRUSS ZONE NUMBER A1	
CLIENT NAME ADCO	
PROJECT ADDRESS 179 CALDERWOOD ROAD CALDERWOOD NSW 2527	
AUSTRUSS PROJECT NUMBER 25363	
DRAWING NAME LF1007	
DRAWING NUMBER ####	
REV 0	

Design Summary	
Floor Type	Concrete
Roof Load	Auto
System	FC_AusTruss
Wind Load	N2

WELD PART

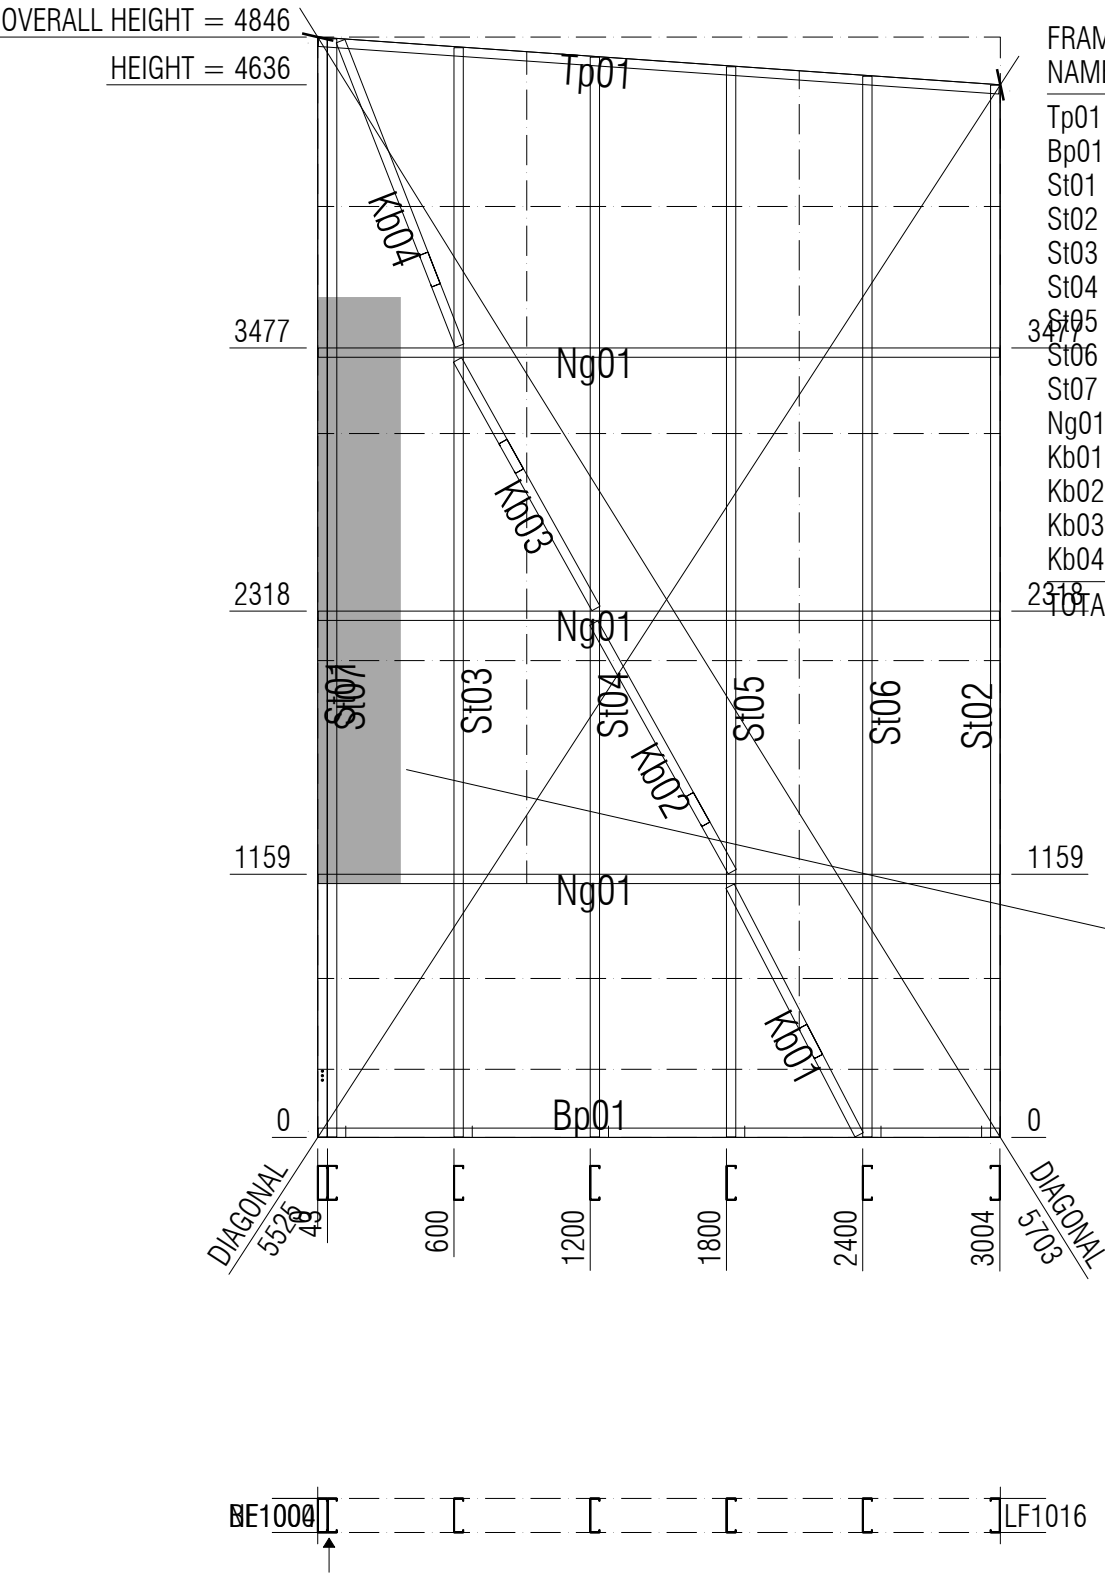

FRAME STICKS NAME	LENGTH	WT	QTY	PROFILE
Tp01	3005	5.5	1	150S41-950-500
Bp01	3000	5.5	1	150S41-950-500
St01	4839	8.9	1	150S41-950-500
St02	4632	8.5	1	150S41-950-500
St03	4797	8.8	1	150S41-950-500
St04	4755	8.7	1	150S41-950-500
St05	4713	8.7	1	150S41-950-500
St06	4671	8.6	1	150S41-950-500
St07	4836	8.9	1	150S41-950-500
Ng01	3000	5.5	3	150S41-950-500
Kb01	1234	2.3	1	150S41-950-500
Kb02	1253	2.3	1	150S41-950-500
Kb03	1253	2.3	1	150S41-950-500
Kb04	1440	2.6	1	150S41-950-500
TOTAL	53430	98.3	16	

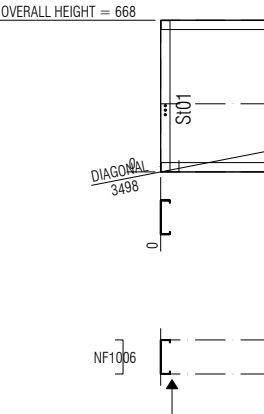


SCAN FOR 3D

 AUSTRUSS DELIVERING SINCE 2003		
DRAWN: N.N		PH: 02 4860 1416 OFFICE: 02 4860 1400
REV	DATE	REASON
AUSTRUSS PROJECT NAME		
CALDERWOOD		
AUSTRUSS ZONE NUMBER		
A1		
CLIENT NAME		
ADCO		
PROJECT ADDRESS		
OVERALL HEIGHT = 888		
179 CALDERWOOD ROAD CALDERWOOD NSW 2527		
AUSTRUSS PROJECT NUMBER		
25363		
DRAWING NAME		
LF1015		
DRAWING NUMBER		
####		
REV		
0		

Design Summary	
Floor Type	Concrete
Roof Load	Auto
System	FC_AusTruss
Wind Load	N2

WELD PART

OVERALL HEIGHT = 668

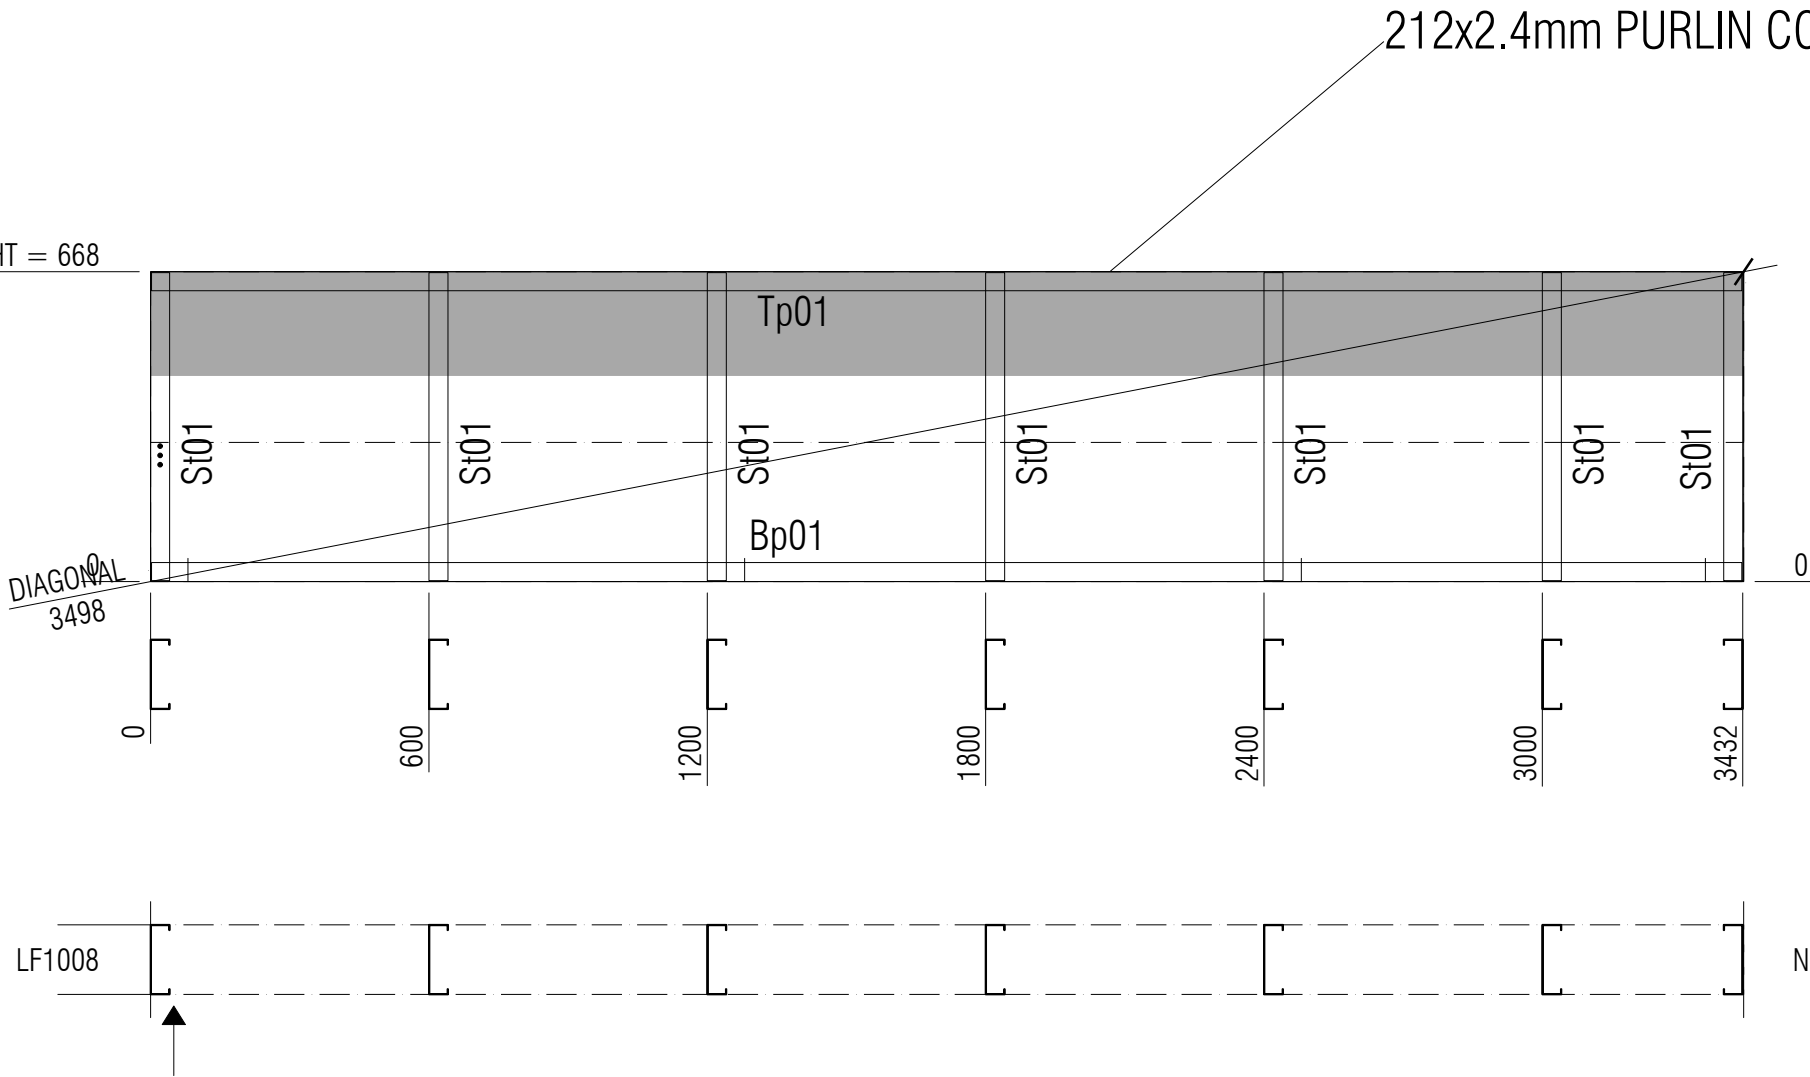

FRAME STICKS				
NAME	LENGTH	WT	QTY	PROFILE
Tp01	3428	6.3	1	150S41-950-500
Bp01	3428	6.3	1	150S41-950-500
St01	664	1.2	7	150S41-950-500
TOTAL	11504	21.2	9	



DELIVERING SINCE 2003

DRAWN: N.N

PH: 02 4860 1416
OFFICE: 02 4860 1400

REV	DATE	REASON

AUSTRUSS PROJECT NAME

CALDERWOOD

AUSTRUSS ZONE NUMBER

A1

CLIENT NAME

ADCO

PROJECT ADDRESS

179 CALDERWOOD ROAD
CALDERWOOD NSW 2527

AUSTRUSS PROJECT NUMBER

25363

DRAWING NAME

NF1005

DRAWING NUMBER

####

REV

0


SCAN FOR 3D




Design Summary	
Floor Type	Concrete
Roof Load	Auto
System	FC_AusTruss
Wind Load	N2

WELD PART

OVERALL HEIGHT = 668

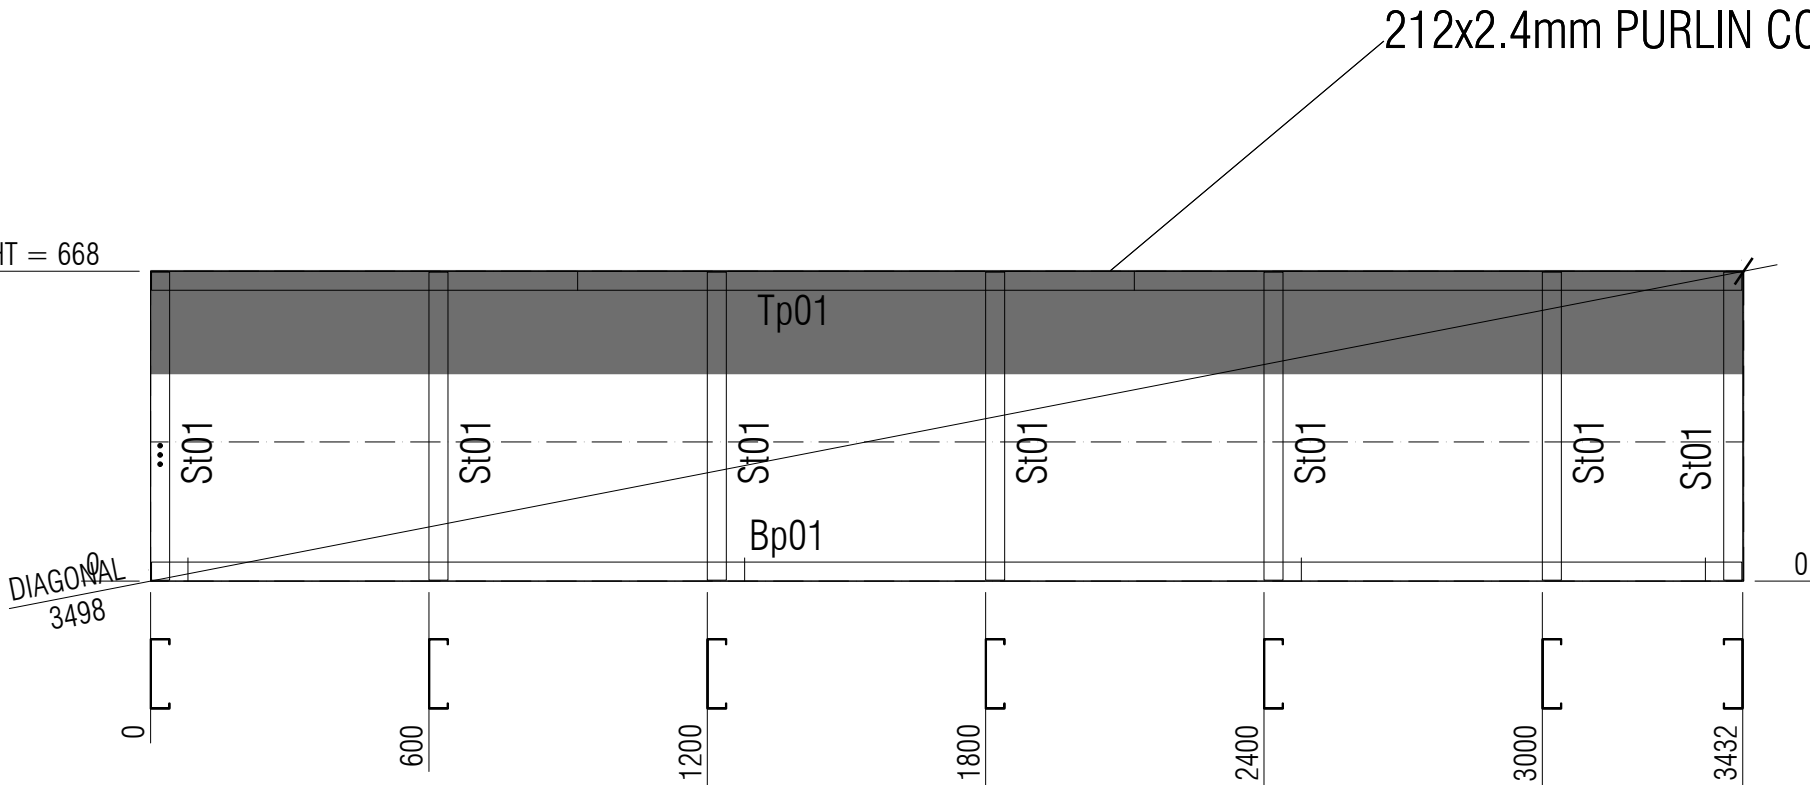

FRAME STICKS				
NAME	LENGTH	WT	QTY	PROFILE
Tp01	3428	6.3	1	150S41-950-500
Bp01	3428	6.3	1	150S41-950-500
St01	664	1.2	7	150S41-950-500
TOTAL	11504	21.2	9	

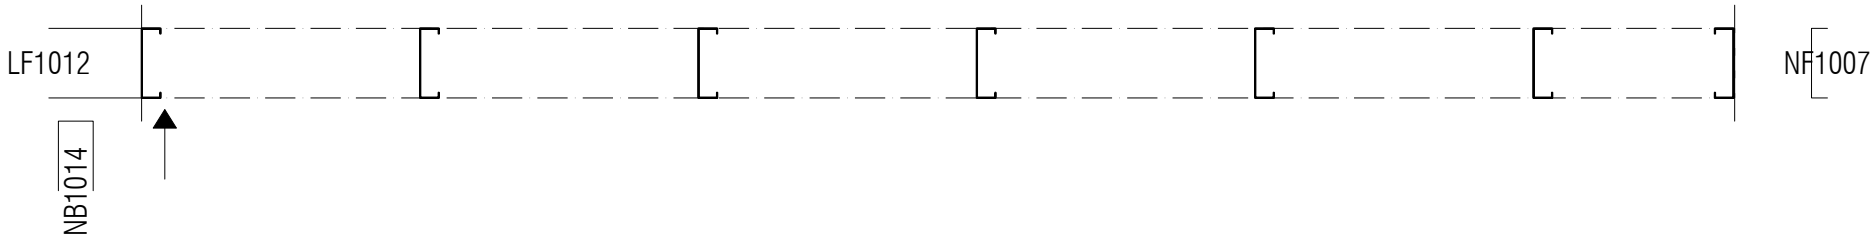


SCAN FOR 3D

AUSTRUSS		
DELIVERING SINCE 2003		
DRAWN: N.N		PH: 02 4860 1416
		OFFICE: 02 4860 1400
REV	DATE	REASON
AUSTRUSS PROJECT NAME		
CALDERWOOD		
AUSTRUSS ZONE NUMBER		
A1		
CLIENT NAME		
ADCO		
PROJECT ADDRESS		
179 CALDERWOOD ROAD		
CALDERWOOD NSW 2527		
AUSTRUSS PROJECT NUMBER		
25363		
DRAWING NAME		
NF1006		
DRAWING NUMBER		REV
####		0

Design Summary	
Floor Type	Concrete
Roof Load	Auto
System	FC_AusTruss
Wind Load	N2

WELD PART

OVERALL HEIGHT = 668

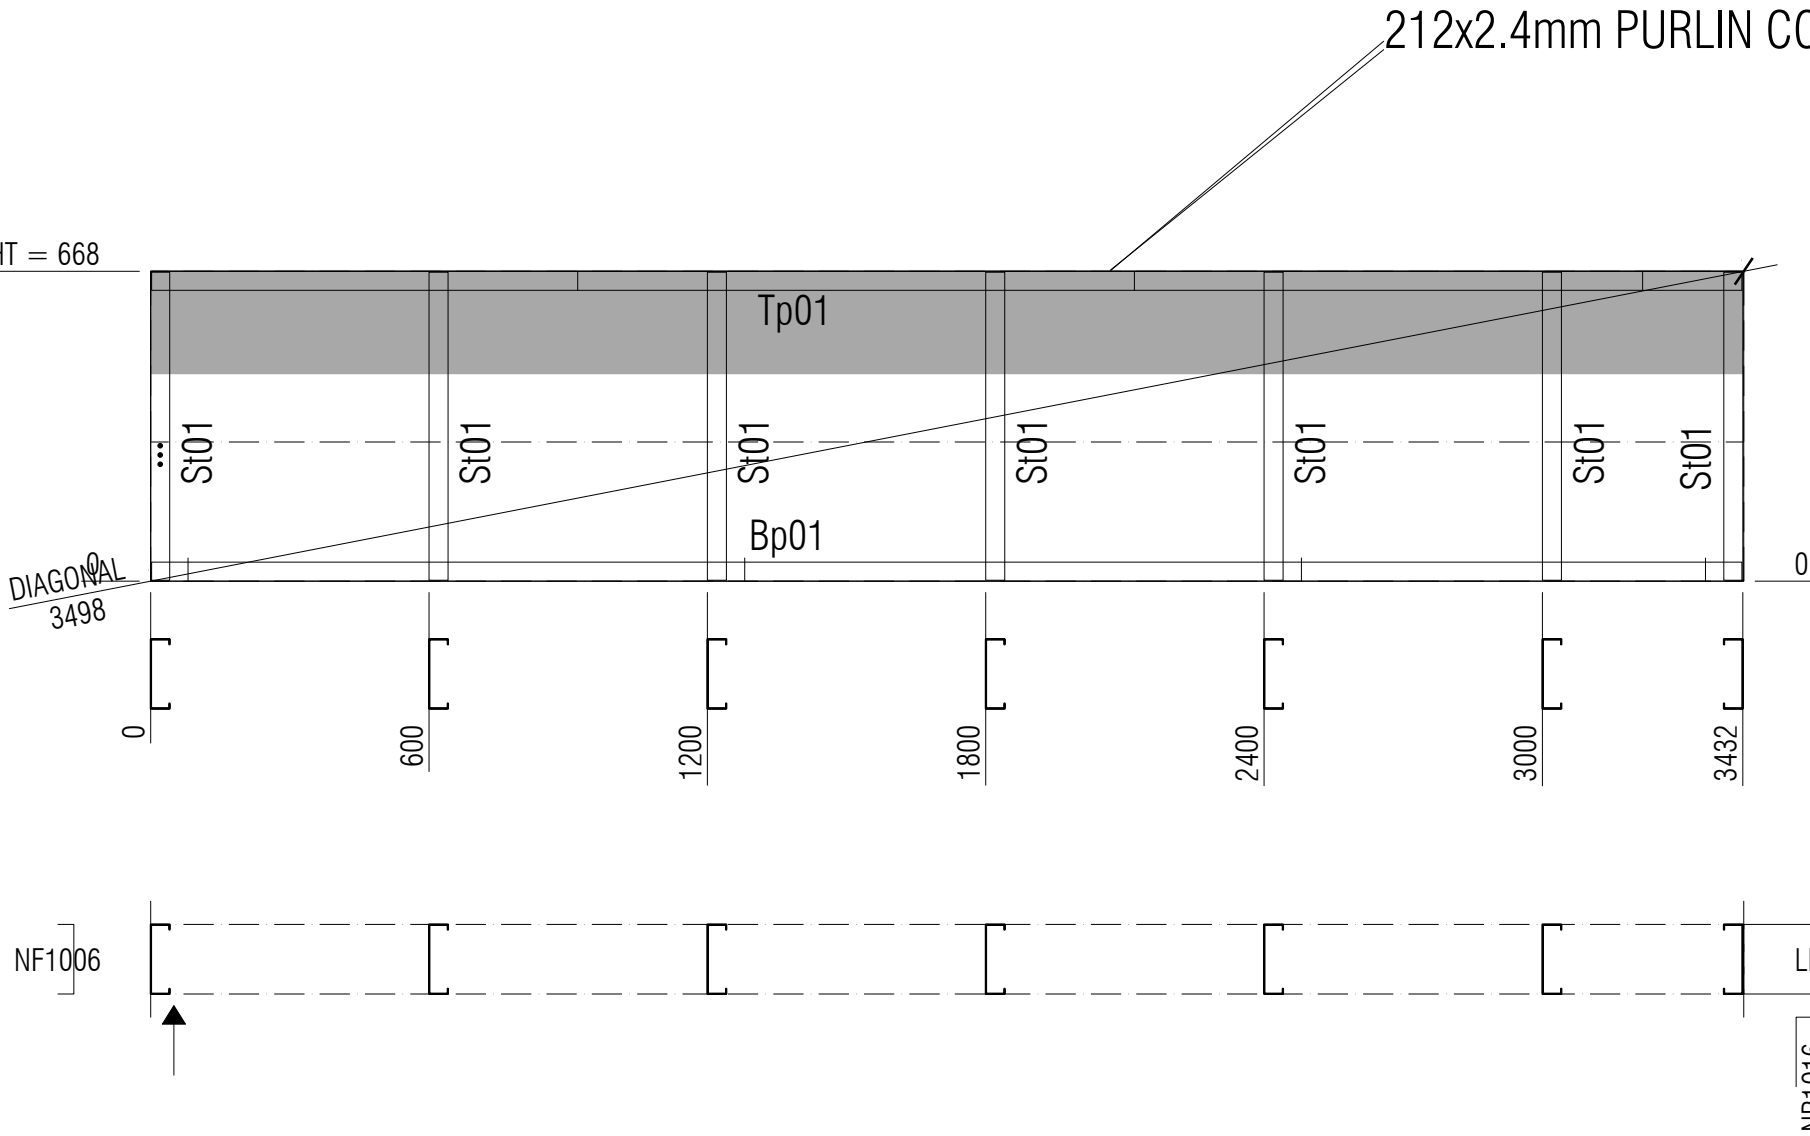

FRAME STICKS				
NAME	LENGTH	WT	QTY	PROFILE
Tp01	3428	6.3	1	150S41-950-500
Bp01	3428	6.3	1	150S41-950-500
St01	664	1.2	7	150S41-950-500
TOTAL	11504	21.2	9	



DELIVERING SINCE 2003

DRAWN: N.N

PH: 02 4860 1416
OFFICE: 02 4860 1400

REV	DATE	REASON

AUSTRUSS PROJECT NAME

CALDERWOOD

AUSTRUSS ZONE NUMBER

A1

CLIENT NAME

ADCO

PROJECT ADDRESS

179 CALDERWOOD ROAD
CALDERWOOD NSW 2527

AUSTRUSS PROJECT NUMBER

25363

DRAWING NAME

NF1007

DRAWING NUMBER

####

REV

0


SCAN FOR 3D




Design Summary	
Floor Type	Concrete
Roof Load	Auto
System	FC_AusTruss
Wind Load	N2

WELD PART

OVERALL HEIGHT = 668

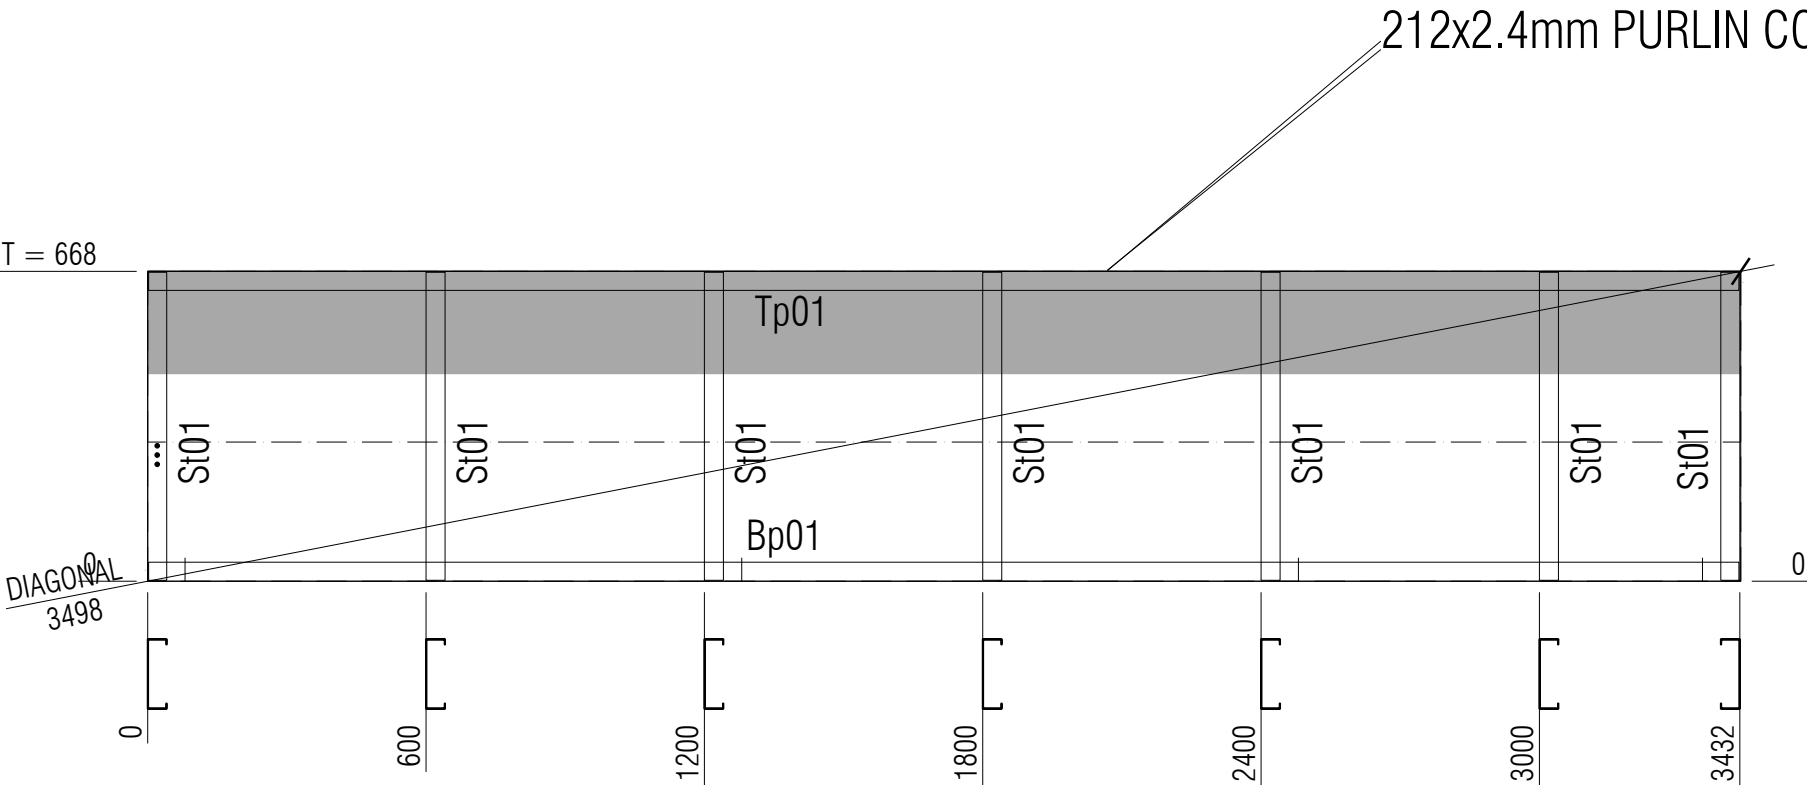

FRAME STICKS				
NAME	LENGTH	WT	QTY	PROFILE
Tp01	3428	6.3	1	150S41-950-500
Bp01	3428	6.3	1	150S41-950-500
St01	664	1.2	7	150S41-950-500
TOTAL	11504	21.2	9	

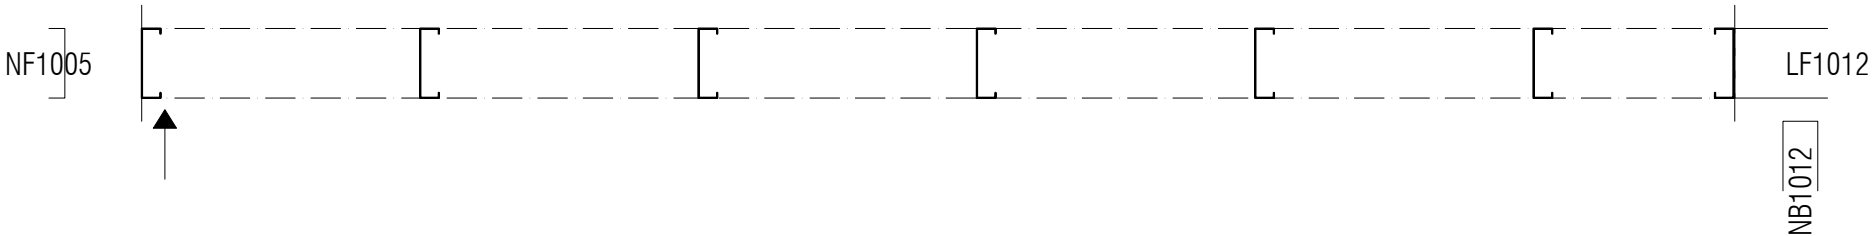


SCAN FOR 3D

 DELIVERING SINCE 2003		
DRAWN: N.N		PH: 02 4860 1416 OFFICE: 02 4860 1400
REV	DATE	REASON
AUSTRUSS PROJECT NAME CALDERWOOD		
AUSTRUSS ZONE NUMBER A1		
CLIENT NAME ADCO		
PROJECT ADDRESS 179 CALDERWOOD ROAD CALDERWOOD NSW 2527		
AUSTRUSS PROJECT NUMBER 25363		
DRAWING NAME NF1008		
DRAWING NUMBER ####		REV 0


Design Summary	
Floor Type	Concrete
Roof Load	Auto
System	FC_AusTruss
Wind Load	N2

WELD PART

OVERALL HEIGHT = 668

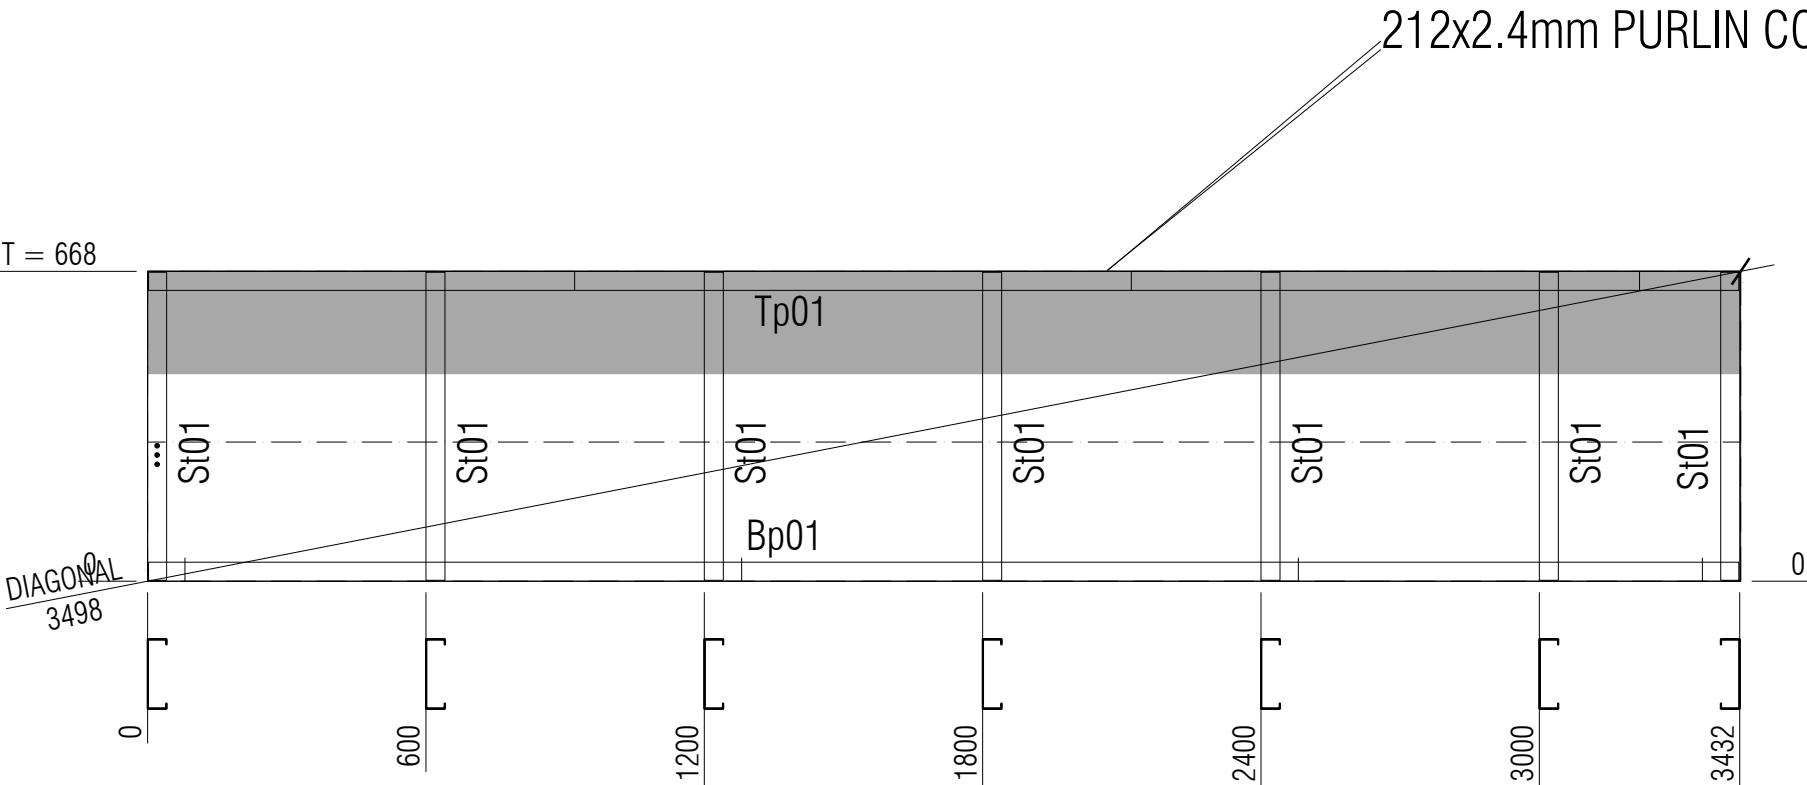

FRAME STICKS				
NAME	LENGTH	WT	QTY	PROFILE
Tp01	3428	6.3	1	150S41-950-500
Bp01	3428	6.3	1	150S41-950-500
St01	664	1.2	7	150S41-950-500
TOTAL	11504	21.2	9	

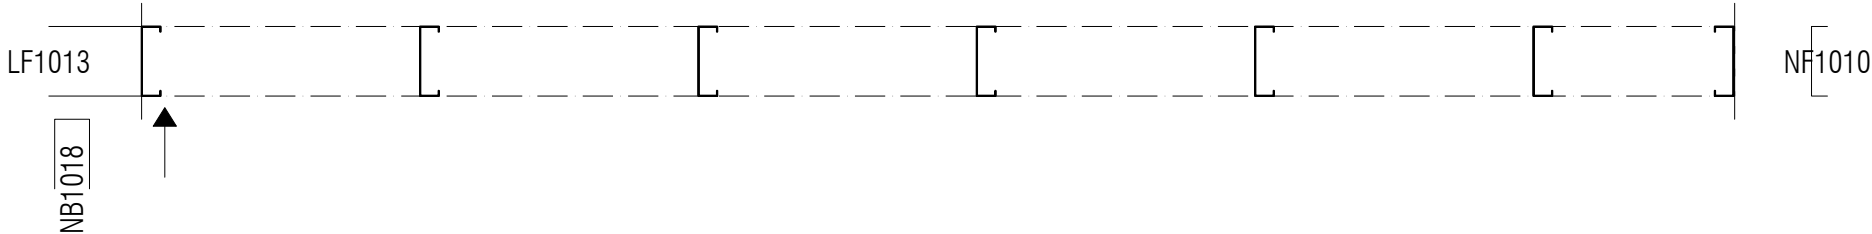


SCAN FOR 3D

AUSTRUSS		
DELIVERING SINCE 2003		
DRAWN: N.N		PH: 02 4860 1416
		OFFICE: 02 4860 1400
REV	DATE	REASON
AUSTRUSS PROJECT NAME		
CALDERWOOD		
AUSTRUSS ZONE NUMBER		
A1		
CLIENT NAME		
ADCO		
PROJECT ADDRESS		
179 CALDERWOOD ROAD		
CALDERWOOD NSW 2527		
AUSTRUSS PROJECT NUMBER		
25363		
DRAWING NAME		
NF1009		
DRAWING NUMBER		REV
####		0

Design Summary	
Floor Type	Concrete
Roof Load	Auto
System	FC_AusTruss
Wind Load	N2

WELD PART

OVERALL HEIGHT = 668

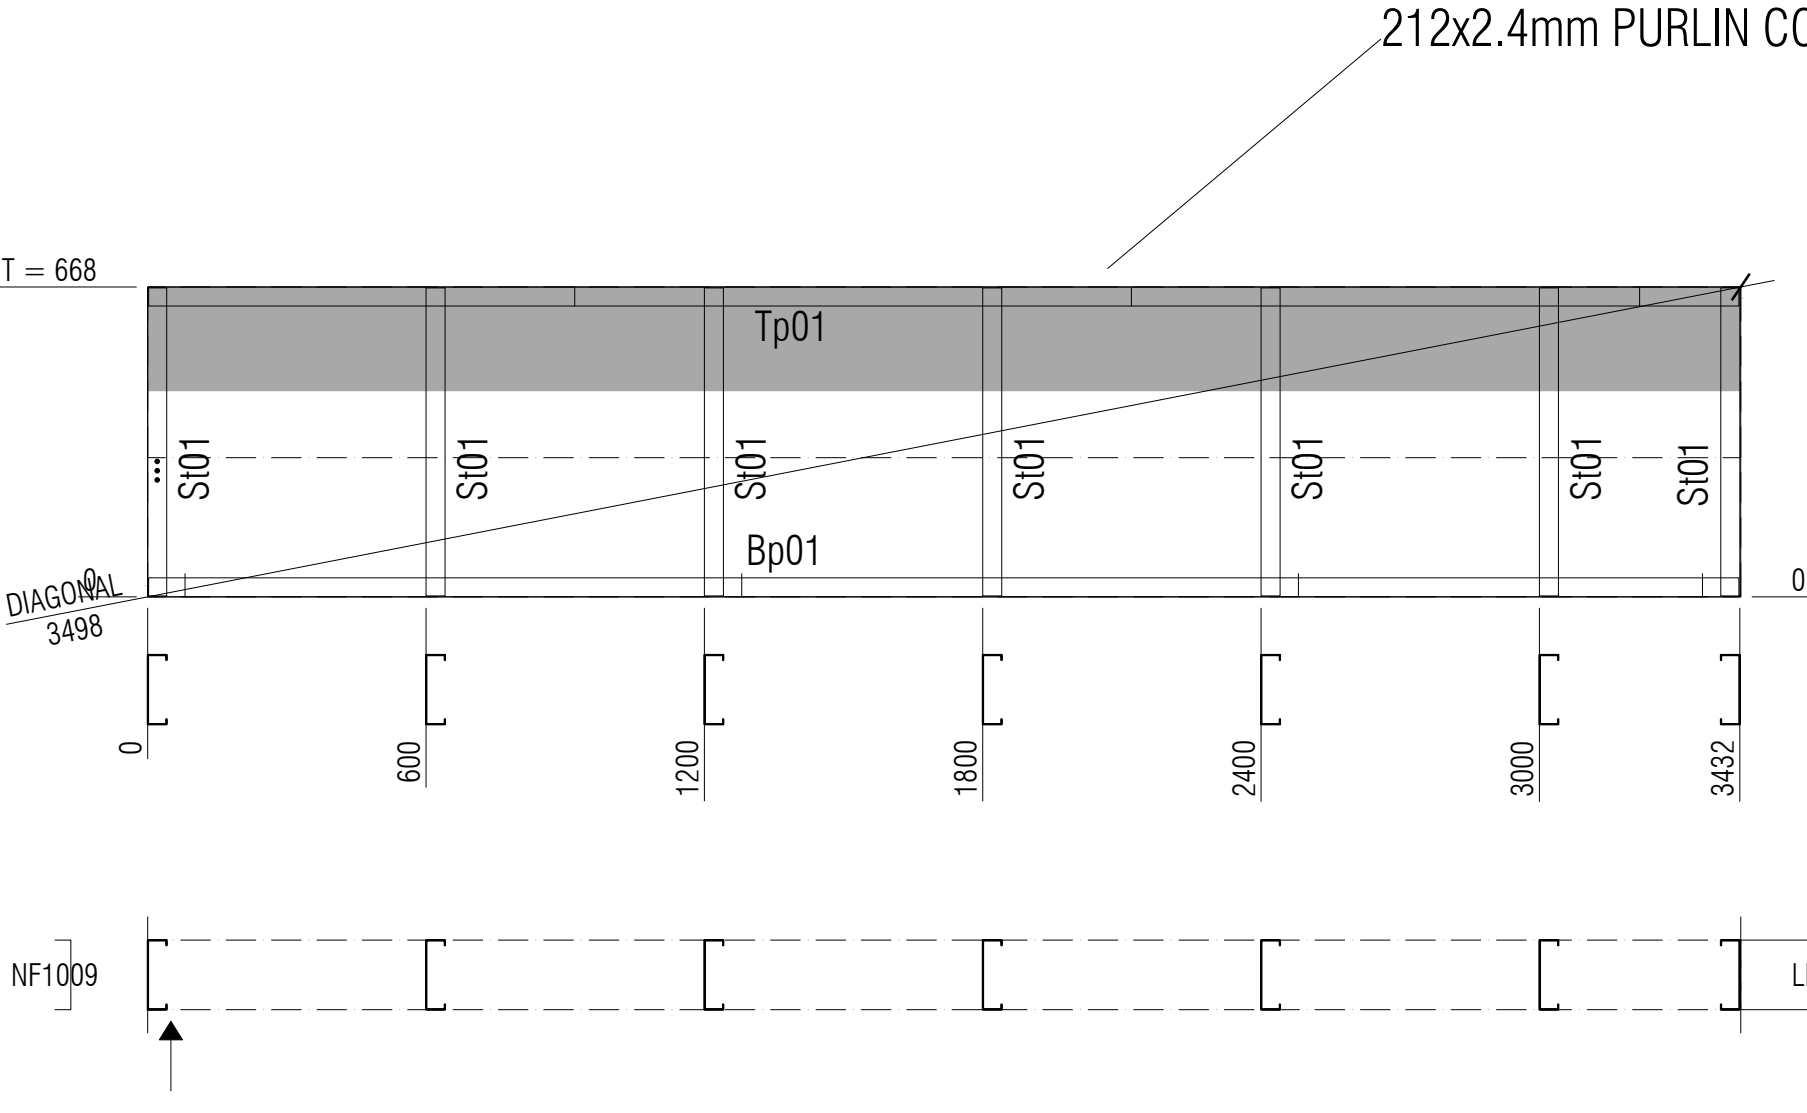

FRAME STICKS				
NAME	LENGTH	WT	QTY	PROFILE
Tp01	3428	6.3	1	150S41-950-500
Bp01	3428	6.3	1	150S41-950-500
St01	664	1.2	7	150S41-950-500
TOTAL	11504	21.2	9	



SCAN FOR 3D

 AUSTRUSS		
DELIVERING SINCE 2003		
DRAWN: N.N		PH: 02 4860 1416 OFFICE: 02 4860 1400
REV	DATE	REASON
AUSTRUSS PROJECT NAME		
CALDERWOOD		
AUSTRUSS ZONE NUMBER		
A1		
CLIENT NAME		
ADCO		
PROJECT ADDRESS		
179 CALDERWOOD ROAD CALDERWOOD NSW 2527		
AUSTRUSS PROJECT NUMBER		
25363		
DRAWING NAME		
NF1010		
DRAWING NUMBER		REV
####		0