


WELD ALL

150x1.9 SIDERAIL CAP TO TOP AND BOTTOM

DOUBLE GIRDER — 2× GI1000

DIAGONAL
7636

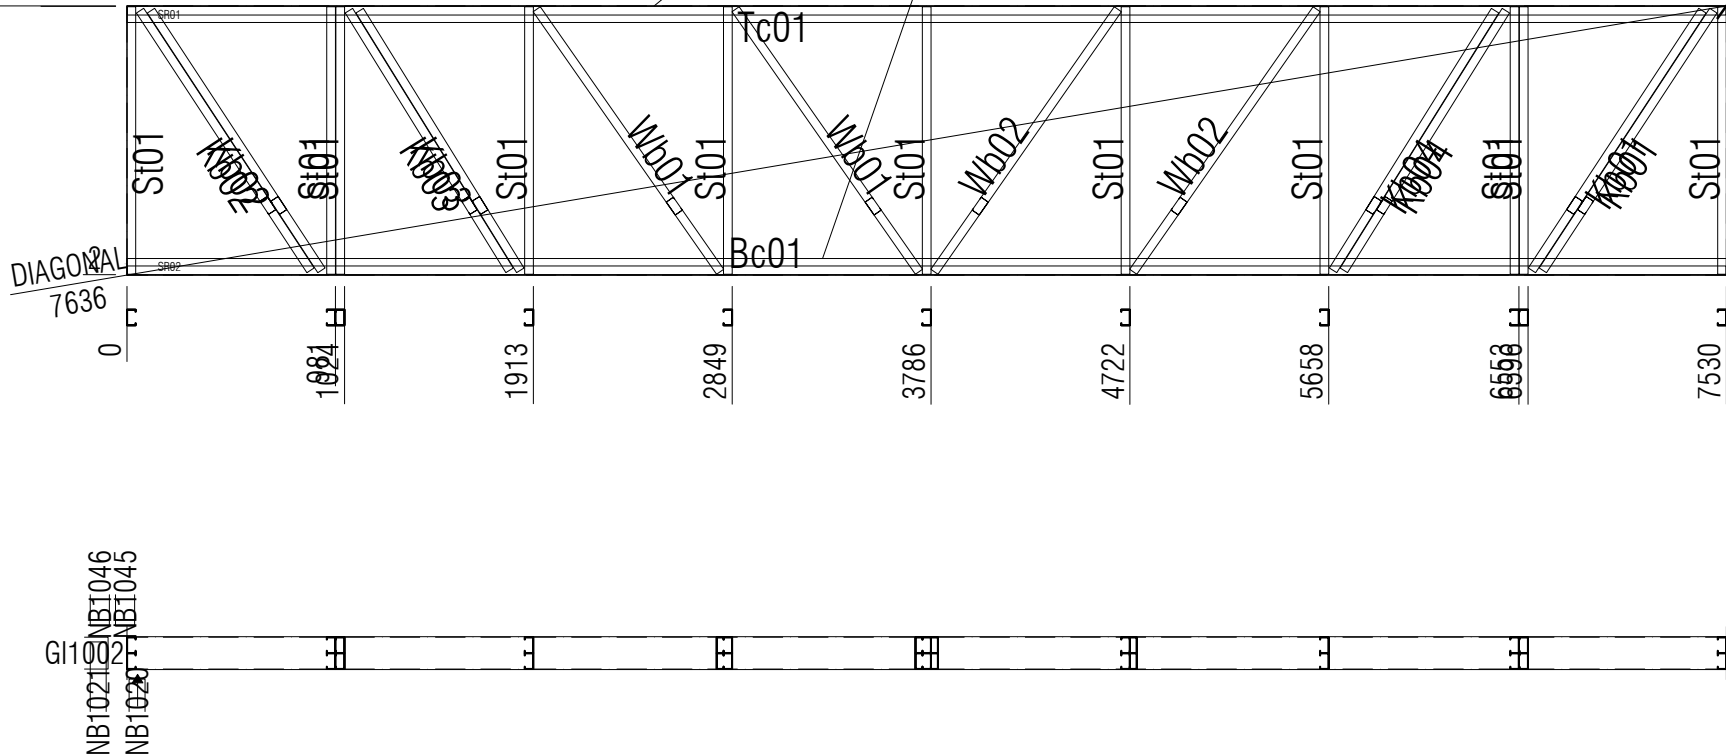

STEEL SUPPORT MEMBERS				
NAME	PROFILE	LENGTH	WT	QTY
SR9001	SR150x1.9	7530	33.5	1
SR9001	SR150x1.9	7530	33.5	1
TOTAL			67.0	2

A compass rose with a circle and a crosshair. The letter 'N' is at the top. A line points to the top of the circle, and another line points to the right of the circle. The angle between these two lines is labeled '10° E'.

SCAN FOR 3D

25363

DRAWING NAME
GI1000

DRAWING NUMBER
LGS-A1-230

REV	#####
-----	-------

Design Summary

Floor Type

Roof Load

System

Wind Load

Concrete

Auto

FC_AusTruss


N2

WELD ALL

40mm WELD EACH SIDE
FULLY WEDLED GIRDER BEFORE ASSEMBLY

150x1.9 SIDERAIL CAP TO TOP AND BOTTOM

OVERALL HEIGHT = 1265

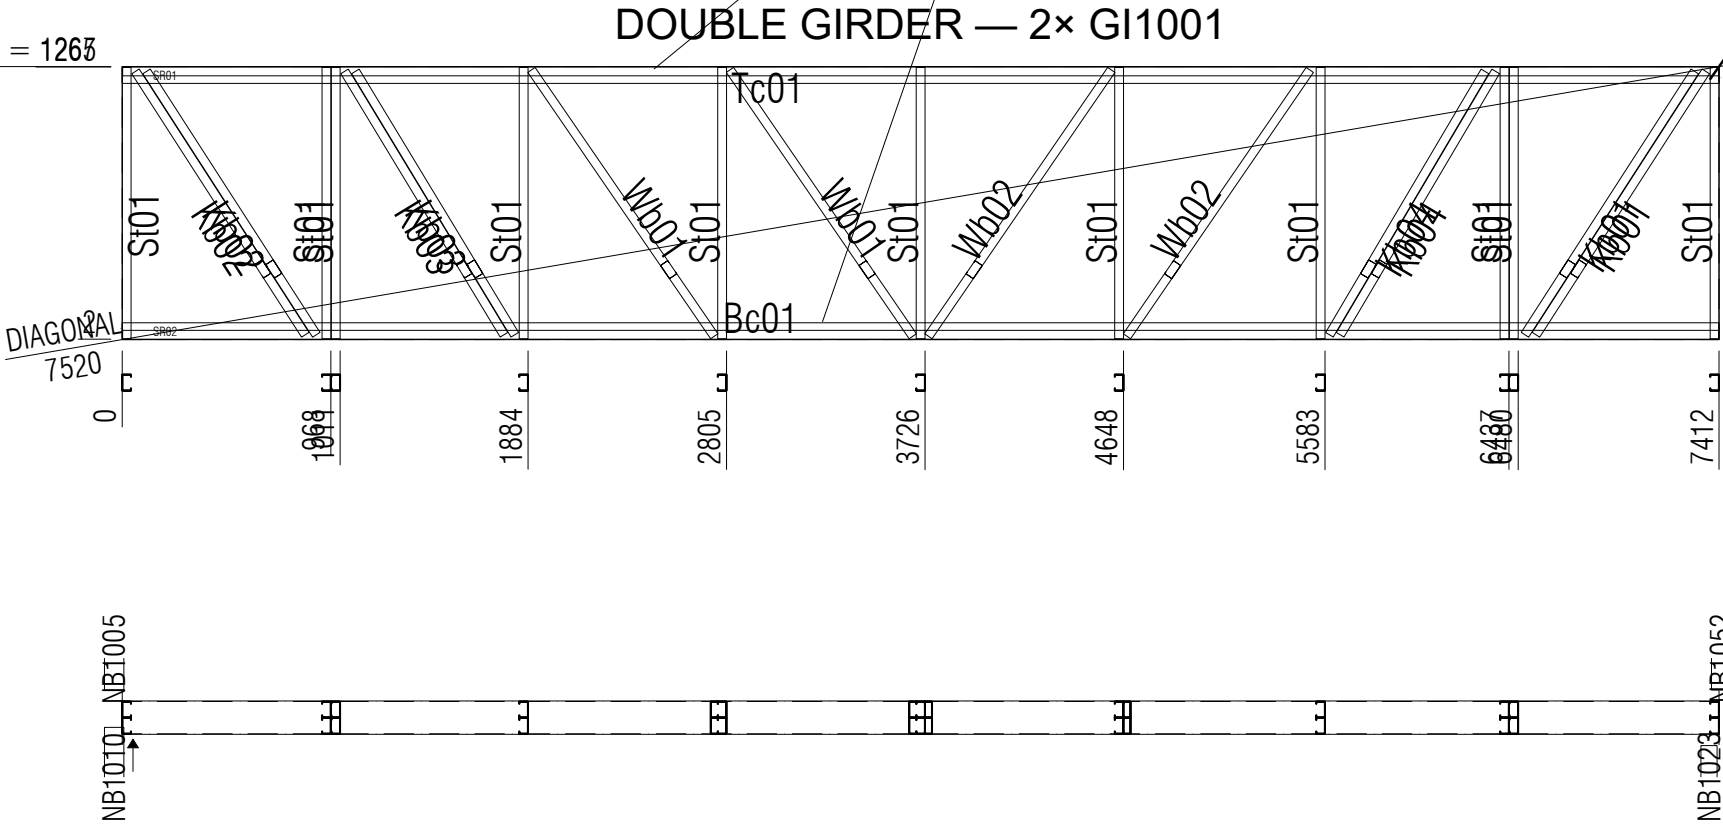

FRAME STICKS				
NAME	LENGTH	WT	QTY	PROFILE
St01	1260	1.6	22	75S41-950-500
Kb01	1455	1.9	4	75S41-950-500
Kb02	1455	1.9	4	75S41-950-500
Kb03	1429	1.8	4	75S41-950-500
Kb04	1420	1.8	4	75S41-950-500
Tc01	7408	9.5	2	75S41-950-500
Bc01	7408	9.5	2	75S41-950-500
Wb01	1500	1.9	4	75S41-950-500
Wb02	1500	1.9	4	75S41-950-500
TOTAL	92370	118.2	50	

STEEL SUPPORT MEMBERS				
NAME	PROFILE	LENGTH	WT	QTY
SR9000	SR150x1.9	7412	33.0	1
SR9000	SR150x1.9	7412	33.0	1
TOTAL			66.0	2

AUSTRUSS

DELIVERING SINCE 2003

DRAWN: N.N

PH: 02 4860 1416

OFFICE: 02 4860 1400

REV	DATE	REASON

AUSTRUSS PROJECT NAME

CALDERWOOD

AUSTRUSS ZONE NUMBER

####

CLIENT NAME

ADCO

PROJECT ADDRESS

179 CALDERWOOD ROAD

CALDERWOOD NSW 2527

AUSTRUSS PROJECT NUMBER

25363

DRAWING NAME

GI1001

DRAWING NUMBER

####

REV

####

SCAN FOR 3D



Design Summary

Floor Type

Roof Load

System

Wind Load

Concrete

Auto

FC_AusTruss


N2

WELD ALL

40mm WELD EACH SIDE
FULLY WEDLED GIRDER BEFORE ASSEMBLY

150x1.9 SIDERAIL CAP TO TOP AND BOTTOM

OVERALL HEIGHT = 1265

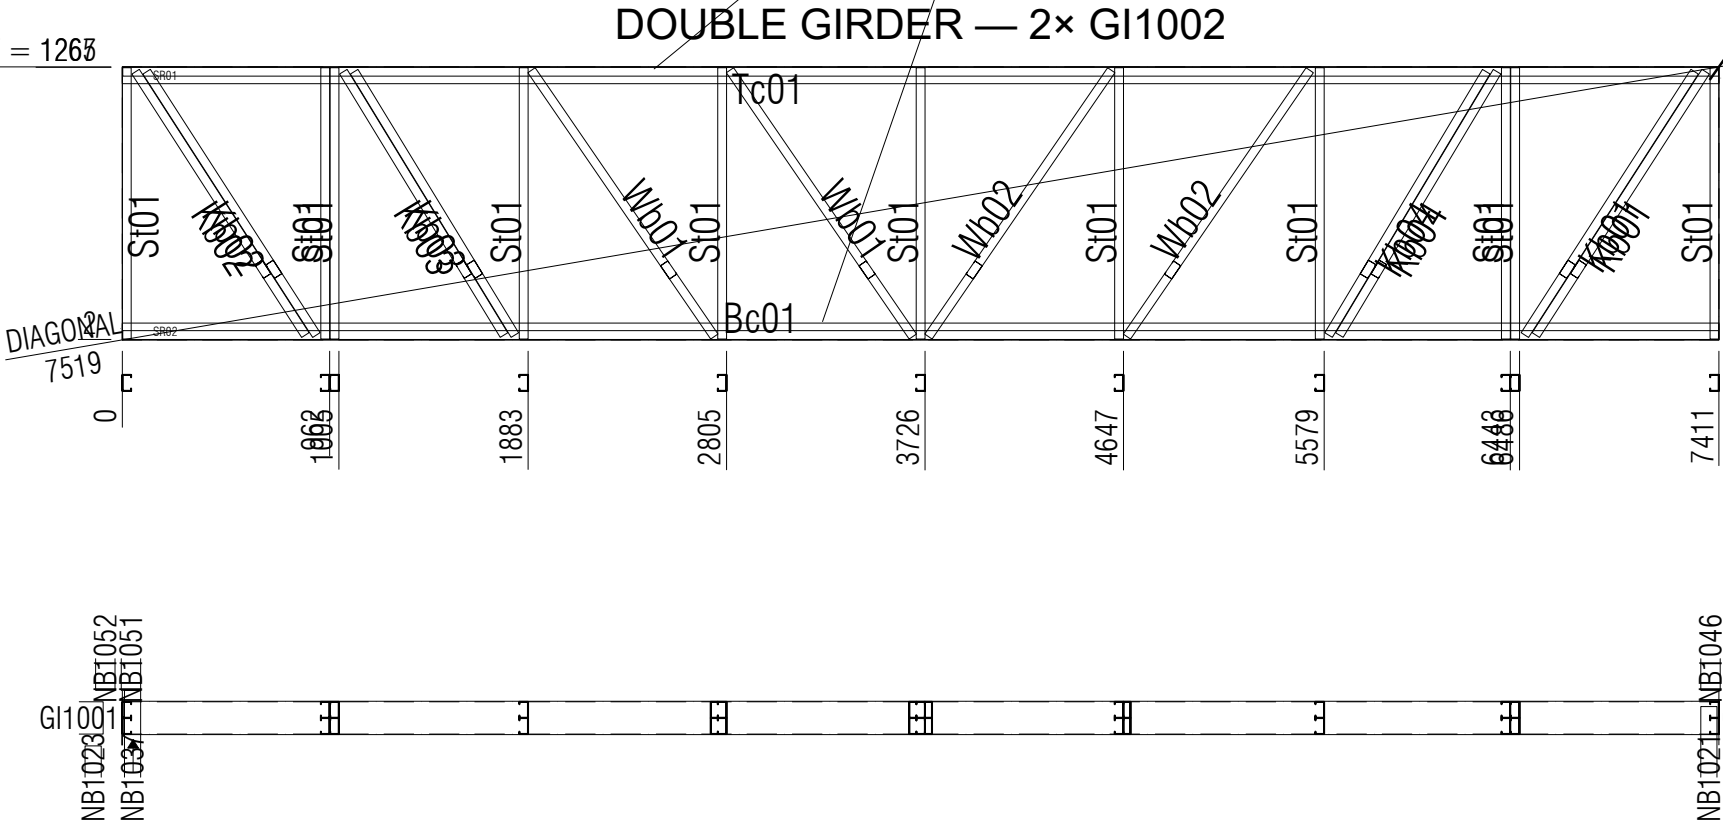

FRAME STICKS				
NAME	LENGTH	WT	QTY	PROFILE
St01	1260	1.6	22	75S41-950-500
Kb01	1455	1.9	4	75S41-950-500
Kb02	1455	1.9	4	75S41-950-500
Kb03	1432	1.8	4	75S41-950-500
Kb04	1425	1.8	4	75S41-950-500
Tc01	7407	9.5	2	75S41-950-500
Bc01	7407	9.5	2	75S41-950-500
Wb01	1500	1.9	4	75S41-950-500
Wb02	1500	1.9	4	75S41-950-500
TOTAL	92398	118.3	50	

STEEL SUPPORT MEMBERS				
NAME	PROFILE	LENGTH	WT	QTY
SR9000	SR150x1.9	7411	33.0	1
SR9000	SR150x1.9	7411	33.0	1
TOTAL			66.0	2



DRAWN: N.N PH: 02 4860 1416
OFFICE: 02 4860 1400

REV	DATE	REASON

AUSTRUSS PROJECT NAME
CALDERWOOD

AUSTRUSS ZONE NUMBER
####

CLIENT NAME
ADCO

PROJECT ADDRESS
**179 CALDERWOOD ROAD
CALDERWOOD NSW 2527**

AUSTRUSS PROJECT NUMBER
25363

DRAWING NAME
GI1002

DRAWING NUMBER
####

REV
####



SCAN FOR 3D