
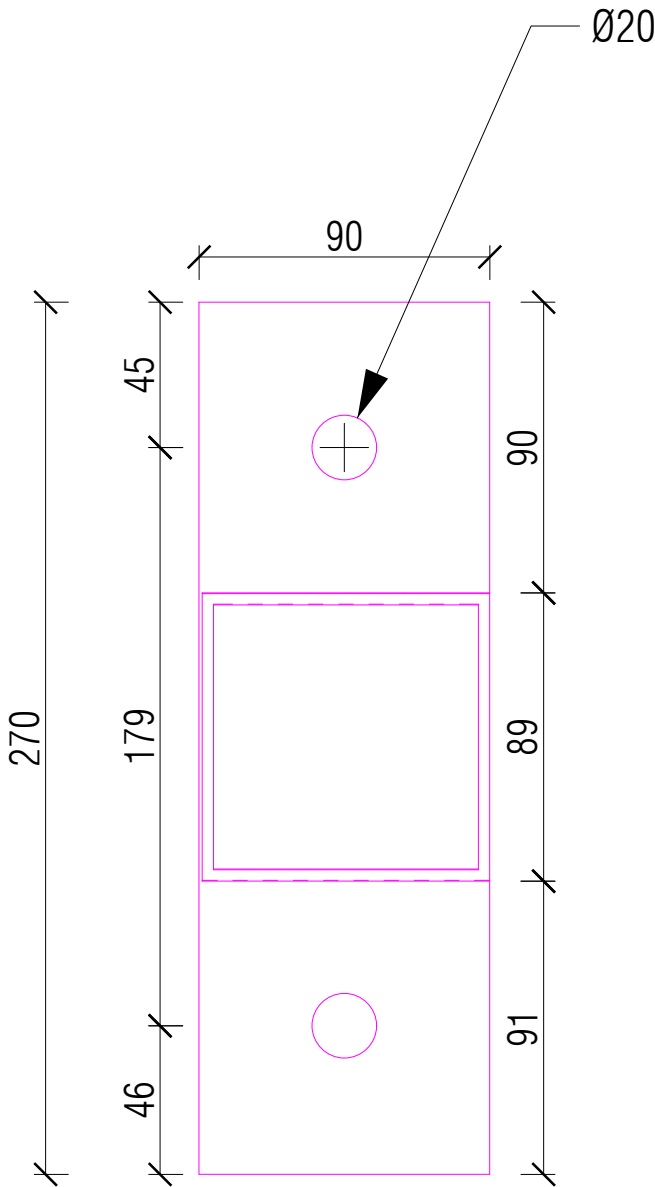
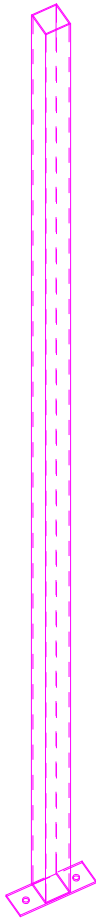



MARK	QTY	LENGTH (mm)	WEIGHT (kg)
C1006	1	4425	37

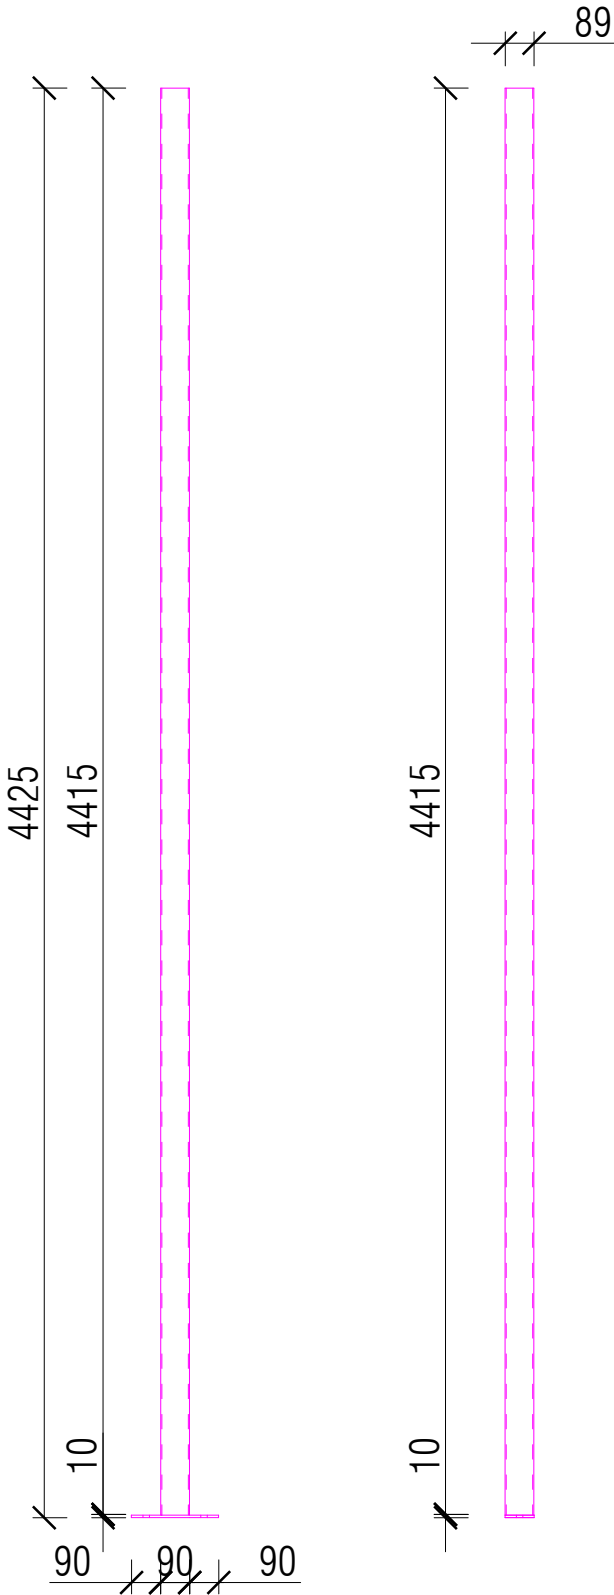

ITEM	QTY	MATERIAL	LENGTH	NOTE	FINISH	UNIT WEIGHT (kg)
1	1	89 x 3.5 SHS	4415	-	REC-PAINTED	
2	1	PL_90x10	270	-	REC-PAINTED	37

 www.austruss.com.au (02) 4860 1400 DWG FILE: #####	DRAWN N.N Ph:02 4860 1416	ISSUE	DATE	DESCRIPTION OF REVISION	Client/Company Name		Project Name		Building / Zone / Area		Job Number	
		0	28/07/26	IFA	ADCO		CALDERWOOD		ZONE B1		25363	
		A	18/08/26	IFC	Project Address		Drawing Name		Drawing Number		Revision	
					179 Calderwood Road Calderwood 2527		STRUCTURAL PRODUCTION		LGS-B1-281		A	
					NOTE: USE PROVIDED DIMENSIONS ONLY. IF NOT PROVIDED, ASK.		Scale: 1:34.4					

MARK	QTY	LENGTH (mm)	WEIGHT (kg)
C1005	3	4425	74

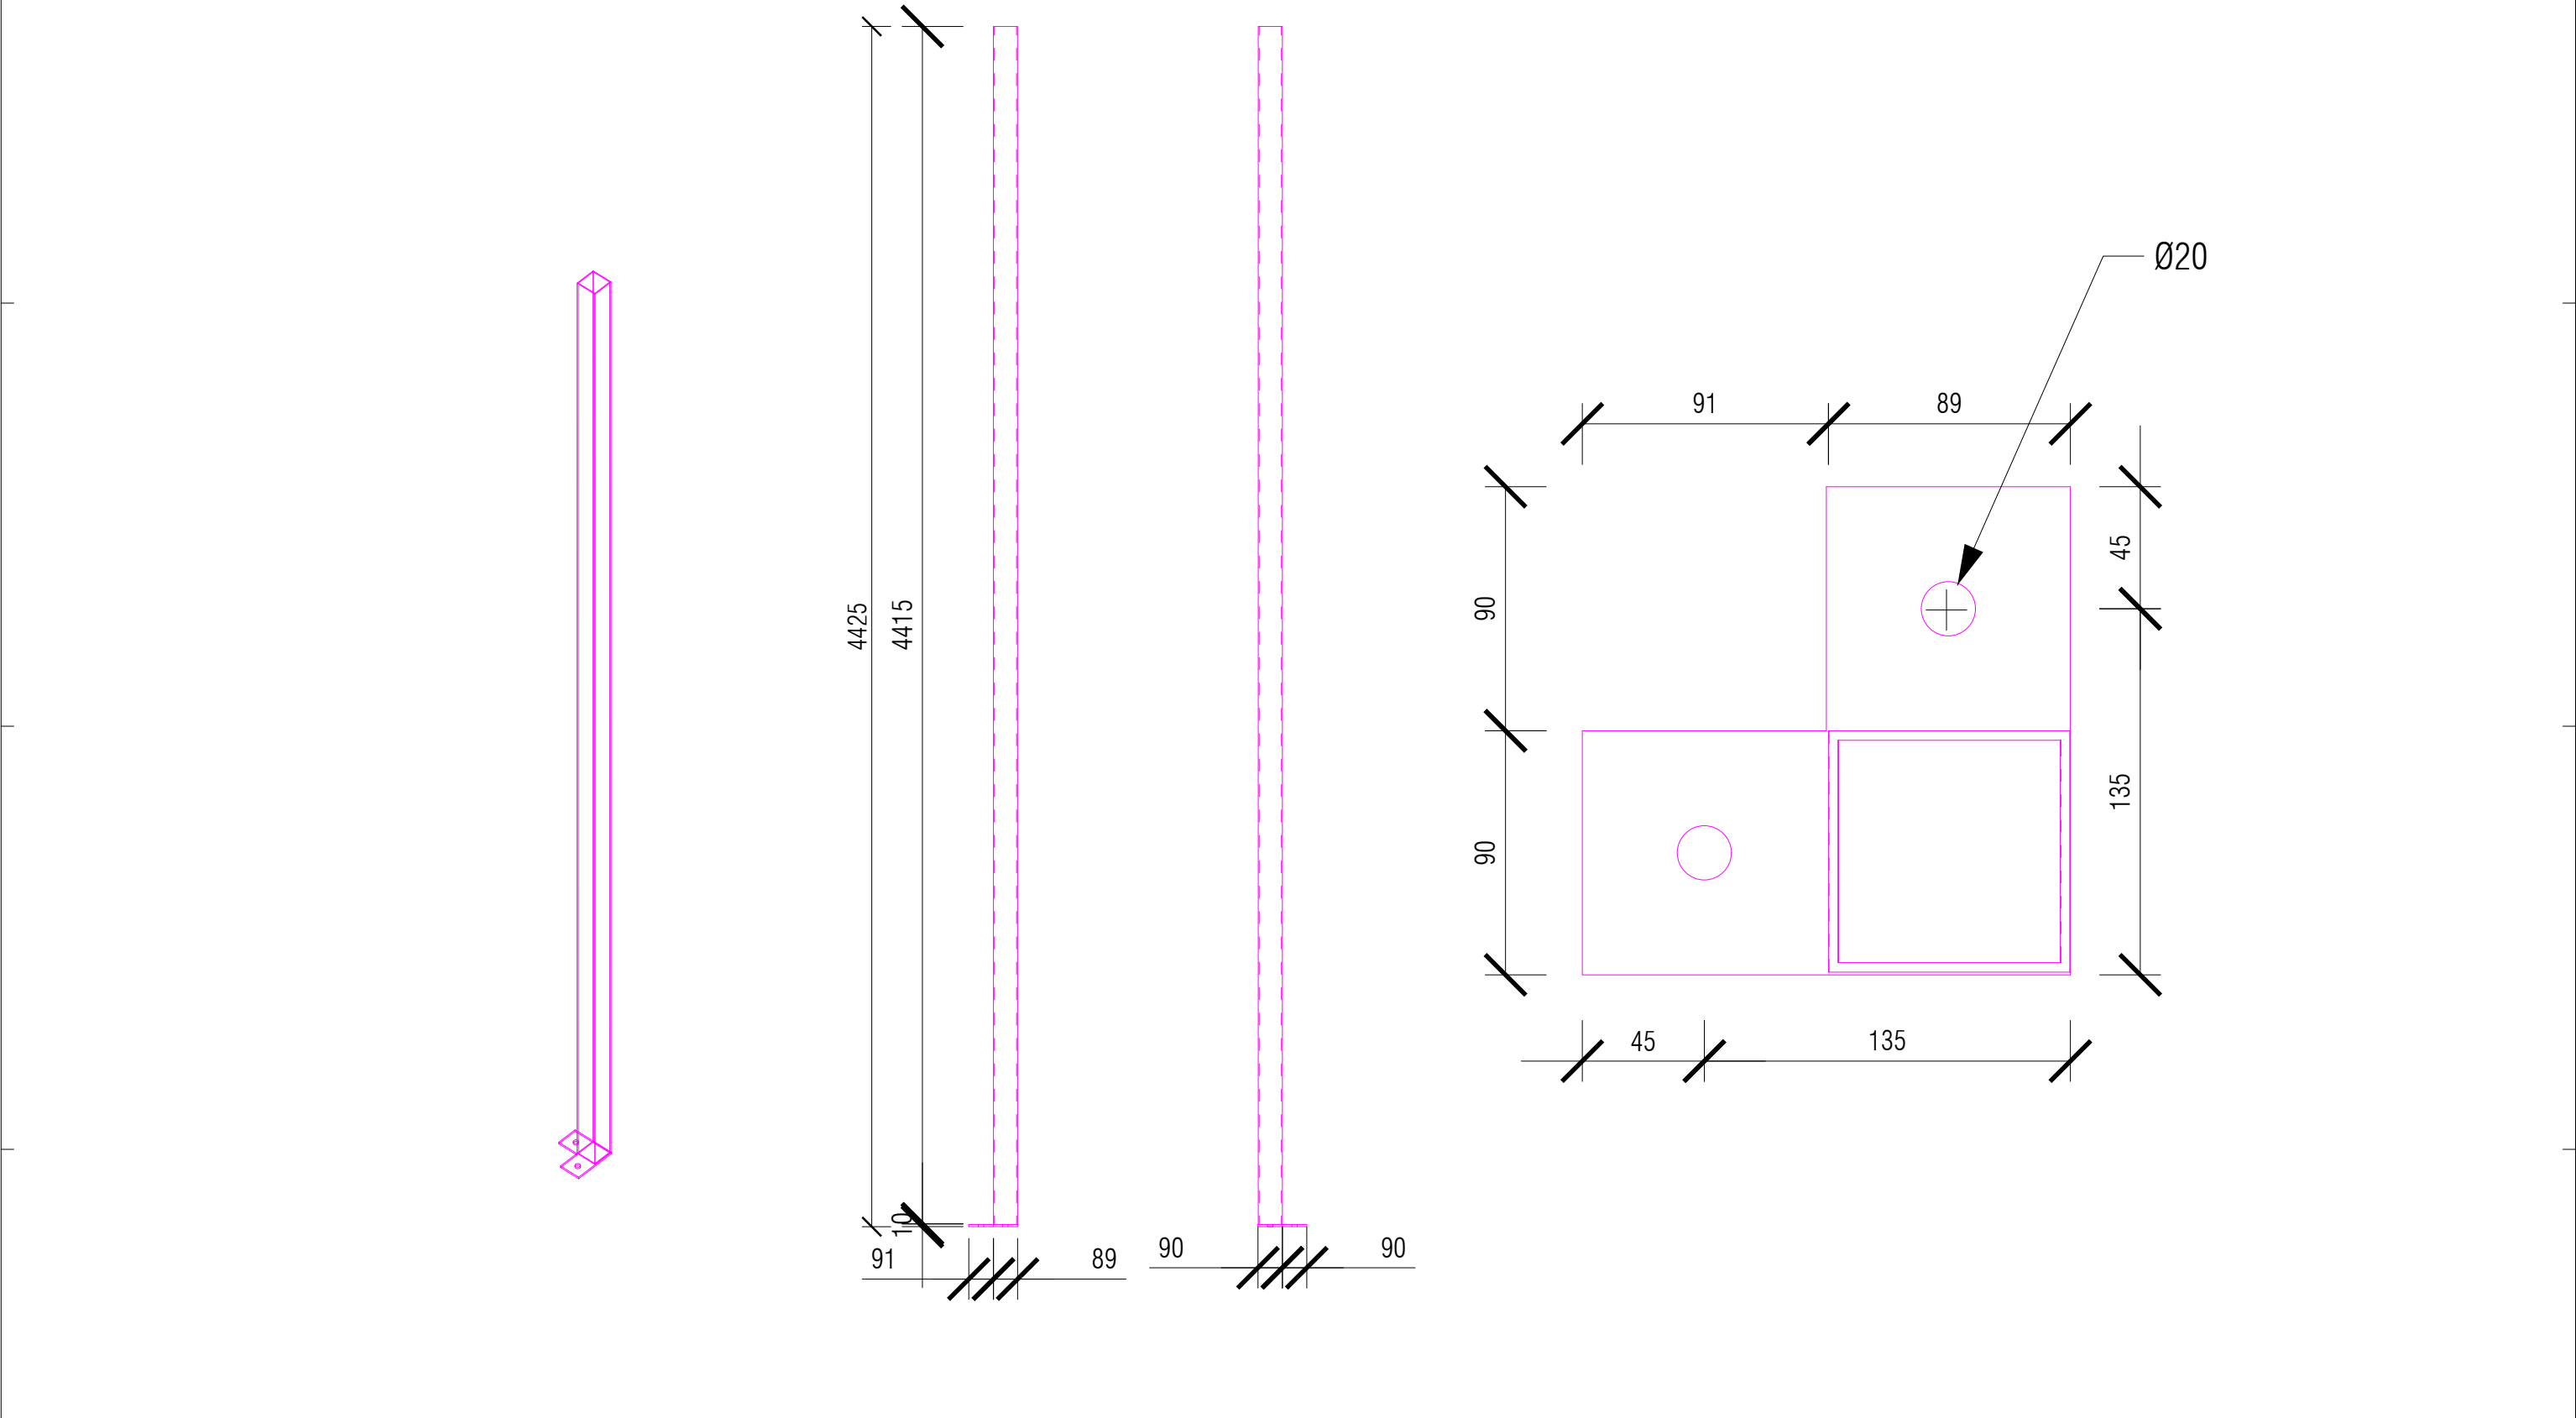

ITEM	QTY	MATERIAL	LENGTH	NOTE	FINISH				
1	1	89 x 3.5 SHS	4415	-	REC-PAINTED	UNIT WEIGHT (kg)			
2	1	PL_200x10	CHK DRAWING	-	REC-PAINTED	37			

 AUSTRUSS www.austruss.com.au (02) 4860 1400 DWG FILE: #####	DRAWN N.N Ph:02 4860 1416	ISSUE	DATE	DESCRIPTION OF REVISION	Client/Company Name		Project Name		Building / Zone / Area		Job Number		
		0	28/07/26	IFA	ADCO		CALDERWOOD		ZONE B1		25363		
		A	18/08/26	IFC									
					Project Address				Drawing Name		Drawing Number		
					179 Calderwood Road Calderwood 2527				STRUCTURAL PRODUCTION		LGS-B1-282		
					NOTE: USE PROVIDED DIMENSIONS ONLY. IF NOT PROVIDED, ASK.		Scale: 1:34.4				Revision		
A													