

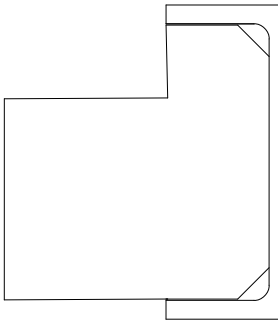
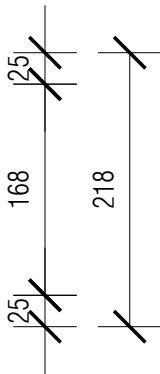
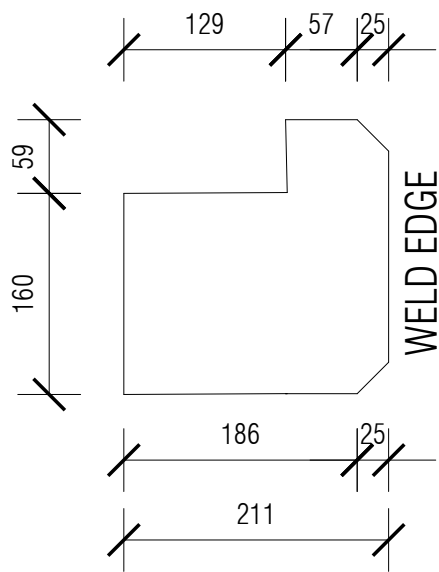


MARK	QTY	LENGTH (mm)	WEIGHT (kg)
PFC3001	1	5382	204

	NAME	DATE	SIG.
FAB BY			
CHECKED BY			

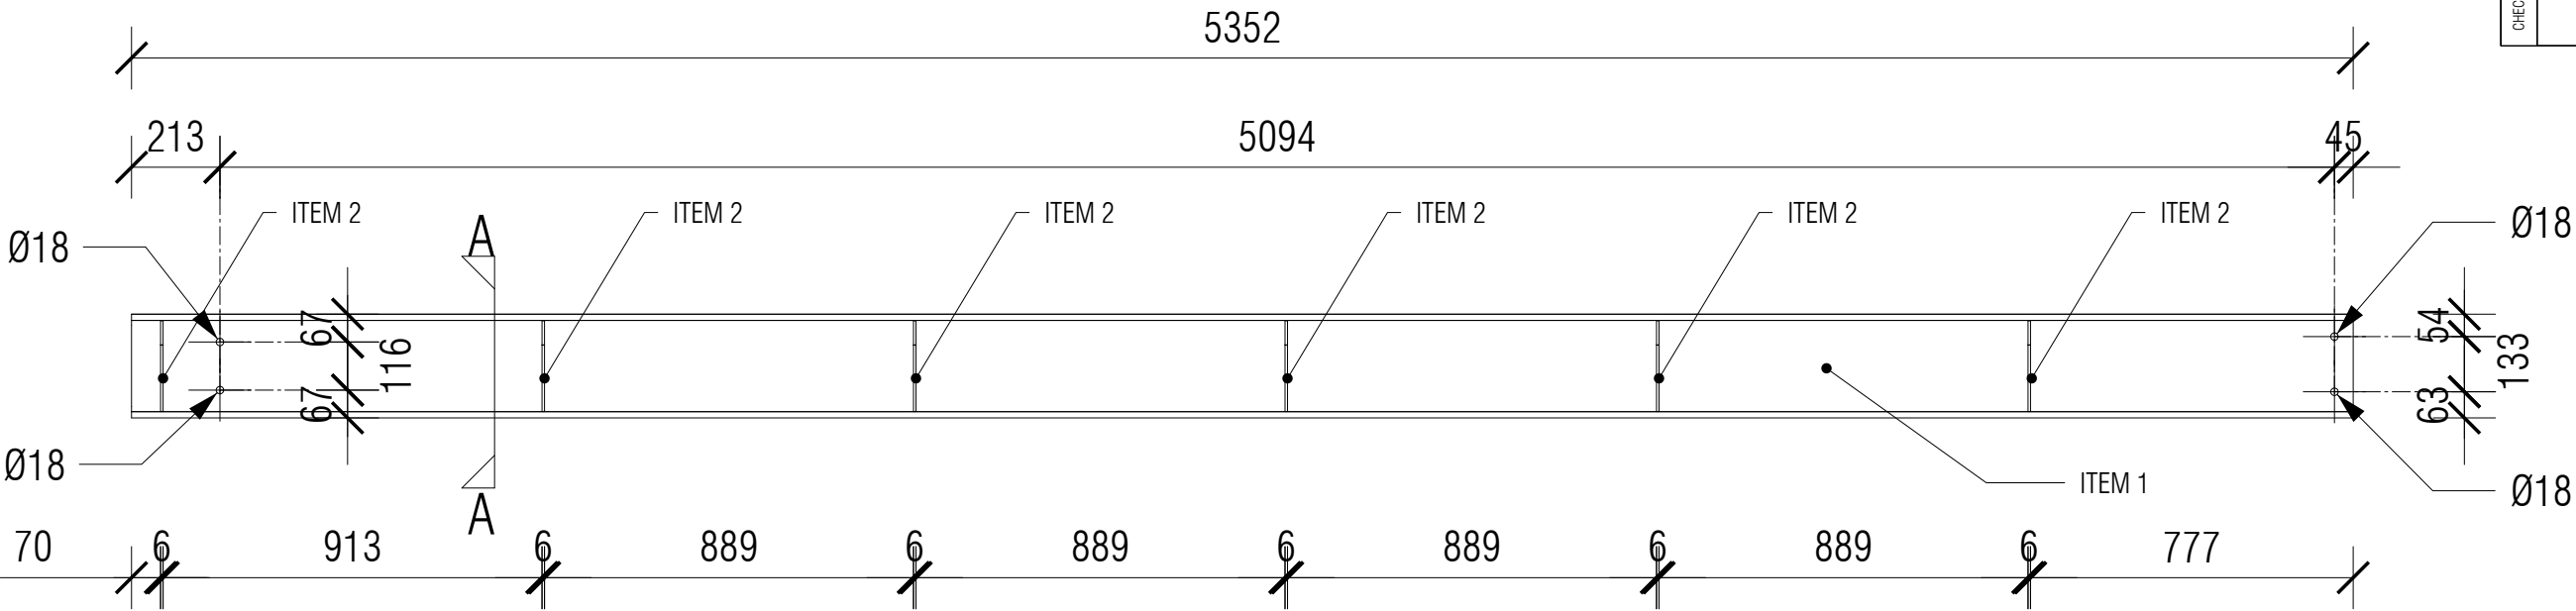

SECTION A-A

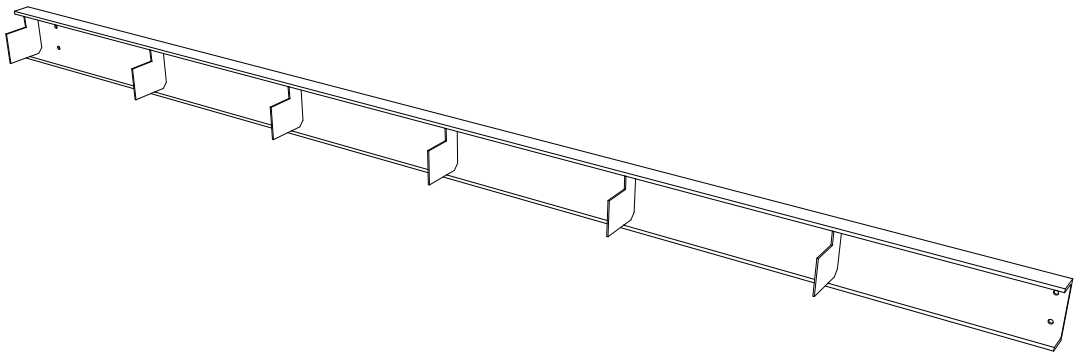

ITEM	QTY	MATERIAL	LENGTH	NOTE	FINISH	
1	1	250 PFC	5382	4x Ø18 HOLES	NEW PAINT	
2	6	PL_211x6	218	-	NEW PAINT	UNIT WEIGHT (kg)
-	-	-	-	-	-	204



www.austruss.com.au(02) 4860 1400

DRAWN
Mitchell.H
Ph:02 4860 1426

ISSUE	DATE	DESCRIPTION OF REVISION
A	16/08/26	IFC
B	18/08/26	IFC
C	24/08/26	IFC

Client/Company Name
ADCO

Project Address
Third Ave, Condell Park, NSW 2200

NOTE: USE PROVIDED DIMENSIONS ONLY. IF NOT PROVIDED, ASK.

Project Name
Condell Park_CPHS

Building / Zone / Area
Zone 3 (Building 0 - Level 2)

Drawing Name
STRUCTURAL PRODUCTION

Job Number
24400






Drawing Number
LGS-3-280

Revision
C

DWG FILE: ###

MARK	QTY	LENGTH (mm)	WEIGHT (kg)
C3000	1	353	6

	NAME	DATE	SIG.
FAB BY			
CHECKED BY			

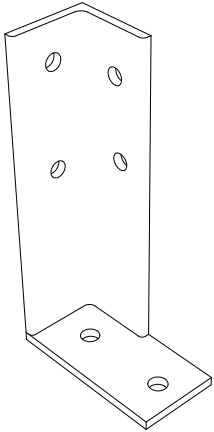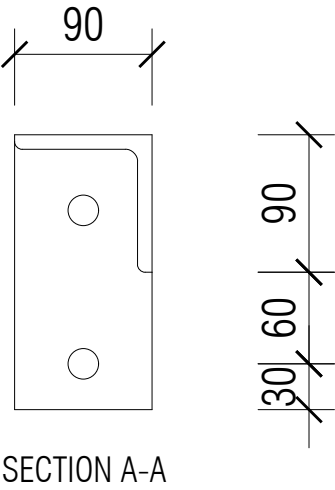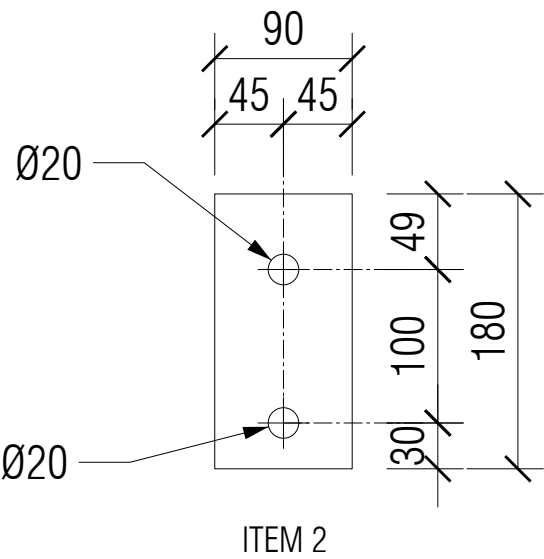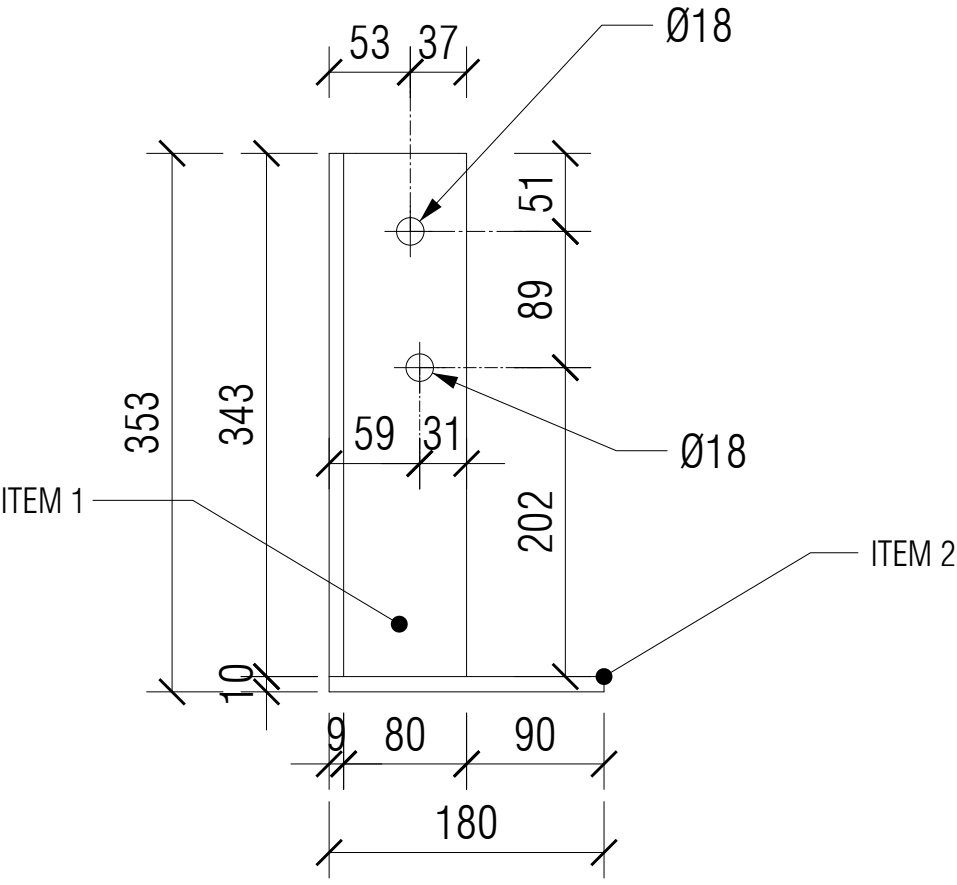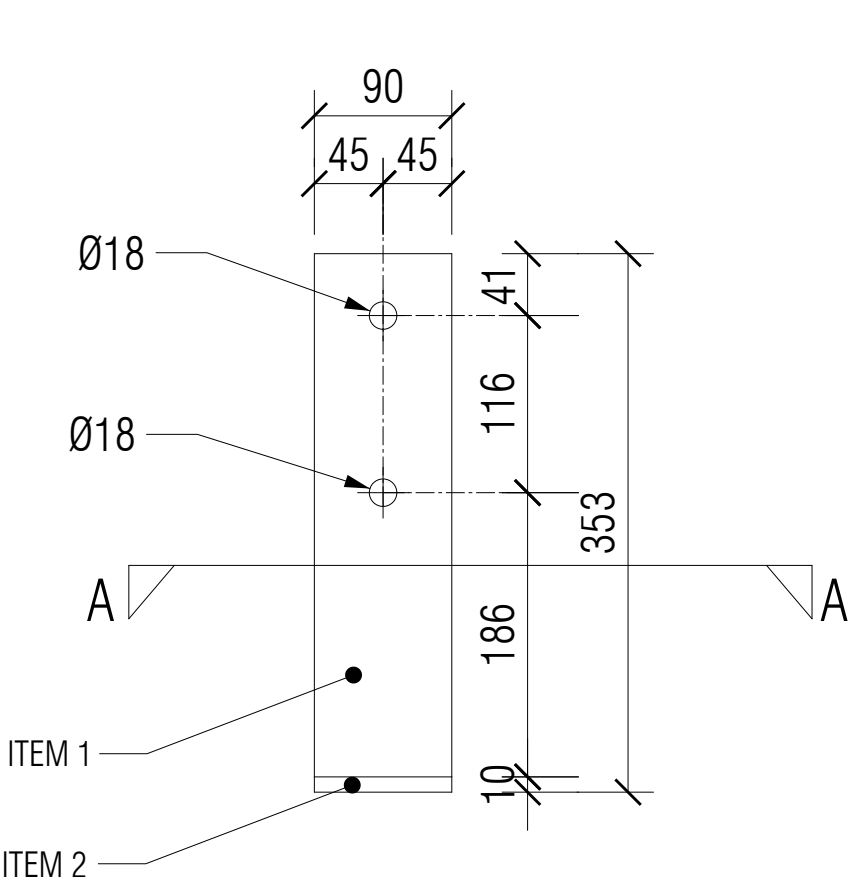




ITEM	QTY	MATERIAL	LENGTH	NOTE	FINISH
1	1	EA_90x10	343	4x Ø18 HOLES	REC PAINT
2	1	PL_90x10	180	2x Ø20 HOLES	REC PAINT
-	-	-	-	-	-

UNIT WEIGHT (kg)
6

 www.austruss.com.au(02) 4860 1400 DWG FILE: ####	DRAWN Mitchell.H Ph:02 4860 1426	ISSUE	DATE	DESCRIPTION OF REVISION	Client/Company Name		Project Name		Building / Zone / Area		Job Number		
		A	16/08/26	IFC	ADCO		Condell Park_CPHS		Zone 3 (Building 0 - Level 2)		24400		
		B	18/08/26	IFC									
						Project Address		Drawing Name		Drawing Number		Revision	
						Third Ave, Condell Park, NSW 2200		STRUCTURAL PRODUCTION		LGS-3-280		B	
						NOTE: USE PROVIDED DIMENSIONS ONLY. IF NOT PROVIDED, ASK.				Scale: NTS			

MARK	QTY	LENGTH (mm)	WEIGHT (kg)
A3000	1	150	2

	NAME	DATE	SIG.
FAB BY			
CHECKED BY			

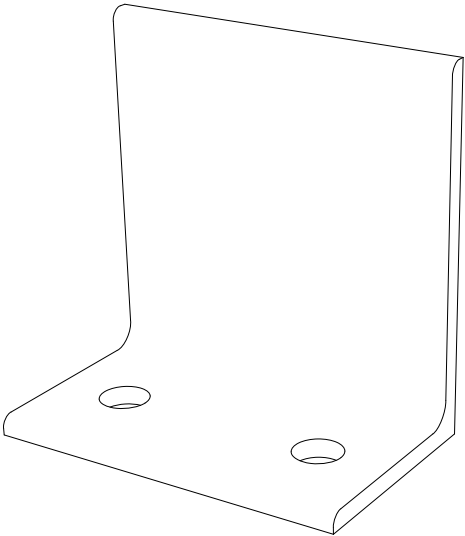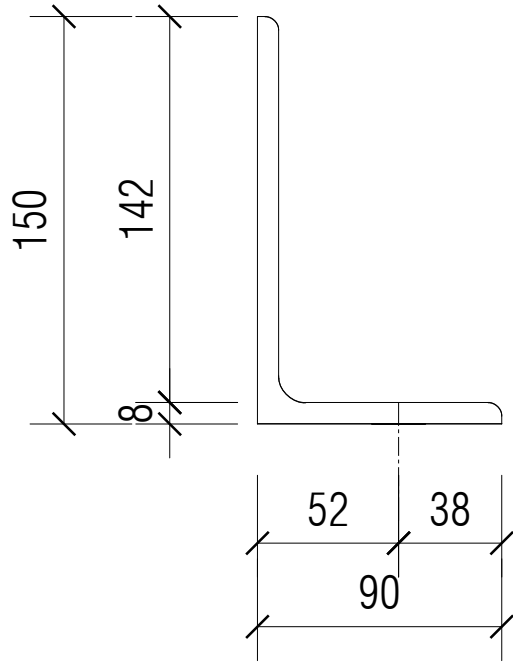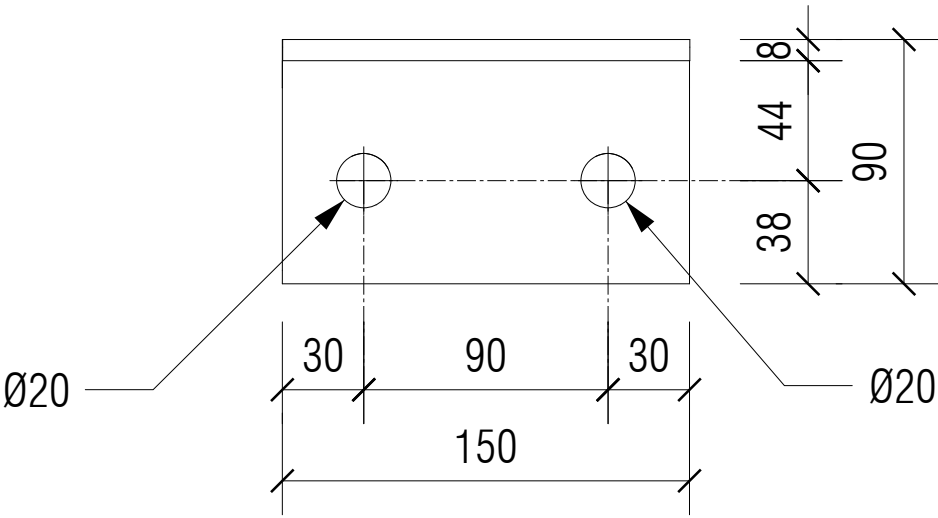

ITEM	QTY	MATERIAL	LENGTH	NOTE	FINISH
1	1	UA_150x90x8	150	2x Ø20 HOLES	REC PAINT
-	-	-	-	-	-
-	-	-	-	-	-

UNIT WEIGHT (kg)
2

 www.austruss.com.au (02) 4860 1400 DWG FILE: ####	DRAWN Mitchell.H Ph.02 4860 1426	ISSUE	DATE	DESCRIPTION OF REVISION	Client/Company Name		Project Name		Building / Zone / Area		Job Number	
		A	16/08/26	IFC	ADCO		Condell Park_CPHS		Zone 3 (Building 0 - Level 2)		24400	
		B	18/08/26	IFC								
					Project Address		Drawing Name		Drawing Number		Revision	
					Third Ave, Condell Park, NSW 2200		STRUCTURAL PRODUCTION		LGS-3-280		B	
					NOTE: USE PROVIDED DIMENSIONS ONLY. IF NOT PROVIDED, ASK.				Scale: NTS			