
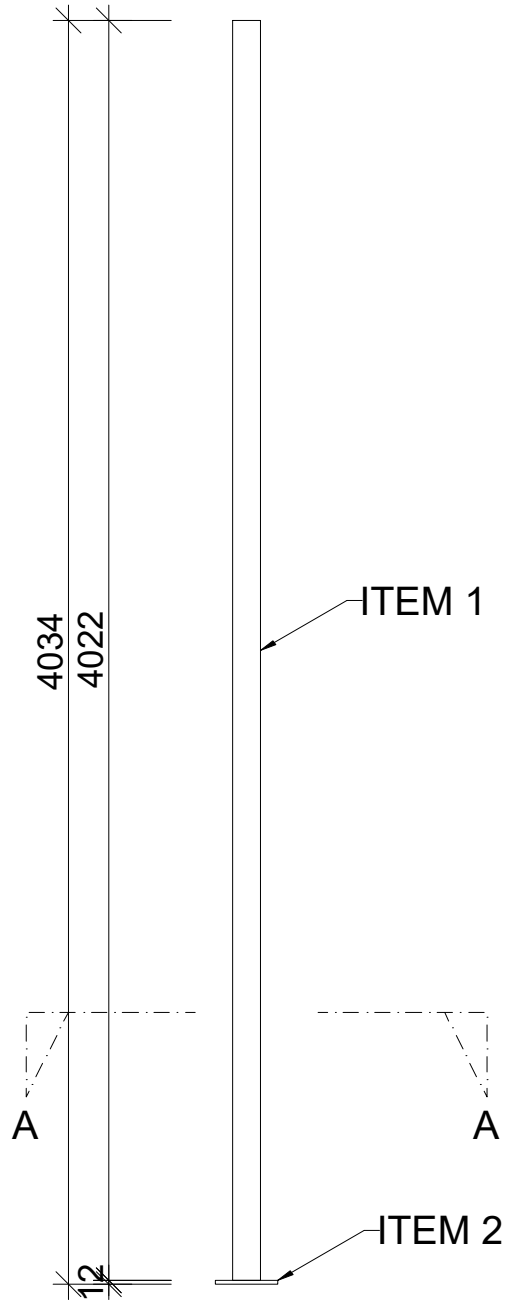


MARK	QTY	LENGTH (mm)	WEIGHT(kg)
P100	1	4043	40

	NAME	DATE	SIG.
FAB BY			
CHECK BY			

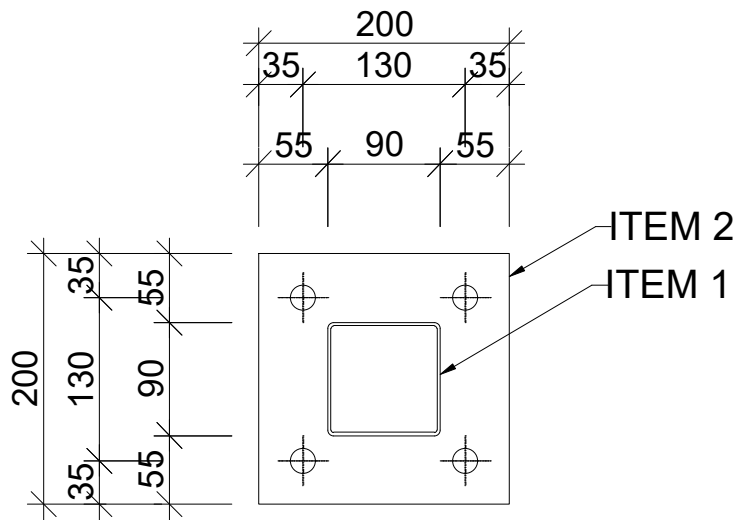


ITEM	QTY	MATERIAL	LENGTH	NOTE	FINISH
1	1	SHS_90 x 3.5	4022	WELD	HDG
2	1	PL_200 x 12	200	4 x 22 Ø_WELD	HDG
-	-	-	-	-	-
-	-	-	-	-	-
-	-	-	-	-	-
UNIT WEIGHT (kg)					40


 www.austruss.com.au (02) 4860 1400 DWG FILE: icad	DRAWN SD Ph:48601409	ISSUE	DATE	DESCRIPTION OF REVISION	Client/Company Name		Project Name	Building / Zone / Area		Job Number		
		A	10.07.26	IFC	PATERSON		NOWRA	BUILDING J		26018		
					Project Address		87 Jervis St. Nowra NSW 2541		Drawing Name		Drawing Number	Revision
					NOTE: USE PROVIDED DIMENSIONS ONLY. IF NOT PROVIDED, ASK.				Scale: 1 : 10	STRUCTURAL DETAIL		ST-190

MARK	QTY	LENGTH (mm)	WEIGHT(kg)
P101	1	3216	32

	NAME	DATE	SIG.
FAB BY			
CHECK BY			

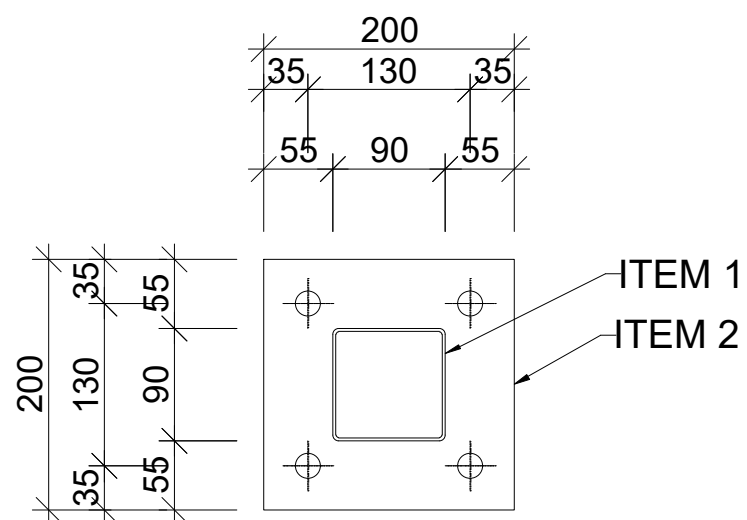

SECTION A-A


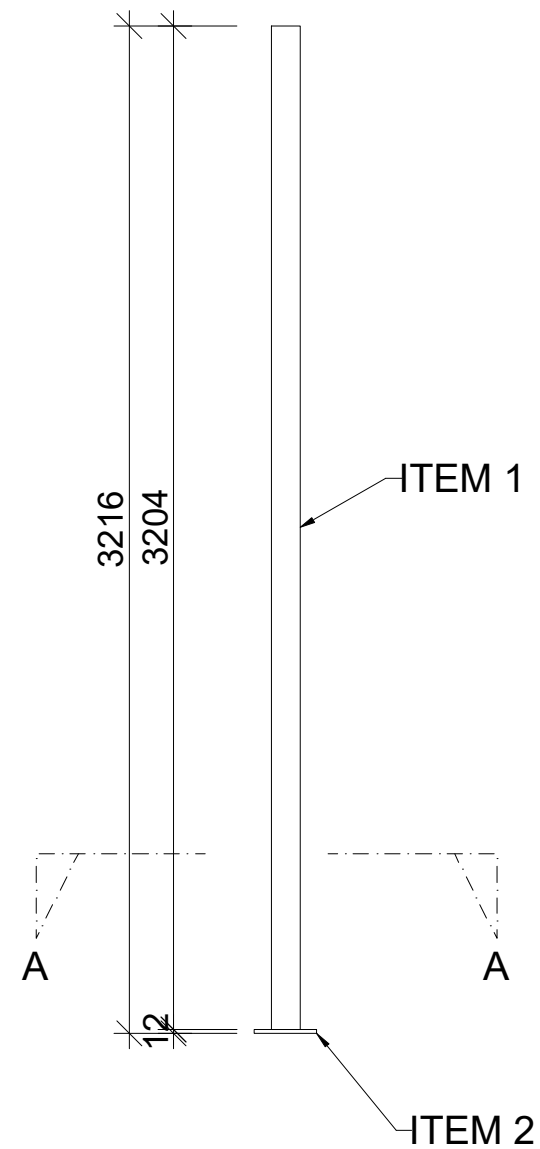


ITEM	QTY	MATERIAL	LENGTH	NOTE	FINISH	
1	1	SHS_90 X 3.5	3204	WELD	HDG	
2	1	PL_200 X 12	200	4 x 22Ø_ WELD	HDG	
-	-	-	-	-	-	
-	-	-	-	-	-	UNIT WEIGHT (kg)
-	-	-	-	-	-	32

 www.austruss.com.au (02) 4860 1400	DRAWN SD	ISSUE A	DATE 10.07.26	DESCRIPTION OF REVISION IFC	Client/Company Name PATERSON		Project Name NOWRA		Building / Zone / Area BUILDING J		Job Number 26018	
	Ph:48601409				Project Address 87 Jervis St. Nowra NSW 2541				Drawing Name STRUCTURAL DETAIL		Drawing Number ST-191	Revision A
					NOTE: USE PROVIDED DIMENSIONS ONLY. IF NOT PROVIDED, ASK.		Scale: 1 : 10					
DWG FILE: icad												

MARK	QTY	LENGTH (mm)	WEIGHT(kg)
RHS-150X50X3.0_BP	2	150	2

	NAME	DATE	SIG.
FAB BY			
CHECK BY			

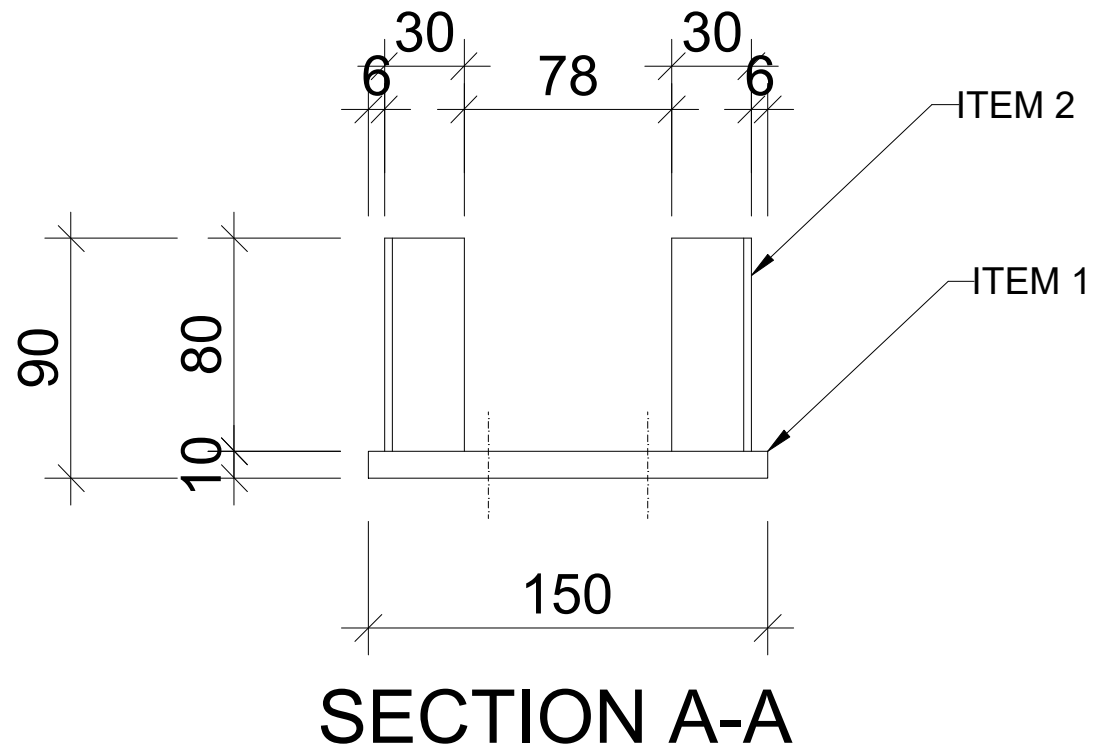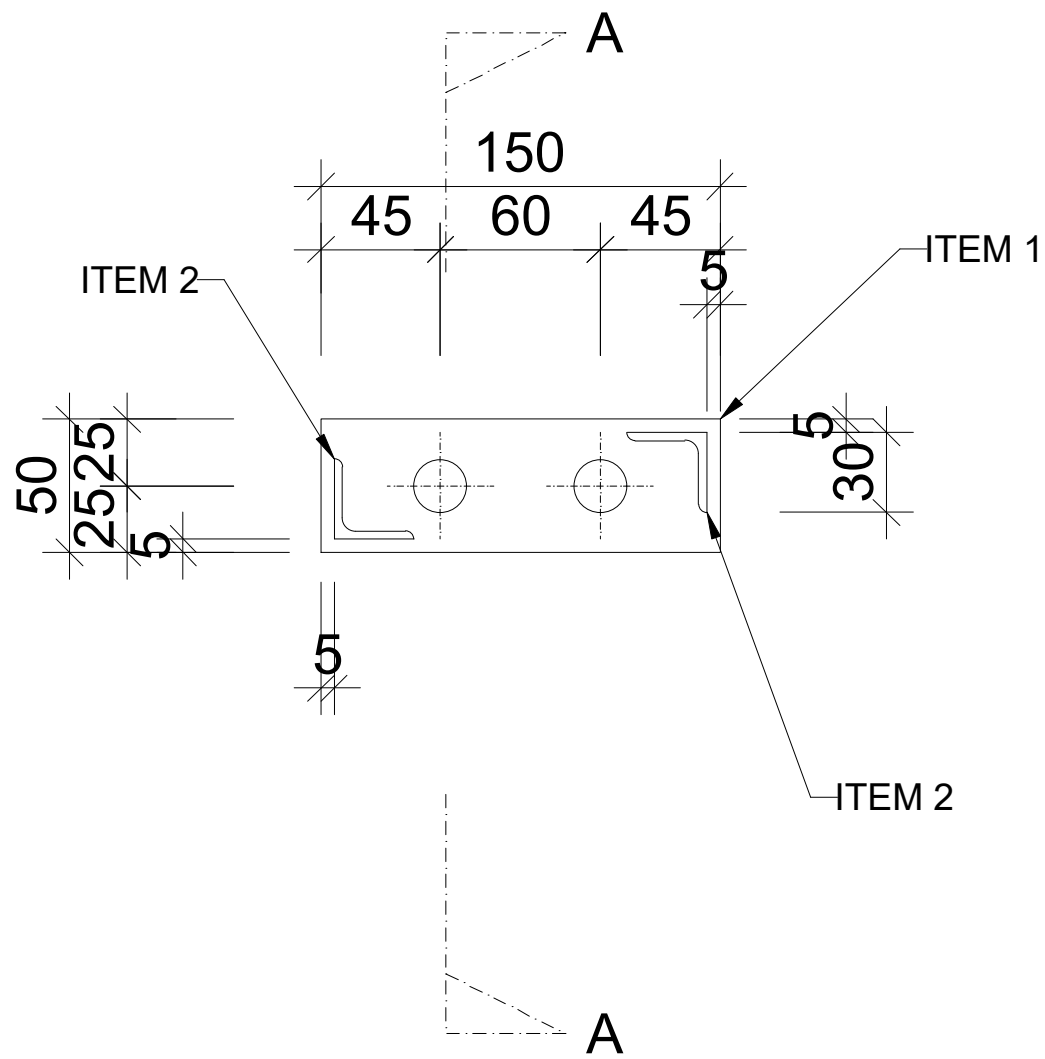

ITEM	QTY	MATERIAL	LENGTH	NOTE	FINISH
1	1	PL_150x12	50	2x20Ø	PAINT
2	2	EA_30x3.0	80	WELD	PAINT
-	-	-	-	-	-
-	-	-	-	-	-
-	-	-	-	-	-
UNIT WEIGHT (kg)					1

 AUSTRUSS www.austruss.com.au (02) 4860 1400 DWG FILE: icad	DRAWN SD Ph:48601409	ISSUE	DATE	DESCRIPTION OF REVISION	Client/Company Name		Project Name		Building / Zone / Area		Job Number	
		A	10.07.26	IFC	PATERSON		NOWRA		BUILDING J		26018	
					Project Address				Drawing Name		Drawing Number	Revision
					87 Jervis St. Nowra NSW 2541				STRUCTURAL DETAIL		ST-192	A
					NOTE: USE PROVIDED DIMENSIONS ONLY. IF NOT PROVIDED, ASK.				Scale: 1 : 10			